
专业协调01：分栋连厅与一层平面

两户各向外移1.00米；单栋不缩放。上层相对墙轴线x=13.80及15.80米，恢复2米间距。

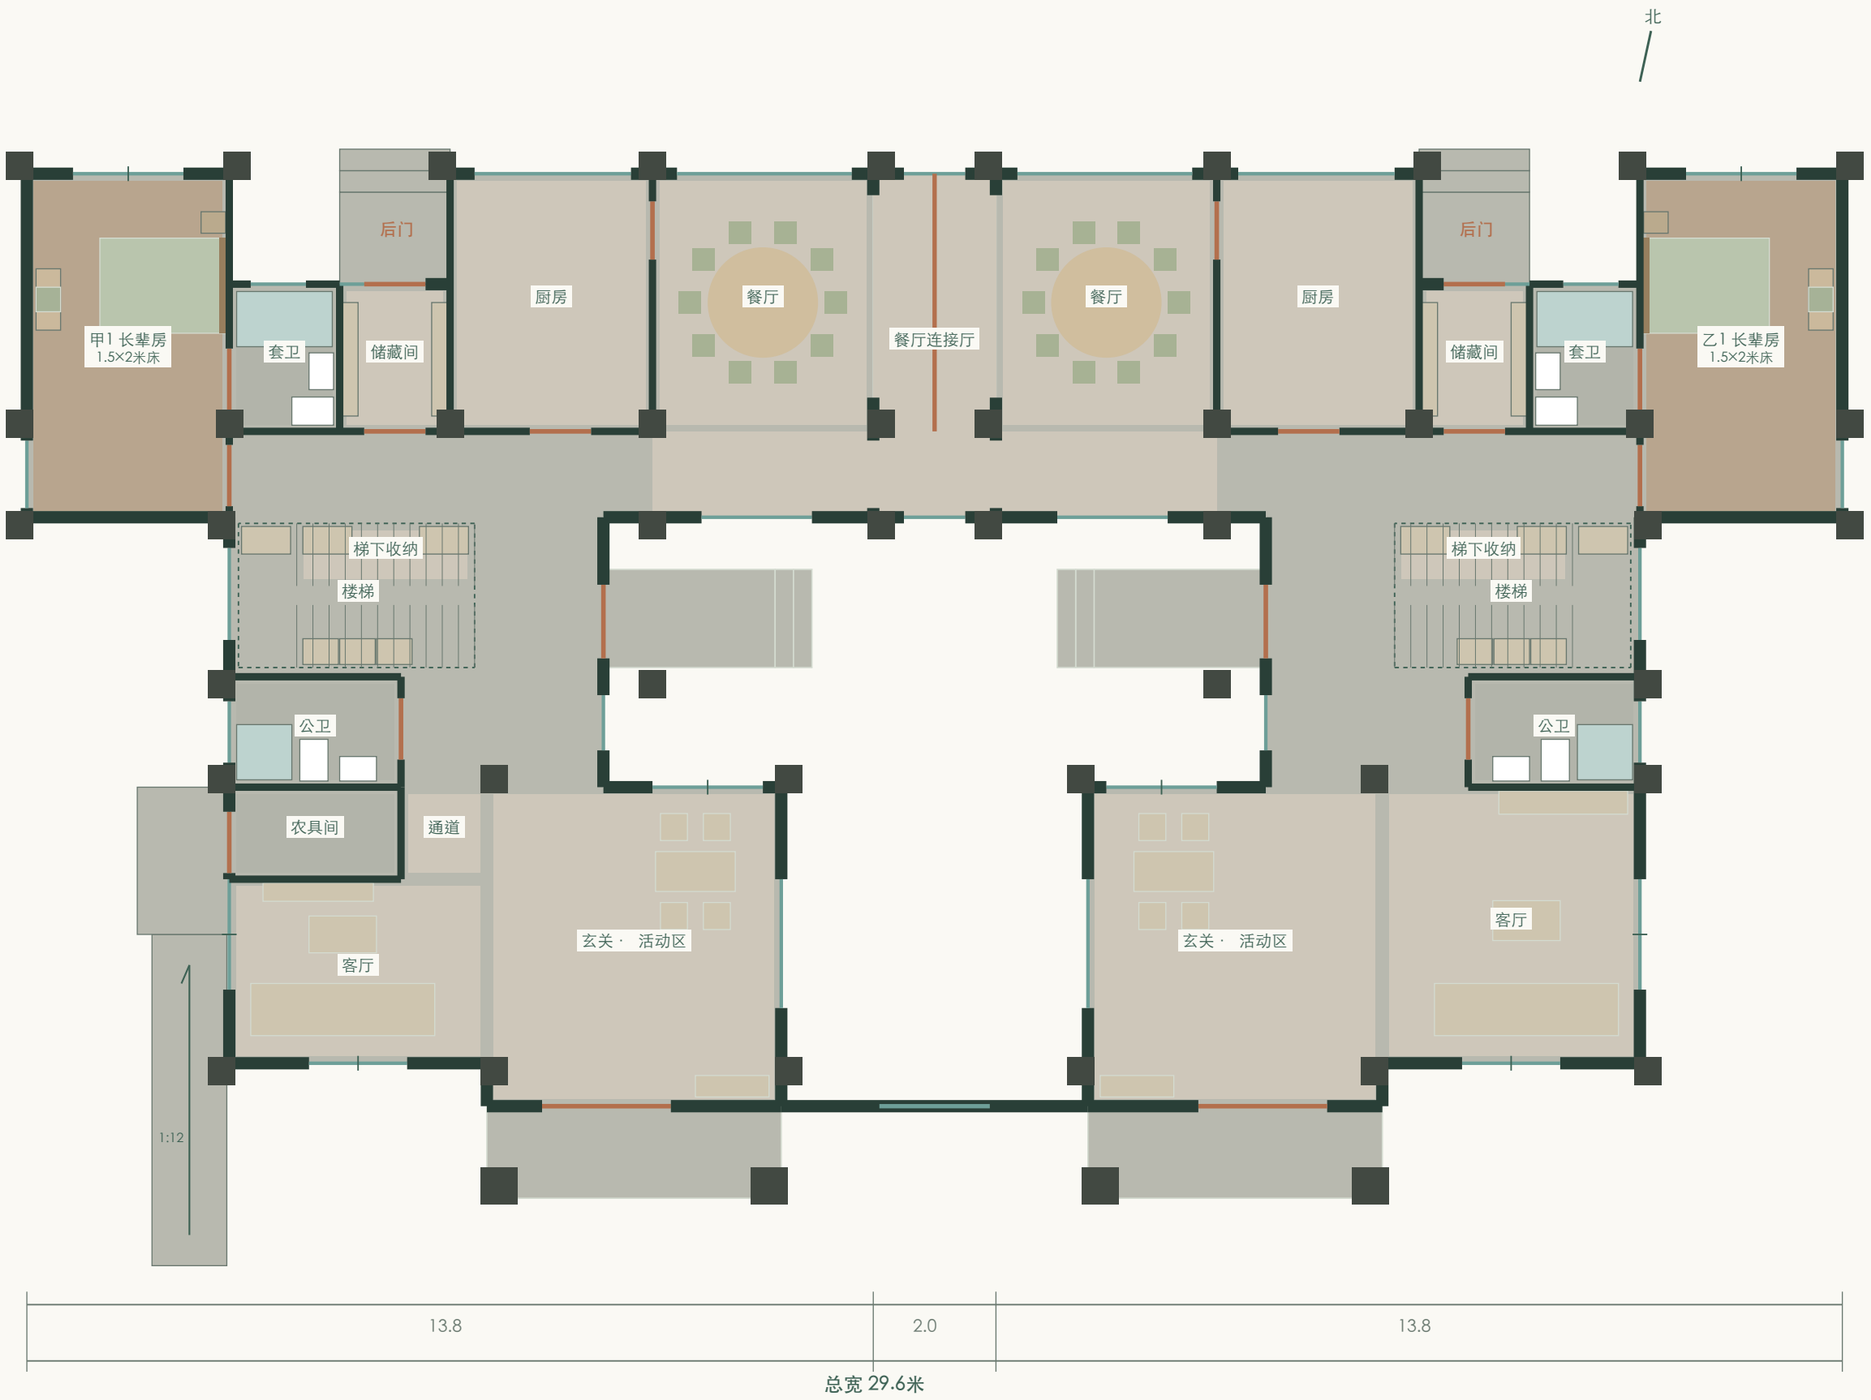

几何变更

层高3.90/3.30/3.30米；室外−0.45米，三级150毫米台阶。

总宽29.60米，单栋开间13.80米，中间2.00米。

一层保留2.00×5.60米连接厅及20席餐厅；二、三层中间不设楼板，相对端墙错位保留4扇窗。屋檐内侧外挑600毫米，中央余约800毫米开缝。

餐厅隔断线长4.20米，打开时屏风、端部短墙及横挡墙均不留在厅内；原柱保留，支承构造另定。

一层三角标记新增2处1.00米门洞；X侧门改窗；厨房旁空置区改储藏间，外后门位于北界y=14.90米，另设平台与三级台阶。


天井门洞1.20米，门外平台2.80×1.60米，门扇全开后模型余深超过1.50米；实际净尺寸按门窗深化复核。非施工图，未定配筋与基础。

专业协调02：二、三层临空边缘与屋面

蓝线为保留的露台栏杆；深灰为恢复的走廊墙，青绿为新窗；室内楼板范围保留，北侧增卧室小阳台；内侧主屋顶补600毫米挑檐。



二层：有顶走廊加墙，转折通道补顶，前露台敞开

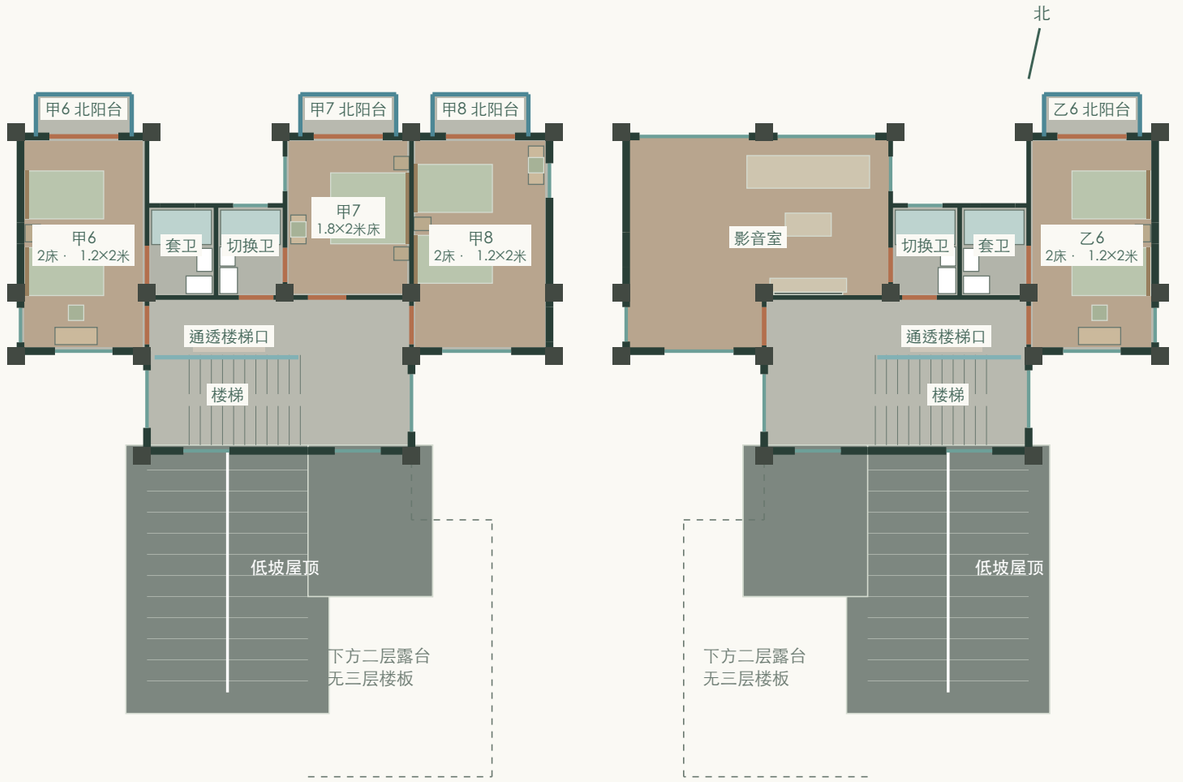

三层：走廊外墙保留，梯洞边改玻璃栏杆，低坡翼顶延伸

前部露台原8段栏杆保留，北侧卧室阳台各三面围护：0.35米暖灰轻质基座，上部哑光暖灰铜细竖杆与扶手，高度暂按1.20米建模；应复核实际完成面高度、竖杆间距、扶手、基座与边梁锚固。

后排主屋顶前坡约18°，楼梯并入连续坡面，二层卧室上方小顶左右约8°分坡，屋脊及侧檐向南约3°降低；三层前部原露台楼板全部取消，不将坡屋面作为可走露台。

相对内墙新增4扇错位小窗，连接厅前后补2窗。上层2米为墙轴线几何间距；实际净距、采光通风、防火及维护条件须正式核定。

专业协调03：门窗统计与结构待办

仅完成方案几何筛查。未确定结构体系、地勘、构件截面及配筋，不能放行施工。

本轮门窗与功能核对

卧室 / 卫浴	14间、21张床 / 14处（42件洁具）
厨房 / 日常餐厅	2间 / 2间，合厅20席
洗衣 / 储藏	每户二层洗衣间；甲户农具间、两户储藏间及梯下收纳
竖向标高	层高3.90/3.30/3.30米；室外−0.45米，三级150毫米台阶
窗总数	76处：12双扇、4四折、2固定配双侧窄扇、18固定配窄扇、14单扇、14上悬、12固定（8楼梯 + 2连厅 + 2天井门旁）
门总数	60处：46平开、10组通高玻璃推拉、4处卫浴贴墙推拉
中间新窗	4扇错位小窗、2扇连接厅窗
几何筛查	按平移后的原柱状符号复核，无洞口投影重叠；49处近柱提示

正式结构设计应落实

1. 原图保留柱位随两栋向外复位；二层露台8处多余柱段仍取消。两栋各自柱网及连接厅节点、基础与沉降策略须正式设计，不能将模型视为已定柱网。
2. 恢复围护的新增恒荷载、窗过梁、墙梁柱连接和下部支承；一层墙线与上层不重合，不能直接认定传力可行。
3. 餐厅联通处与原隔断墙线的屋盖支承；屏风不承重，原柱保留。
4. 主坡顶、低坡顶、檩条、屋架、檐沟及抗风连接。
5. 双扇外开窗的尺寸、五金、限位、玻璃和纱窗，以及室外通行净空。
6. 地基基础、重力、抗侧与抗震计算及签审图。

坐标表按分栋复位后的实际坐标输出：两户恢复原坐标，单栋尺度不变；中间墙轴线x=13.80和15.80米。门窗高度、洞口、栏杆与坡度均为方案意向；门窗表不能用于直接加工或施工。

下载逐洞口坐标及开启意向表（CSV）

专业协调04：地面材料与采购接口

色彩和规格为选材方向；具体产品须核实用途、吸水率、湿面适用与耐污维护资料。



客厅 / 餐厅 / 玄关 / 厨房

800×800毫米 / 暖米灰细石纹瓷质砖

暖米灰、细石纹、细腻哑光。客餐厅尽量连续铺贴，厨房选厂商明确适用的易清洁表面。



卧室 / 影音室

200×1200毫米 / 浅橡木色木纹瓷质砖

低饱和浅橡木色，顺直或不超过三分之一错缝；不做人字拼，避免偏橙、强木结。



天井 / 露台 / 开敞走廊

600×600毫米 / 暖浅灰室外石纹瓷质砖

暖浅灰、细防滑石纹；按室外湿区适用性选样，兼顾泥水清洁与排水。楼梯从同色系列裁制踏步。



卫浴 / 淋浴区

300×300毫米 / 暖灰卫浴防滑瓷质砖

暖灰细防滑砖，配近色灰缝；适用于赤脚湿区，便于围绕地漏找坡。

长条木纹砖错缝和砖缝按厂家及实物平整度确定；本图不承诺任一厂家产品已通过项目选材。开敞走廊与天井采用室外湿区适用面，淋浴区另核赤脚湿态性能。不能把单一摩擦系数或哑光外观当作所有场地的安全证明。

地坪完成面、地漏与找坡、防水、接缝及门槛一并协调；普通同色勾缝须耐污且适应使用环境，室外不得把所有缝刚性填死。瓷质砖日常用适配的中性清洁剂与清水维护；按厂家方法清除残留并避免长期积油、皂膜或泥水。

参考：TCNA湿区用途分类、Marazzi室外瓷砖与安装维护说明；均不替代中国项目正式设计及实际产品报告。

专业协调05：门饰面颜色表

位置与洞口详见门窗协调CSV；以下颜色用于协调，不作涂层、门芯或防火等级承诺。



入户门 / 2处

烟熏胡桃色 / #806A55



卧室及普通室内门 / 19处

浅灰橡木色 / #B2A087



卫浴门 / 18处

暖灰米色 / #B9B6AA



北侧后门 / 5处

深暖灰 / #666C63



天井 / 露台门框 / 16处

炭灰细框 / #414944

入户和后门按户外使用环境核对耐候、防腐与五金；卫浴按耐湿、清洁和门锁条件核对。门体材料、面层与安全性能分别确认，不能以效果图木色认定门芯或结构。

同一颜色在木纹膜、烤漆、金属和玻璃框上会产生不同光泽和观感，应以同一现场光线下的实样批准。

专业协调06：天井侧恢复墙与门窗布置

原有16处新增窗保留；玄关内部两门取消，二层门位保持；原门窗保留范围、二楼新门位、后排南向高窗及小屋顶见本轮说明；均为方案意向。

每户新增窗：宽 × 高 / 窗台高（米）

一层玄关北窗	1.80 × 1.45 / 1.00
一层侧走廊	1.50 × 1.85 / 1.00
一层中央南向窗	1.80 × 1.85 / 1.00
二层侧走廊	1.50 × 1.85 / 1.00
二层中央南向窗	1.80 × 1.85 / 1.00
三层侧走廊	1.50 × 1.85 / 1.00
三层中央南向窗	1.80 × 1.85 / 1.00
三层南端	1.20 × 1.50 / 1.35

每行甲、乙户各1处。后排南向高窗及8处天井侧窗窗头2.85米，固定主玻璃配窄开启扇；三楼小南窗的窄扇宽0.30米，其他天井窗0.45米。把手中心约1.50米。新洞口未与原柱状符号投影相交；该筛查不等于结构承载或抗震验算。

空间与实施核对

一层：玄关通楼梯门与内部隔墙取消，外侧北窗保留，避开转角窗开启范围，窗下不增柜体以保留活动桌拉椅空间。天井门洞1.20米，门外平台2.80×1.60米，后接三级150毫米高差；模型中门扇完全外开后仍有超过1.50米余深。两侧台阶之间约留2.00米通行。

二层：北端y=8.50米原露台门墙取消；卫浴旁x=7.50米设1.00米卧室侧门，南端y=6.70米设1.10米露台门。甲5、乙5旧入口及短隔墙拆除，卫浴门墙保留。转折通道已补低坡内翼屋顶，天井侧为墙，前露台仍用栏杆。

三层：原走廊尽端纳入卧室，既有南向窗保留，不设通向取消楼板处的门。

围护暂按200毫米外观建模，宜优先比选轻质墙；新增墙体荷载、边梁、连接、过梁与基础须结构设计确认。窗下及洞边实体段不能据本图认作已设计的构造柱。

统一炭灰窗框；外侧窗台排水、上口滴水、安全玻璃、限位、纱窗和实际净空须门窗深化。原低窗防护及全屋采光通风仍须整体核查，本页不作全屋合规结论。

协调依据：GB 55038-2025 第4.2.1条（公共走廊及开启窗）、第4.1.16条（临空外窗防护）、第4.2.7条（出入口与平台）。适用范围及项目落实由当地正式设计核定。

查看主管部门发布的规范摘录

专业协调07：复坡小屋顶与后排南向高窗

屋顶坡度及门窗尺寸仅为方案几何，未确定结构截面、玻璃及五金。



小屋顶：每片以局部x=5.40米起脊，左右各8°分坡；沿y方向另设约3°南向坡。前、后檐形成山墙轮廓，左右侧檐沟向南端汇水。后缘最高约1.03米，低于新南窗窗台1.35米；柱顶按同一坡面下延40毫米，避免穿出屋面。

低坡内翼：小屋顶右坡与内翼合成同坡面连续L形屋面，覆盖两户转折通道与新增洗衣间；不增加三层楼板，前露台及中央天井仍露天。取消内部檐沟与重叠补片，外围檐沟、泛水和滴水须深化。

后排南向高窗：原1.80米洞宽不动，窗台1.00米、窗头2.85米；主玻璃固定，0.45米侧扇外平开。不能把模型分格视为玻璃厚度或五金承载已定。

侧檐沟、落水、泛水、双锁边金属板与实际复坡排水路径须联合深化；型材、屋架、抗风与梁柱荷载须正式验算。各家屋面系统对坡度及密封有专门要求，按最终产品选型。

屋面构造参考：RHEINZINK Standing Seam Technology（非项目选材或中国标准替代）

专业协调08：四折大窗与本轮空间核对

平面模型协调，非五金加工图或结构计算。

四折窗清单 / 原洞口不变

甲户 / 1层 / 厨房	2.55 × 1.60米；窗台0.85米
甲户 / 1层 / 餐厅	2.85 × 1.60米；窗台0.85米
乙户 / 1层 / 厨房	2.55 × 1.60米；窗台0.85米
乙户 / 1层 / 餐厅	2.85 × 1.60米；窗台0.85米

本轮分栋与屋面协调

一层：玄关、客厅和楼梯之间的分隔门墙取消；公卫围墙、外墙及原柱保留，两端各补南端柱并贯通至屋顶。上部荷载不能依赖已删除的隔墙，须复核梁柱承载和传力。甲户客厅后角设农具间，电视贴新墙；乙户恢复完整客厅及原电视墙。两户沙发朝北。

二层：相邻双坡小顶向内侧延伸，转折通道有顶；边梁、轻屋面与泛水需正式设计。模型对二层房间和通道的980个采样点作竖向屋面射线检查，前露台保持露天。

侧窗：其余朝天井的侧窗沿用固定主玻璃配0.45米窄扇；一层门旁两侧窗改0.90×1.35米固定玻璃；甲7侧窗改为0.90×1.60米，与甲3一致。

折叠窗：四扇2＋2外折，端部窗扇约0.64至0.71米宽；重量、五金、轨道、耐候、限位、纱窗及洞边支承由产品及正式设计确定。模型动作不代替加工或结构性能核验。

四折窗在模型全开状态下，中间视线未被玻璃阻挡；左右堆叠仍占用端部空间，不能按整个洞口面积作为实际通风或消防有效开口。门窗表与本页须随选定厂家复核，不作直接订货依据。

专业协调09：三楼南窗、连续屋面与补柱

本页为方案位置与几何核对，新增柱及连接需正式结构设计。

四扇南向小窗 / 同一立面语言

每扇外框约1.20×1.50米；窗台1.35米、窗头2.85米，与中央高窗对齐。主玻璃约0.90米，窄分格约0.30米，两户镜像布置。

两扇楼梯窗保持固定，两块玻璃均不动且不设把手。两扇走廊窗仅窄扇向外开启；新窗不作为上人屋面出入口。

连续屋面后缘最高约1.03米，新窗下方留约0.32米模型间隙；实际窗台、泛水、完成面及安装公差须复核。

连续L形屋面 / 外围排水

主翼右坡与通道内翼共面，沿接边高度及法向一致。屋面没有原补片之间的坡度折线或内檐沟；锁边纹理连续，统一薄檐。

左右坡约8°，纵向向南约3°；排水沿L形外围组织。前露台和中央天井保持露天。屋面接墙泛水、檐沟容量、防结露、保温及抗风仍须正式设计。

两端侧墙每层各三柱。新柱位于南端转角，与原前排柱线对齐；新增柱参考原柱状符号外形，非已设计的截面或配筋。

柱位及上下衔接

原图128处柱段记录保留，取消的8处二层柱段及6处已无楼板的矮柱段不显示；新增两端南柱每户每层1段，共6段。模型共显示120段柱，新增柱脚落至室外铺地下50毫米；72处上层柱段逐一核对与下层衔接，顶层接主屋顶下皮。

新增柱不意味着基础和荷载路径已完成设计。结构人员应统一核定柱网、地基基础、梁柱连接、抗震与沉降策略，并把新增柱计入门窗洞口协调。

专业协调10：v4挑檐与餐厅界面

主檐600毫米，低檐550毫米；默认烟陶红；内侧600毫米挑檐分开收边，顶部约800毫米开缝。

主屋面外露边挑出约600毫米；二楼L形低屋面外露边挑出约550毫米。扩大外露檐口，保持原坡面和屋脊高度，采用约60毫米视觉薄檐、深阴影线及外围排水；接上层墙处采用泛水，不将屋面穿入室内。

v4恢复上层2米间距，一层保留2×5.6米连接厅。两户餐厅南侧3.60米轴线范围内的墙和门取消，连通长走廊；西、东端原柱保留；连接厅活动屏风打开时整块移走，取消中线短墙及横挡墙。地面同标高连续铺暖米灰室内砖；厨房界面、外侧玻璃围护保留。


挑檐悬挑、檩条、抗风连接、檐沟容量、滴水及屋面层厚度须联合设计。模型中的檐口和柱位只用于方案协调。餐厅墙移除时，上部荷载应由正式设计的梁柱体系承担，不能将移墙后的模型当作承载已获确认。

中间仅保留4扇0.90×1.60米磨砂单扇外开窗；甲栋留北侧、乙栋留南侧，窗台0.85米、窗头2.45米，其余4处封实。连接厅前后各补1.00×2.40米整片固定景窗，窗台0.55米、窗头2.95米。南端墙长5.00米、高2.20米，保留1.80米装饰花窗。屋檐落地黑色管线从外观模型移除，实际排水系统仍须正式设计。


二层洗衣、一层梯下半开放收纳

两户镜像设置；洗衣间双门连通，梯下为敞开入口、低柜、搁架与格栅。

二层洗衣间 / 1:30

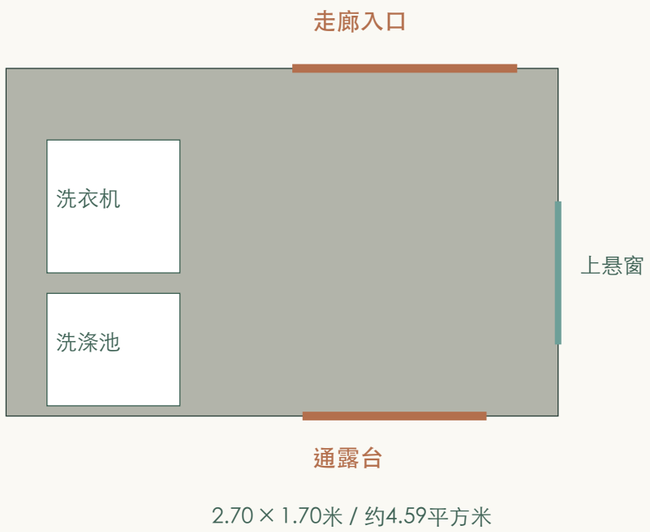

一层梯下半开放收纳 / 1:40

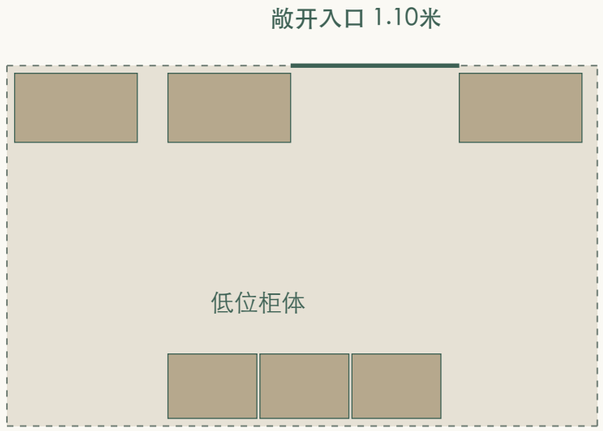

虚线为楼梯投影，入口不设门。

两侧低柜配开放搁架与疏朗木格栅。

洗衣间：每户二层露台北侧约4.59平方米，走廊与露台各一门；设备、门扇和侧窗保留。轻质围护、设备荷载、防水与排水须联合设计。

梯下收纳：取消门与整面封墙，北侧原楼梯隔墙同步取消，中央1.10米入口敞开。低处阶梯式带门柜，高处开放搁架，两侧浅灰橡木格栅轻遮挡；低矮处只放物品，不作站立通道。

农具入甲户专用房间，季节用品入各户储藏间；梯下以鞋、雨具、常用杂物为主。通风、防潮、照明及实际梯板下净高须深化。

北侧：只给卧室小阳台

二层6处，三层4处，共10处；影音室不加阳台，北窗采用双侧开启扇。




每处约2.50×1.10米，新增阳台投影共约27.5平方米。原1.80米洞口统一为2.45米高的双片玻璃推拉门。靠书桌侧固定，另一片平移收拢，模型通行口约0.82米；原洞宽不变；床与书桌按最新床型表调整。

栏杆统一哑光暖灰铜与暖灰薄基座。模型仅表达空间及外观；阳台悬挑、边梁、锚固、防水、排水、门槛及总造价须正式核定，未据此完成承载或合规验算。


卧室北侧门窗：整幅玻璃，同高细框

10组统一为1.80×2.45米通高推拉门；靠书桌侧固定，开启侧向其收拢。

闭合 / 两片完整玻璃

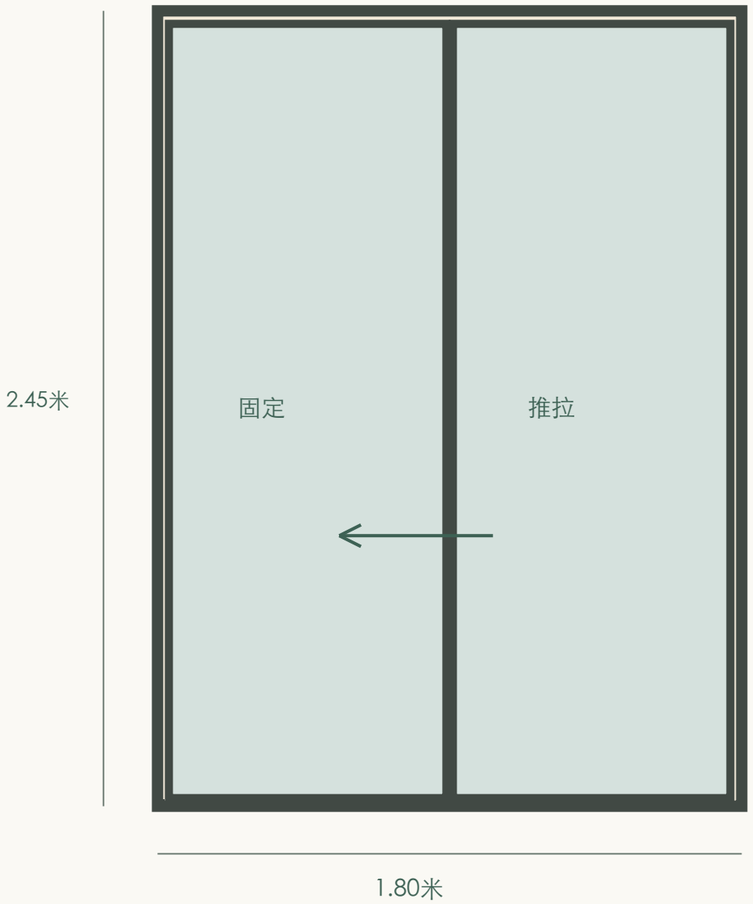

开启后 / 约0.82米通行口

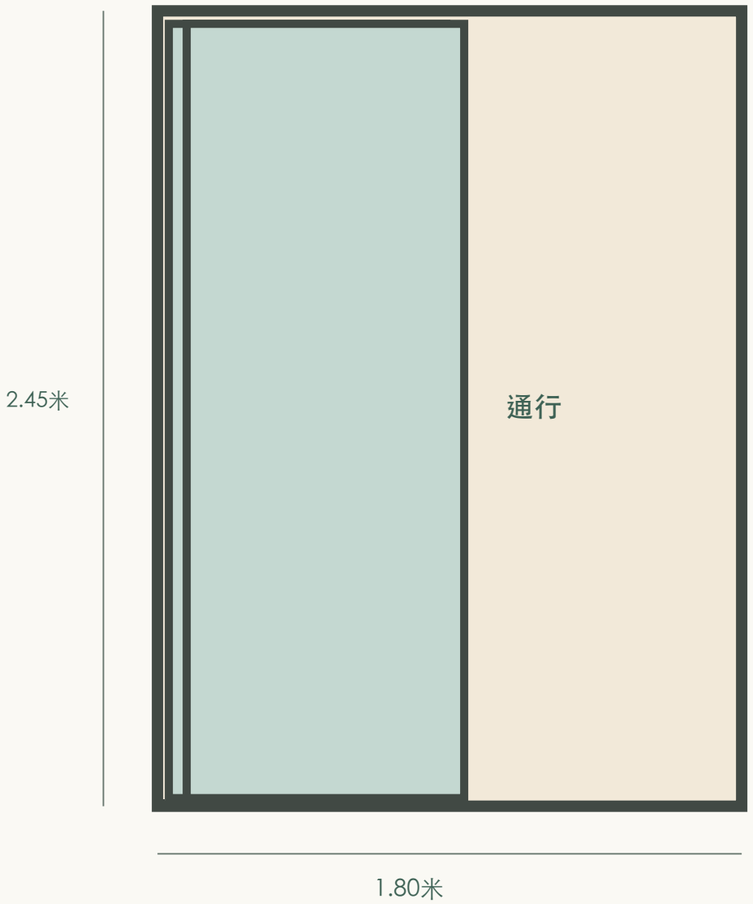

设计：整组同高、统一外框，仅留一道中央接缝，玻璃一直延伸至低轨。每间房按书桌位置镜像设置固定侧，推拉不占用室内及1.10米深阳台的门扇回转空间。

模型意向：外框约35毫米、扇框约25毫米、闭合中缝约70毫米，低轨约20毫米，模型通行口约820毫米；均不是成品加工或验收尺寸。

采用配套外门系统，实际净开口、安全玻璃、密封、五金、纱门、轨道清洁、门外截水与阳台找坡由门窗深化及施工图共同落实。原洞口位置及宽度保留，不据此认定结构验算已完成。

一层：农具、干储分开，生活动线保持敞开

甲户设农具间约4.20平方米；两户各设储藏间约4.32平方米，乙户恢复原客厅。房屋轮廓不变。

甲户农具间 2.80 × 1.50米




室外直接进出 · 1.00米门洞

只取甲户客厅后部外侧角落，甲户电视移到新增隔墙前；乙户该处恢复客厅，取消农具外门、平台与缓坡。农具从甲户侧院进出。

门外平台1.50×2.40米。推车缓坡净宽1.10米、长5.40米，跨越450毫米高差。

坡度1:12，侧缘设低挡边；场地、排水、防滑及成品净空待深化。

每户储藏间 1.80 × 2.40米

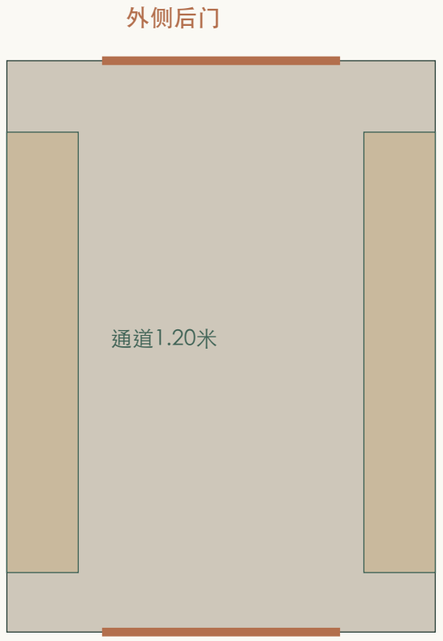

由室内进入

利用厨房旁原空置服务区，保留室内入口，北端新增外后门和高位通风窗；两侧约300毫米深搁架，中间1.20米模型通道。外门后为1.50米深平台与三级150毫米台阶。

宜存干货、折叠椅、节庆用品和清洁物料。农药、燃油等不与食品混放；喷雾器清洗、晾干后入农具间。

面积为轴线范围估算；净尺寸以正式设计为准。卧室14间、卫浴14处、厨房2间、日常餐厅2间及合厅20席保留。

季节与时间：拖动看光影

右侧两条连续滑杆；连接厅改整片固定景窗，三楼梯洞边改玻璃栏杆。

右侧控制 / 北京时间

季节



时间




拖动季节，连续查看全年太阳位置；拖动时间，观察早晚方向、日照色温、阴影长度及夜间亮度变化。分享链接会保留所选季节与时间。

坐标：北纬26.745458°，东经112.056528°；北京时间UTC+8。沿用建筑南偏东约12.31°朝向，阳光按真北计算。

模型展示晴天太阳位置与几何遮挡；缺少实测山体、邻房和天气资料。剖切、隐藏屋顶或降低墙体时，界面标为“剖切光影示意”，不能据此判断实际室内采光。

太阳位置方法：NOAA通用方程

连接厅固定景窗

 


1.00 × 2.40米

连接厅前、后各一片固定玻璃，窗台0.55米、窗头2.95米；细框、无把手，不能点击开启。

三楼取消楼梯北侧整面隔墙；透明栏杆沿梯洞边设置，旁侧上楼出口保持敞开。走廊外墙、原柱和楼梯固定窗保留。

固定玻璃及栏杆的安全玻璃、构造、承载与锚固须正式设计。日照功能是方案展示工具，不是报审或规范日照分析。


三楼楼梯玻璃栏杆

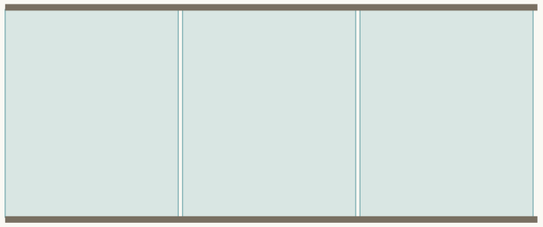

模型高度1.20米

三楼影音室：向天井侧南扩为L形

原约28.98平方米，增加约5.04平方米至34.02平方米；沿前排两柱围合，右侧公共走廊保留。

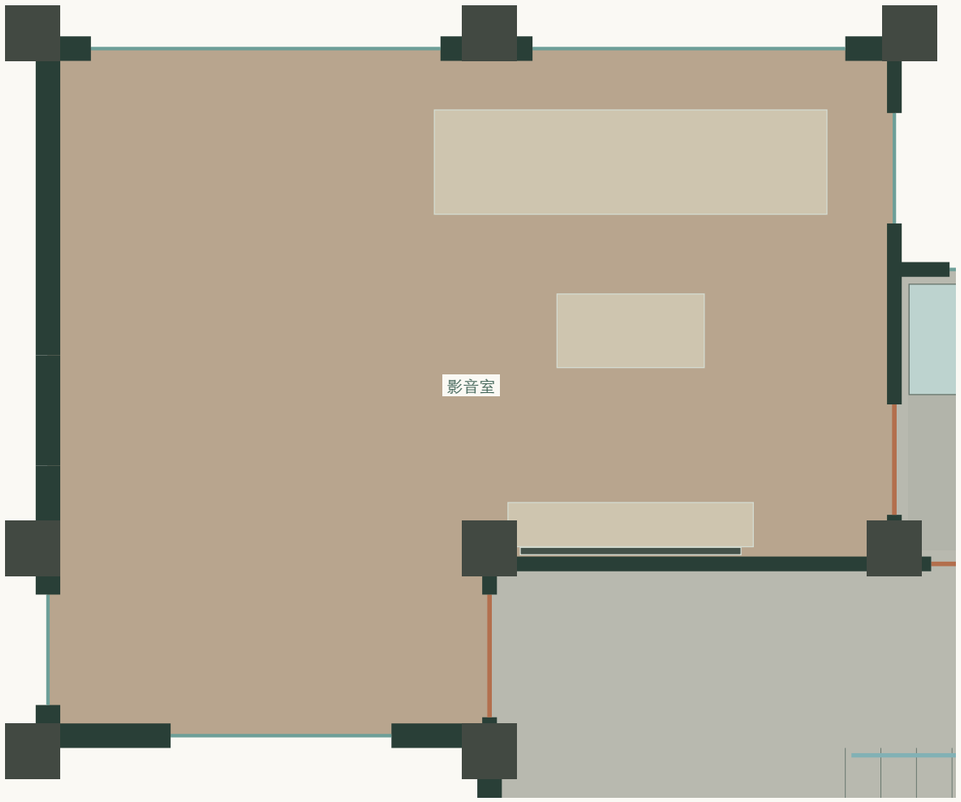

三层乙户局部 / 1:50（A3原尺寸打印）

墙、门、窗与家具一起调整

1. 拆旧南墙靠天井约3.60米的一段及原门；两柱之间形成新的南向围护，转角侧墙闭合，影音室保持独立。

2. 南窗恢复原1.80×1.85米分格，窗台1.00米、窗头2.85米；固定主玻璃配0.45米外开窄扇。其余5扇后排南向高窗沿用原分格。

3. 新入口位于转角侧墙，门洞1.00米，向影音室内开，避开楼梯到达及公共卫浴通道。

4. 电视贴右侧保留实墙，沙发与电视对正；原北向四折大窗、可切换卫浴及其双入口保留。

5. 不增楼板，不改屋顶或柱位；扩入部分由原楼板与主屋面覆盖。拆墙性质、梁下净高及新增围护荷载须正式核定。

地面连续采用浅橡木色木纹瓷质砖；转角扩出的区域可作自由活动空间。图示为同一模型平面，未据此完成结构承载或隔声设计。

14间卧室：七间双床，其余按房型配床

床垫长统一2.00米；七间双床房共14张1.20米床，全屋共21张床。门洞、卫浴及阳台保留。

房间	床垫规格（宽×长）	床头抽屉柜 / 宽×深	书桌（长×深）
甲1 / 1层	1张1.50×2.00米	1只 / 0.40×0.35米	1.00×0.40米
乙1 / 1层	1张1.50×2.00米	1只 / 0.40×0.35米	1.00×0.40米
甲2 / 2层	2张1.20×2.00米	1只 / 0.40×0.45米	1.10×0.45米
甲3 / 2层	1张1.80×2.00米	2只 / 0.40×0.35米	0.75×0.40米
甲4 / 2层	2张1.20×2.00米	1只 / 0.45×0.35米	1.00×0.40米
甲5 / 2层	1张2.00×2.00米	2只 / 0.45×0.35米	1.20×0.60米
乙2 / 2层	2张1.20×2.00米	1只 / 0.40×0.45米	1.10×0.45米
乙3 / 2层	1张1.80×2.00米	2只 / 0.40×0.35米	0.75×0.40米
乙4 / 2层	2张1.20×2.00米	1只 / 0.45×0.35米	1.00×0.40米
乙5 / 2层	1张2.00×2.00米	2只 / 0.45×0.35米	1.20×0.60米
甲6 / 3层	2张1.20×2.00米	1只 / 0.40×0.45米	1.10×0.45米
甲7 / 3层	1张1.80×2.00米	2只 / 0.40×0.35米	0.75×0.40米
甲8 / 3层	2张1.20×2.00米	1只 / 0.45×0.35米	1.00×0.40米
乙6 / 3层	2张1.20×2.00米	1只 / 0.40×0.45米	1.10×0.45米


1.20米为常见成品床垫宽度，不是必须统一采用的法定标准。薄床架外包长约2.05米、宽比床垫多约50毫米，采购时须按实际床架复核。

甲3、乙3、甲7各用一张1.80×2.00米床；甲2、乙2、甲4、乙4、甲6、甲8、乙6各用两张1.20×2.00米床，并列布置。每间卧室标签显示床垫尺寸。床头均有完整实墙，床头柜各两只抽屉；双床房共用柜，书桌及北阳台路线保留。成品家具与完成面净距须现场复核。


成品规格示例：IKEA中国120×200厘米床垫（非产品指定）

灯光：以灯带、局部灯具与低位光组织空间


卧室、客厅和影音室不用中央大吸顶灯；暖灰铜灯体、浅米灯罩，窄灯槽与常规型材控制施工复杂度。

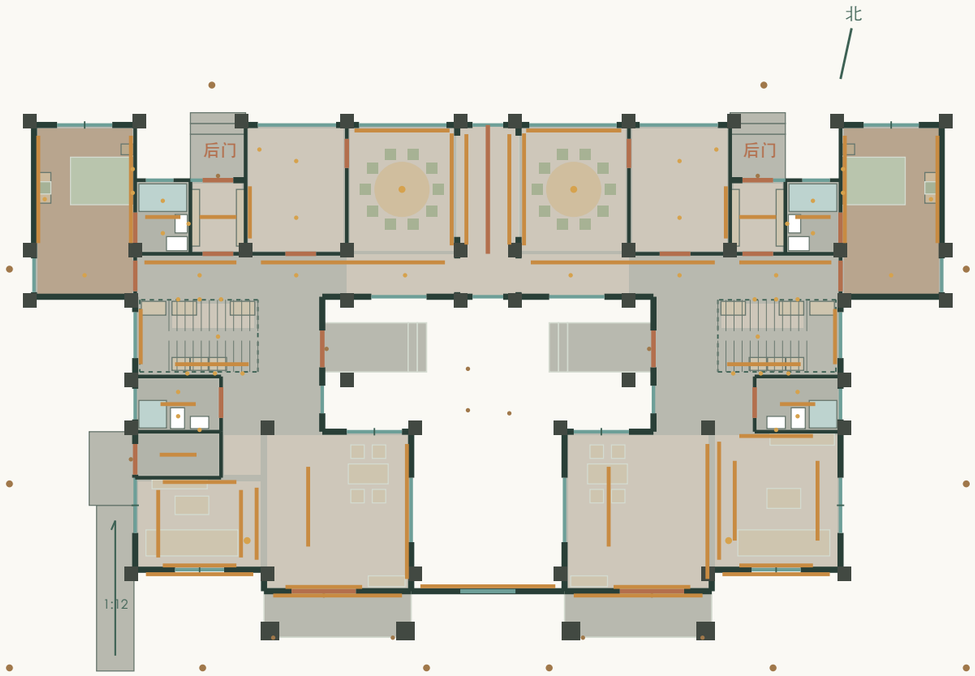

一层：客餐厅、厨房、庭院与入户路径

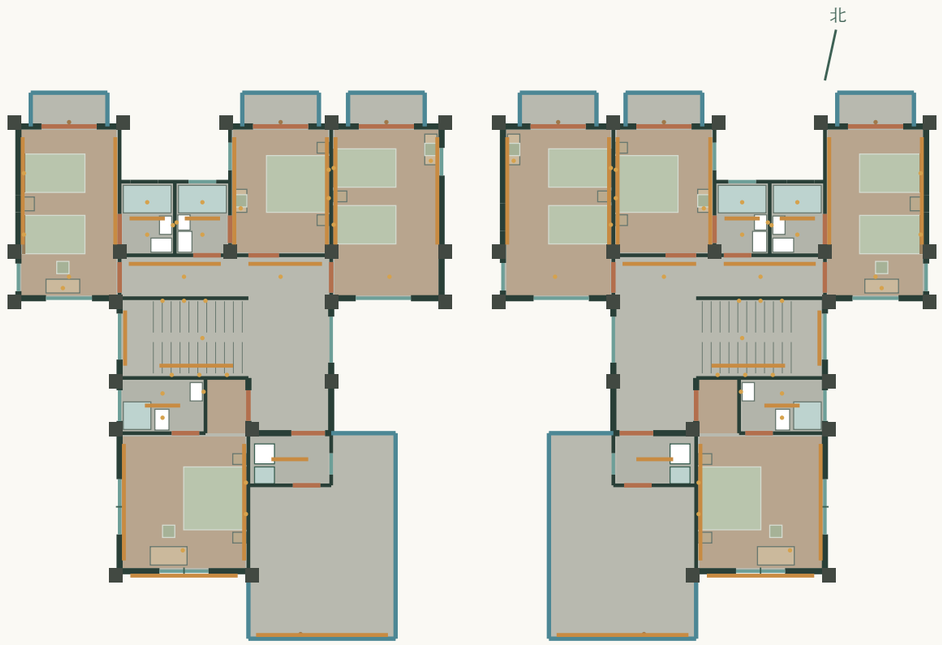

二层：卧室、阅读、洗衣与阳台

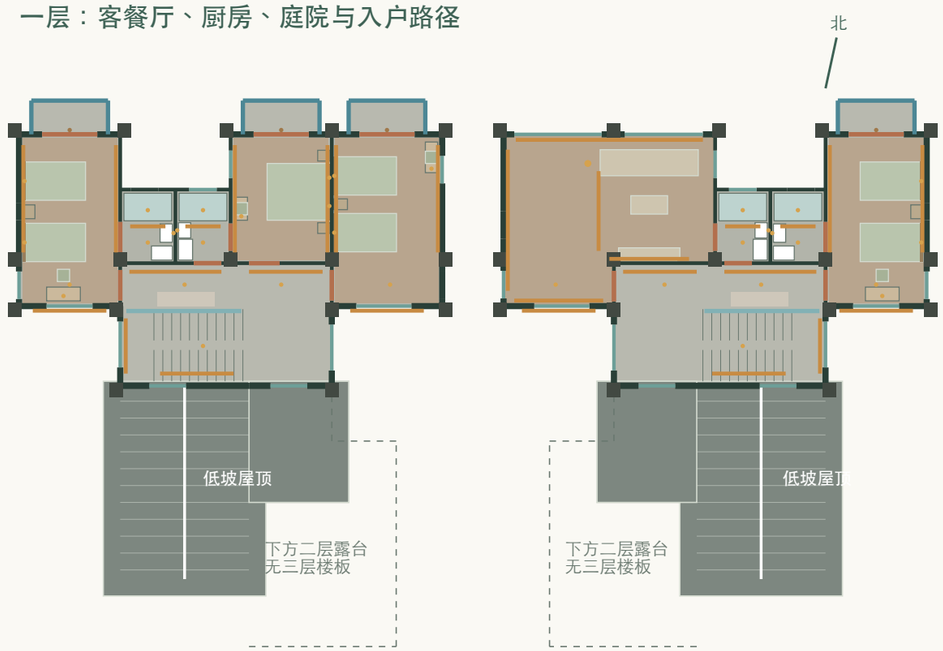

三层：卧室与影音室分层照明

用光与操作

金色线：隐藏灯带与工作灯；圆点：局部灯具及低位导光。图示按同一模型位置输出，非照明施工图。

卧室与室外保留2700K暖光；客餐厅、玄关、影音室及卫浴主体采用3000K，书桌与厨房工作光3000K。床头阅读灯、台灯及3只落地灯独立使用，实际分路调光。

走廊连续线光与楼梯平台、踏步灯采用3000K；入户、露台、12只路径灯、3只树灯及花窗墙分层补光。室外选防眩、耐候产品，排水、线管与供电保护由正式设计落实。

右侧“夜景”切换至20点，也可滑动时间；灯具在傍晚渐亮，白天熄灭。夜景由Cycles计算遮挡与反射，网页固定烘焙；隔断移开工况，无照度、眩光或电气验算。

下载中文概念灯位表（坐标与色温）

9间侧卧室：沿柱线改门，纳入走廊尽端

二层平面作为示例；一层2间、二层4间、三层3间。建筑外轮廓、原柱和外窗保留。

二层：绿色区域纳入卧室，橙色为新侧门



绿色区域每间进深1.40米，来自原有顶走廊尽端；不新增建筑外轮廓。

公共通道仍连接楼梯、卫浴与其余卧室。原14间卧室、14处卫浴及21张床保留；移墙后的传力、隔墙锚固及门框与柱边关系由正式设计复核。

轴线面积对照（平方米）

卧室	原面积	调整后	增加
甲1（一层）	13.9	18.5	+4.6
乙1（一层）	13.9	18.5	+4.6
甲2（二层）	13.9	18.5	+4.6
甲4（二层）	15.1	20.2	+5.0
乙2（二层）	13.9	18.5	+4.6
乙4（二层）	15.1	20.2	+5.0
甲6（三层）	13.9	18.5	+4.6
甲8（三层）	15.1	20.2	+5.0
乙6（三层）	13.9	18.5	+4.6

新侧门洞口暂按1.00×2.35米；南侧铰接，向卧室内开，门口地面平接。门框安装后的实际净宽、柱边收口及五金须正式深化。

床、书桌、床头实墙、卫浴及北阳台入口保留。卧室地面连续铺木纹瓷砖，走廊灯带在新墙处截断并重新分区。

南北向墙线（模型坐标）

甲1／2／6：x=3.30米；乙1／2／6：x=26.30米。


甲4／8：x=10.20米；乙4：x=19.40米。

各新门y=11.28～12.28米；隔墙暂按120毫米。

四间双床房与错位采光窗

甲2、乙2、甲6、乙6调整；21张床、14间卧室与14处卫浴。影音室仅改北侧两扇大窗。

侧卧室南窗：1.50×1.85米

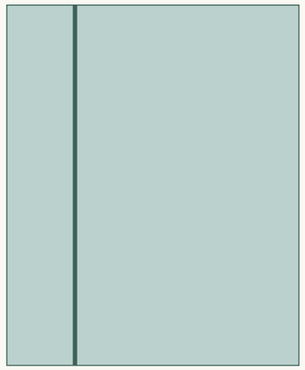

350毫米窄扇向外开启

窗台1.00米、窗头2.85米，与中间景窗齐平。两侧墙垛各约0.90米。主体玻璃固定，窄扇独立外开。


四间各两张1.20×2.00米床；甲户床头向西、乙户床头向东，均靠外侧实墙。

外侧仅保留正对卧室门的一扇0.90×1.60米窗，原床间窄窗封实；双床共用床头柜；南窗下设1.10×0.45米书桌。床脚侧约1米通道，北阳台前约0.8米模型间距，成品与完成面须复核。

影音室北窗：中间固定、两侧开启



2.85×1.60米

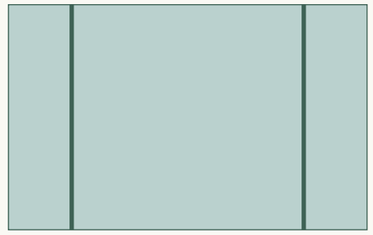

2.55×1.60米

原北窗洞口宽高保留，左右开启扇各0.45米，中间大块玻璃固定；两侧窄扇分别向外平开。南侧1.80米窗保持现有分格。

中间相对窗：甲北、乙南，共4扇



二、三层各按同样错位布置：甲栋保留北侧，乙栋保留南侧，其余4扇封实。

留下4扇统一900×1600毫米磨砂单扇外开窗，窗台850毫米、窗头2450毫米。

对应套卫封窗与排风

四间双床房各自对应的套卫封闭原小窗，公共及可切换卫浴窗保留。普通侧开窗把手中心统一约1.45米，原明确1.50米的保留。

预留独立机械排风至屋面，避免直接向对窗凹槽排气；风量、管径、止回、防水和检修由机电深化。

原柱及建筑外轮廓未改；新增窗洞的过梁、玻璃与五金需正式设计。

公共房间与卫浴：让空间本身明亮

客餐厅与影音室采用间接光和偏置线性光；14处卫浴均补漫射环境光，不以单个中央大灯照亮全屋。



客厅：柔和墙面与环境光





餐厅：灯带与局部餐桌光



影音室：L形空间连续补光

卫浴：宽光束、镜前光与漫射线光

三层影音室与卫浴补平吊顶，模型下皮3.15米；不改变层高与外屋顶。图为同一模型Cycles计算，非照度、眩光或电气验算。灯带、镜前及淋浴灯建议分路调光；功率、配光、湿区防护与吊顶节点须深化。