# 祁东县双桥镇厚南村双户住宅

## 图纸目录及建筑方案总说明

专业方案深化参考版

非施工图，不得据此放线、下料或施工

### 一、图纸目录

| | | |
|---|---|---|
| 建方-01 | 图纸目录及建筑方案总说明 | 本图 |
| 建方-02 | 一层定位及功能平面 | 1:100 |
| 建方-03 | 二层定位及功能平面 | 1:100 |
| 建方-04 | 三层及露台定位平面 | 1:100 |
| 建方-05 | 屋面与排水意向平面 | 1:100 |
| 建方-06 | 入户立面及天井剖面 | 1:125 |
| 建方-07 | 长辈房、卫浴及楼梯布置 | 1:40 / 1:50 |
| 建方-08 | 房间统计与主要门窗洞口建议 | 表格 |
| 建方-09 | 二十人聚餐布置与流线验证 | 1:40 |
| 建方-10 | 预算控制及施工图深化任务 | 表格 |

### 二、已确认的方案边界

两户独立生活；共14间卧室、14处卫浴、2间厨房、2间日常餐厅；每户一层、三层各设1间洗衣房。首层保留长辈房，春节约20人共同用餐；天井露天，前部低屋面作为分户露台；二百万元为含室内、设备及庭院的总费用上限。

### 三、统一图示约定

1. 主要平面比例1:100，图幅A3按原尺寸打印。平面尺寸为毫米，标高为米。
2. 定位轴线为本方案坐标依据，来源于原始示意尺寸，尚非实测施工定位轴线。
3. 主墙暂按200、隔墙暂按120表示，不能据此确认承重体系或材料。
4. 黑色方块表示原方案主要开间的结构协调点，柱尺寸、位置和传力体系均须结构复核。
5. 门窗编号与洞口仅供方案协调，不作订货及下料依据。
6. 室内面积为方案包络估算，非审批、产权或结算建筑面积。

### 四、制图与技术依据

表达组织参考《房屋建筑制图统一标准》GB/T 50001-2017、《建筑制图标准》GB/T 50104-2010。上述标准用于图面组织，不表示本项目已完成全部规范审查。

正式设计应结合项目适用范围核定《住宅项目规范》GB 55038-2025、《民用建筑通用规范》及无障碍、防水、防火、节能、结构和设备等现行要求；湖南及祁东地方规定应一并核对。

### 五、设计深度与使用范围

#### 01 可以用于

家庭及设计团队讨论、建筑方案比选、空间与房间数量核对，以及向当地团队说明拟询价范围。

#### 02 不能用于

本套不是建筑、结构、给排水、电气等专业齐全且经签审的施工图，不能直接交施工队开工、现场放线、配筋、下料或订购门窗。

#### 03 原因

现有资料仅有四张平面与场地示意，缺实测地形、法定用地界线、地勘、结构体系、专业计算和机电设计。编制中未虚构上述参数或签章。

#### 04 项目手续

湖南官方资料对限额以上自建房提出勘察、设计及审查等要求。是否纳入及最新办理流程须由祁东属地主管部门核定。

**官方资料链接（可点击）**

制图统一标准发布公告

建筑制图标准：出版社现行目录

住宅项目规范发布公告

湖南自建房勘察设计及监管官方答复

编制阶段：建筑方案深化参考；结构、设备及场地条件尚未核定。

尺寸单位：平面与洞口为毫米，标高为米；不得量图替代标注尺寸。

本套未含结构及机电施工图；正式设计、审查与签审由具资质单位完成。


| | | | |
|---|---|---|---|
| 项目：祁东双户合院 | 图号：建方-01 | 图幅：A3 | 2026.10.26 |
| 图名：图纸目录及建筑方案总说明 | 比例：见图内标注 | 版本：02 | 签审：待完成 |

# 祁东县双桥镇厚南村双户住宅

## 一层定位及功能平面

专业方案深化参考版

非施工图，不得据此放线、下料或施工

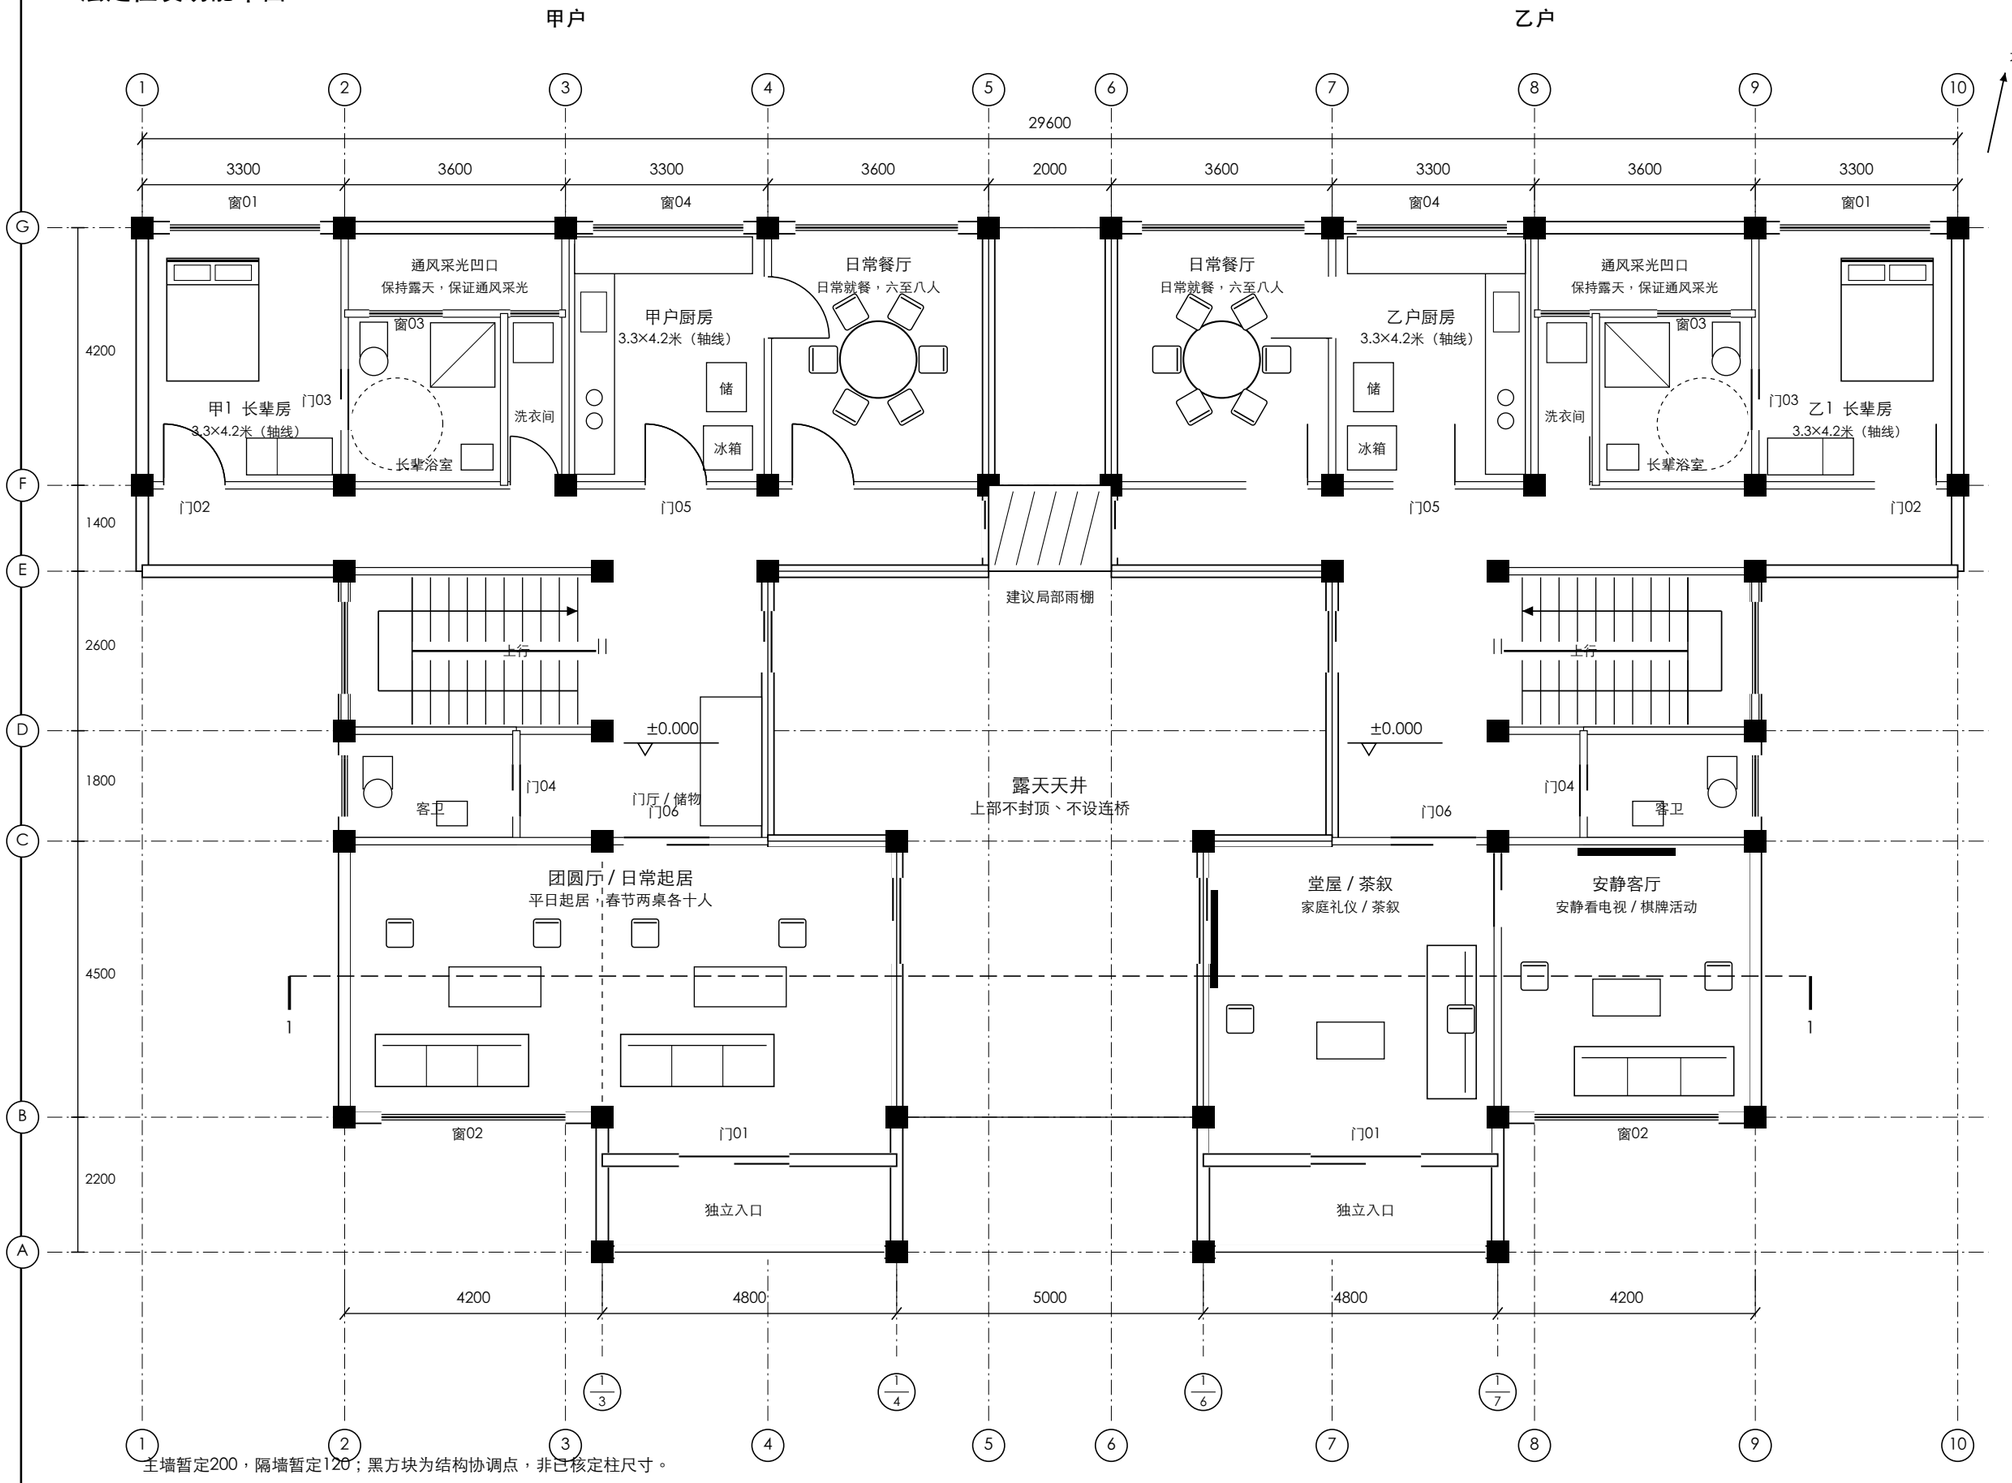


## 本层核对要点

### 01 卧室数量

甲1、乙1，共两间，均作为首层长辈房。

### 02 长辈卫浴

从各自卧室进入，轴线参考尺寸2600×2800；通行和洁具按建方-07复核。

### 03 团圆厅

甲户客厅与堂屋连通。虚线为拟调整分隔，不代表可拆承重墙。

### 04 地坪与入户

±0.000为方案假定。须由实测标高确定绝对标高及平顺入户。

### 05 局部雨棚

跨度约2000，覆盖约2.8平方米，规划与结构均待核定。

门窗编号为主要洞口类型示意，见建方-08。

*北向仅依据原图估读。

轴线圆圈与尺寸仅供本方案协调，正式定位须在实测总平面上核定。

主墙暂定200，隔墙暂定120；黑方块为结构协调点，非已核定柱尺寸。

编制阶段：建筑方案深化参考；结构、设备及场地条件尚未核定。

尺寸单位：平面与洞口为毫米，标高为米；不得量图替代标注尺寸。

本套未含结构及机电施工图；正式设计、审查与签审由具资质单位完成。


| 项目：祁东双户合院 | 图号：建方-02 | 图幅：A3 | 2026.10.26 |
|---|---|---|---|
| 图名：一层定位及功能平面 | 比例：1:100 | 版本：02 | 签审：待完成 |

# 祁东县双桥镇厚南村双户住宅

## 二层定位及功能平面

专业方案深化参考版

非施工图，不得据此放线、下料或施工

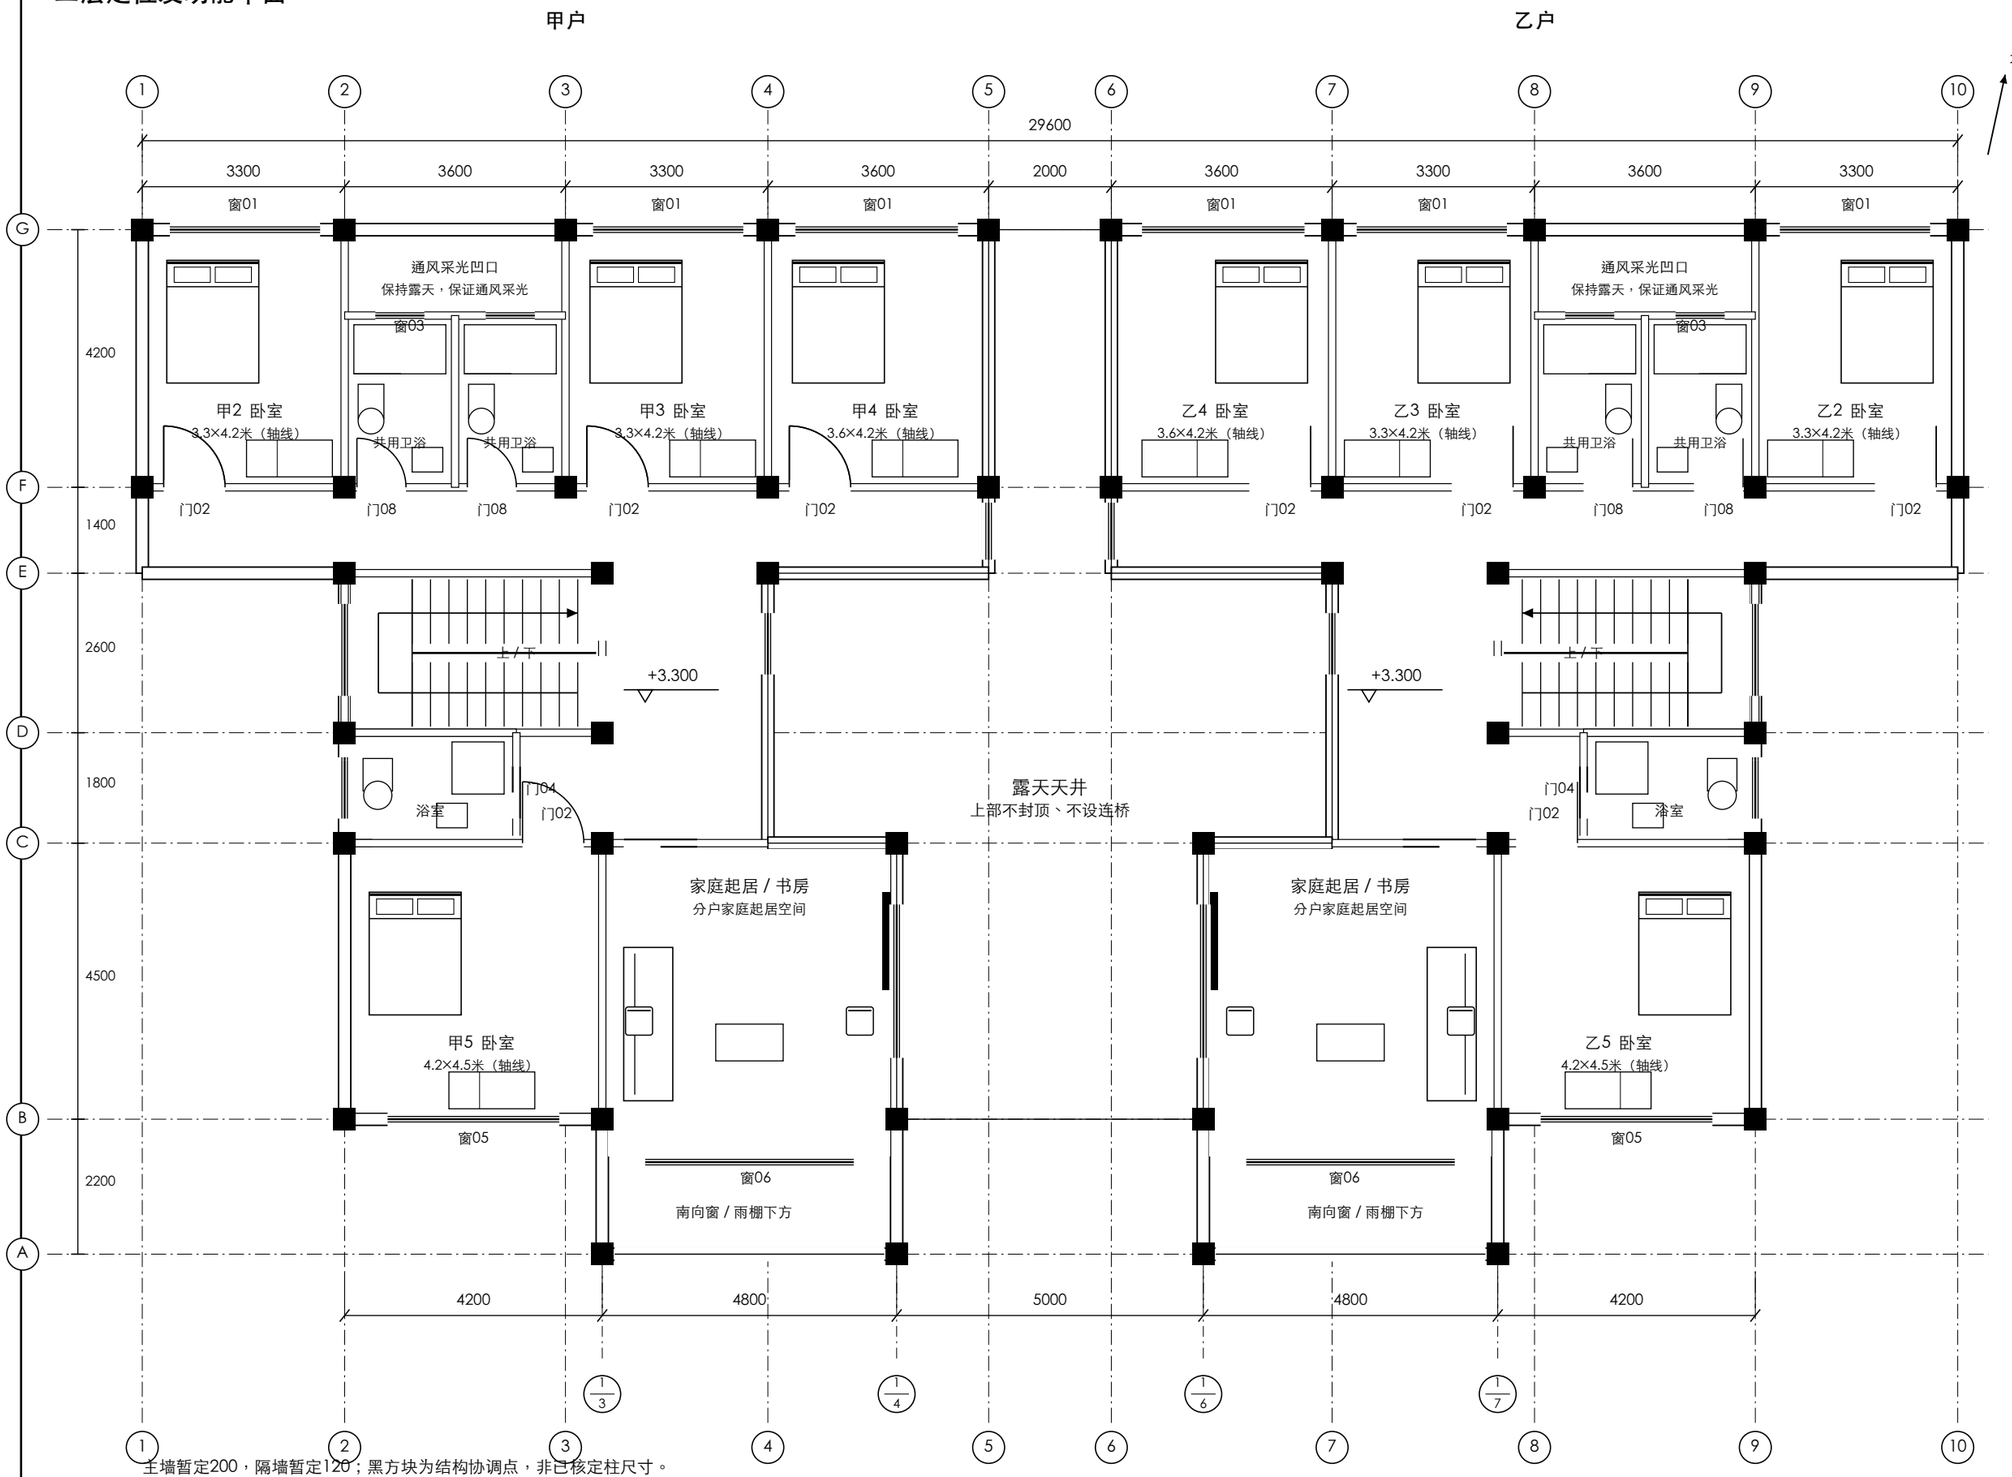


主墙暂定200，隔墙暂定120；黑方块为结构协调点，非已核定柱尺寸。

## 本层核对要点

### 01 卧室数量

甲2至甲5、乙2至乙5，共八间。

### 02 卫浴数量

每户后部两间约1800×2800共用卫浴，另有楼梯侧一间，共六间；均从公共空间进入。

### 03 楼梯

首层至二层升高暂按3300，二层至三层暂按3100；踏步和净空须专业复核。

### 04 分户使用

前部保留各自家庭起居室；不减卧室，洗衣房集中在一层、三层。

### 05 天井

天井露天，不增设跨院楼板或连桥。

门窗编号为主要洞口类型示意，见建方-08。

*北向仅依据原图估读。

轴线圆圈与尺寸仅供本方案协调，正式定位须在实测总平面上核定。


| | | | |
|---|---|---|---|
| 编制阶段：建筑方案深化参考；结构、设备及场地条件尚未核定。<br>尺寸单位：平面与洞口为毫米，标高为米；不得量图替代标注尺寸。<br>本套未含结构及机电施工图；正式设计、审查与签审由具资质单位完成。 | 项目：祁东双户合院 | 图号：建方-03 | 图幅：A3 | 2026.10.26 |
| | 图名：二层定位及功能平面 | 比例：1:100 | 版本：02 | 签审：待完成 |

# 祁东县双桥镇厚南村双户住宅

## 三层及露台定位平面

专业方案深化参考版

非施工图，不得据此放线、下料或施工

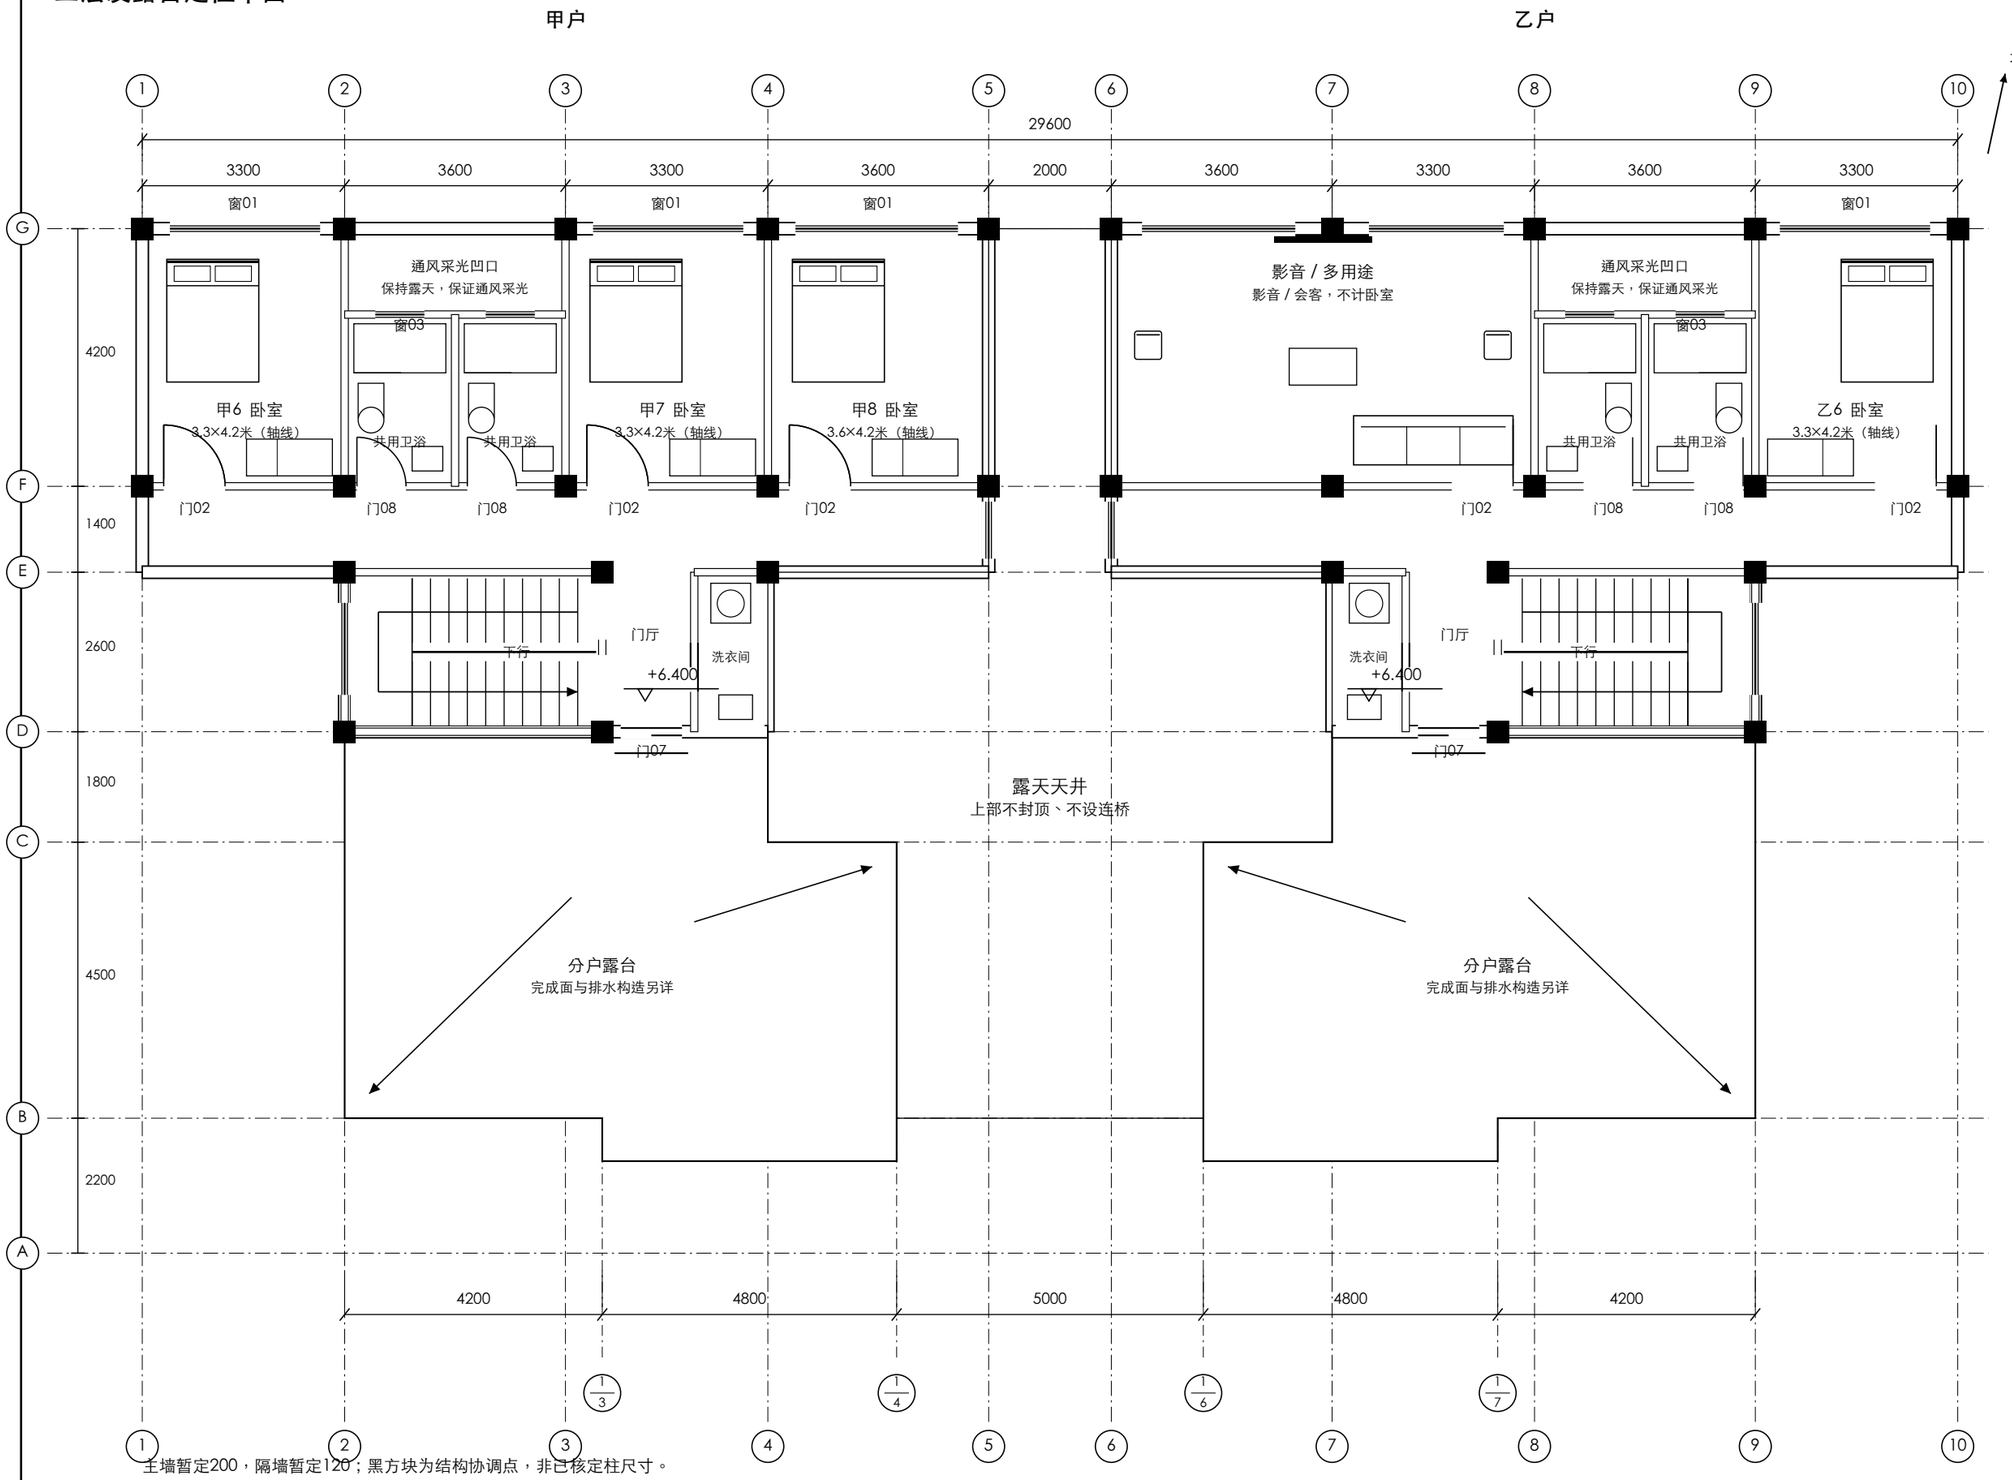


主墙暂定200，隔墙暂定120；黑方块为结构协调点，非已核定柱尺寸。

## 本层核对要点

### 01 卧室数量

甲6至甲8共三间，乙6一间，合计四间。

### 02 公共卫浴

每户两间约1800×2800共用卫浴，均从后走廊进入。

### 03 独立洗衣房

每户门厅外墙侧设约1200×2600洗衣房；门厅余宽约1500轴线，须复核实际净宽、门扇及设备检修。

### 04 露台围护

围护高度、构造、节点及抗水平荷载设计待核定。

### 05 标高含义

+6.400为参考标高；露台门调整至约1000宽，防水构造另定。

门窗编号为主要洞口类型示意，见建方-08。

*北向仅依据原图估读。

轴线圆圈与尺寸仅供本方案协调，正式定位须在实测总平面上核定。

编制阶段：建筑方案深化参考；结构、设备及场地条件尚未核定。

尺寸单位：平面与洞口为毫米，标高为米；不得量图替代标注尺寸。

本套未含结构及机电施工图；正式设计、审查与签审由具资质单位完成。


| 项目：祁东双户合院 | 图号：建方-04 | 图幅：A3 | 2026.10.26 |
|---|---|---|---|
| 图名：三层及露台定位平面 | 比例：1:100 | 版本：02 | 签审：待完成 |

# 祁东县双桥镇厚南村双户住宅

## 屋面与排水意向平面

**专业方案深化参考版**

非施工图，不得据此放线、下料或施工

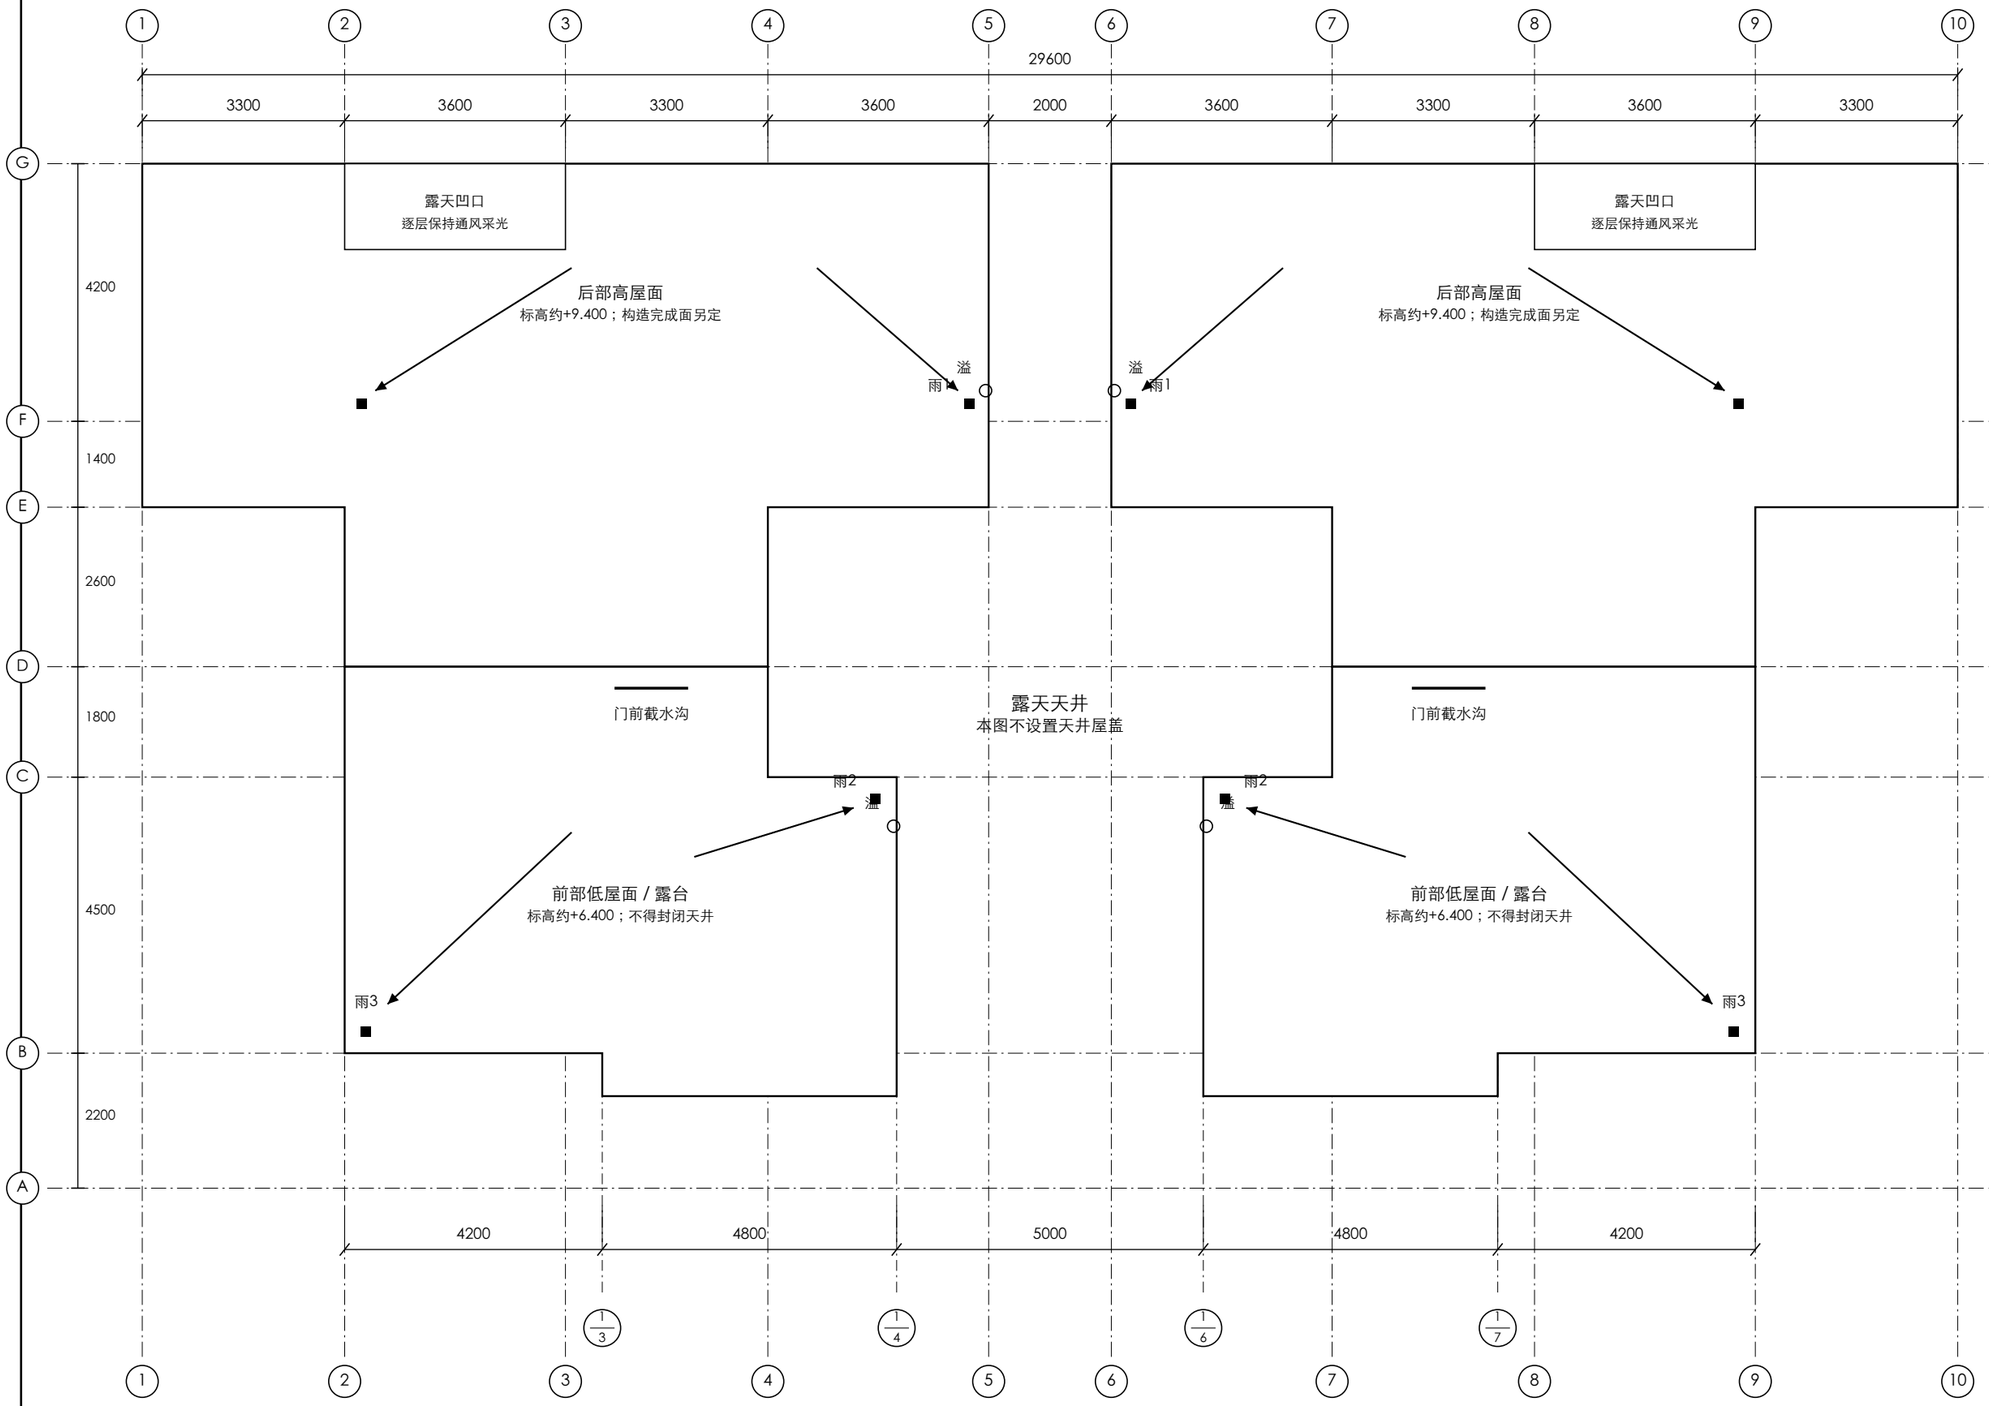


## 屋面深化要求

### 01 图示仅为排水组织意向

雨1至雨3为排水口类型位置示意，未作暴雨强度、汇水面积及管径计算。

### 02 完成面排水

深化各排水分区、坡度、找坡层厚度、雨水口与天沟；不得依据箭头直接施工找坡。

### 03 应急溢流

“溢”为独立溢流意向。位置、数量、标高与能力须由建筑及给排水专业共同核定。

### 04 露台门口

门前截水沟、防水上翻与平顺出入须统一设计；不可通过无控制抬高门槛处理渗水。

### 05 排放与维修

落水路径、排放点和高屋面检修到达方式尚待确定，不向邻地或基本农田随意排水。

### 06 安全围护

围护高度、可攀爬性、连接及荷载，须结合适用规范另行核定。

编制阶段：建筑方案深化参考；结构、设备及场地条件尚未核定。

尺寸单位：平面与洞口为毫米，标高为米；不得量图替代标注尺寸。

本套未含结构及机电施工图；正式设计、审查与签审由具资质单位完成。

| 项目：祁东双户合院 | 图号：建方-05 | 图幅：A3 | 2026.10.26 |
|---|---|---|---|
| 图名：屋面与排水意向平面 | 比例：1:100 | 版本：02 | 签审：待完成 |


# 祁东县双桥镇厚南村双户住宅

## 入户立面及天井剖面

专业方案深化参考版

非施工图，不得据此放线、下料或施工

### 南向入户立面 1:125

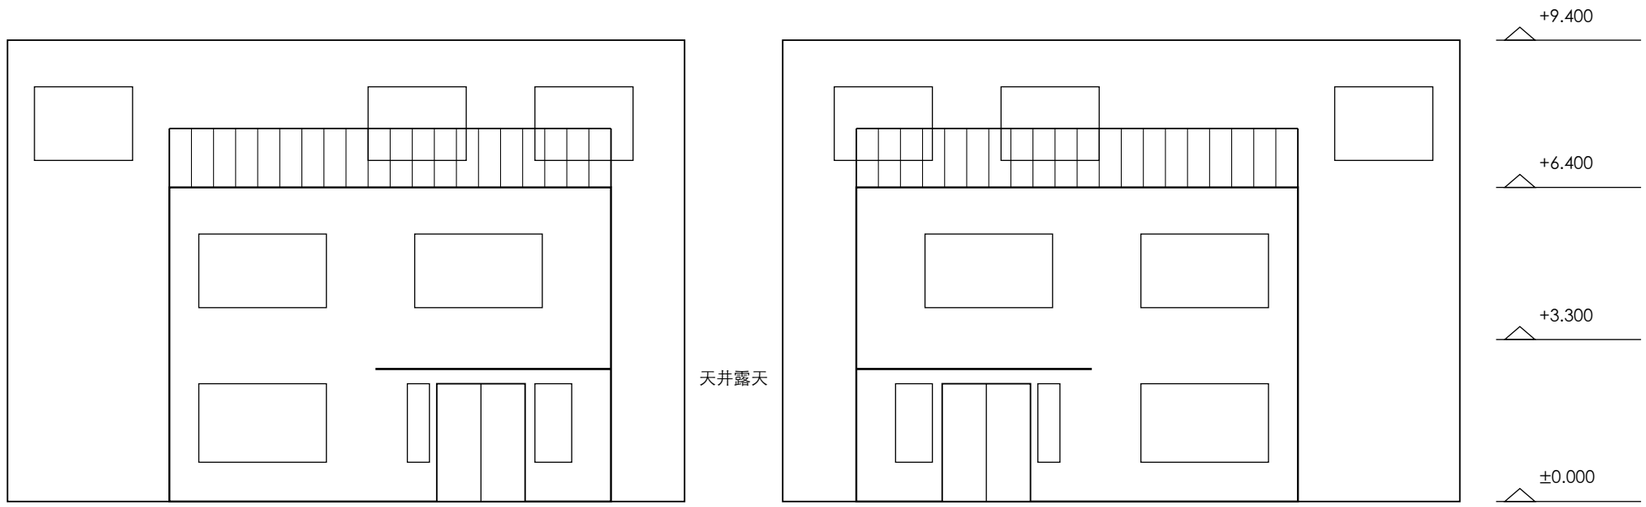


### 立面说明


前部两层、后部三层，前部低屋面用于分户露台。

门窗比例为方案意向，应与最终平面洞口及结构统一。

墙面以简洁涂层为主，墙脚、窗台、雨棚与滴水位置应专门深化。

所有标高均为方案相对标高，绝对标高尚未确定。

### 1-1天井剖面 1:125（剖切位置见建方-02）

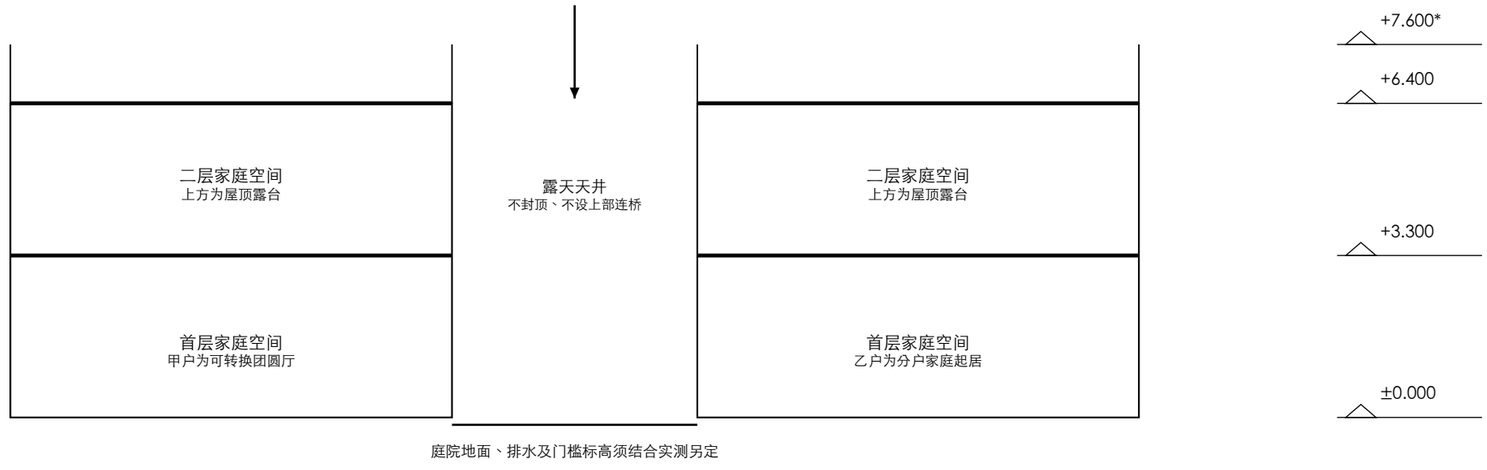


### 剖面深化要点

*围护高度暂按1200示意，不构成合规结论。

楼板厚度、梁底标高与净高均尚未设计，图示楼板线不代表结构构造。

庭院地面暂以室内低150示意，仅用于说明防雨关系。实际应按防涝、排水与长辈平顺通行共同确定。

正式剖面须补充基础、楼梯、屋面、防水、保温、门窗及所有相关节点。

| | | | | |
|---|---|---|---|---|
| 编制阶段：建筑方案深化参考；结构、设备及场地条件尚未核定。<br>尺寸单位：平面与洞口为毫米，标高为米；不得量图替代标注尺寸。<br>本套未含结构及机电施工图；正式设计、审查与签审由具资质单位完成。 | 项目：祁东双户合院 | 图号：建方-06 | 图幅：A3 | 2026.10.26 |
| | 图名：入户立面及天井剖面 | 比例：1:125 | 版本：02 | 签审：待完成 |


# 祁东县双桥镇厚南村双户住宅

## 长辈房、卫浴及楼梯布置

专业方案深化参考版

非施工图，不得据此放线、下料或施工


### 首层长辈房与浴室 1:40（乙户镜像）

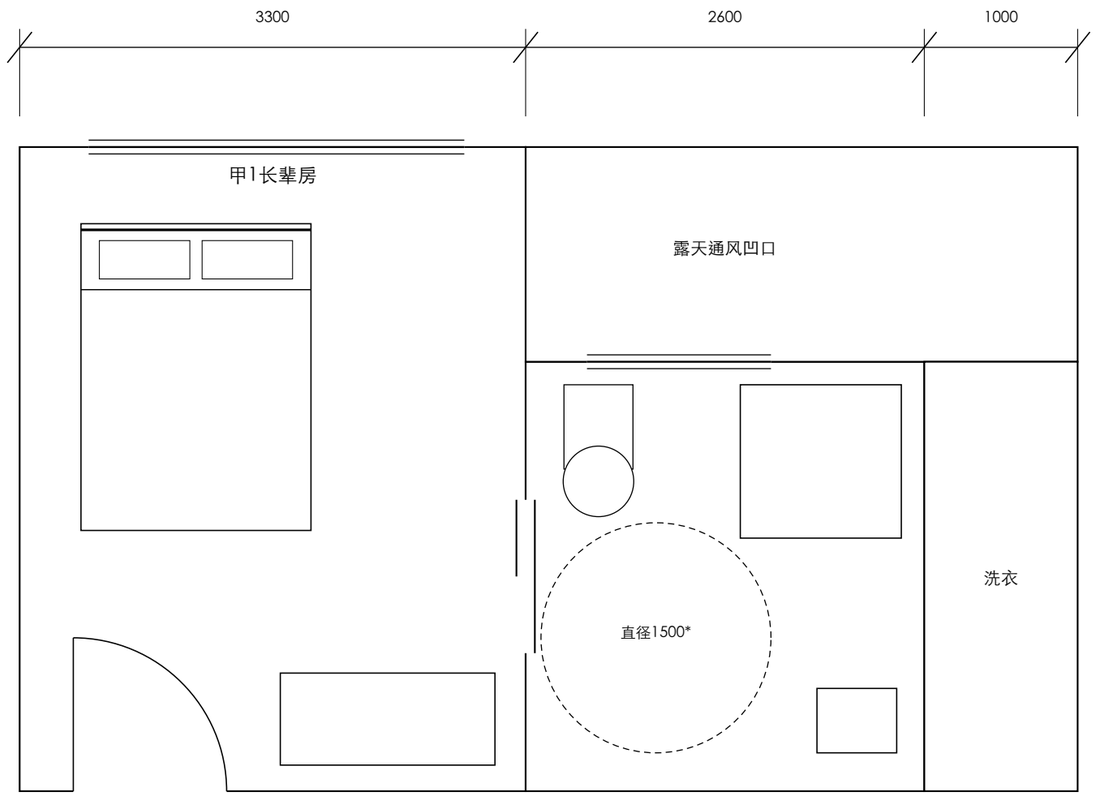


*回转圆为布置目标；净空须扣除完成面并核对实际洁具。

建议保留床侧护理通道、夜灯、扶手基层及平顺门口。淋浴区排水、防滑及干湿关系须与建筑、给排水深化一致。此图不等同于已认证的轮椅无障碍套间。

### 楼梯平面布置意向 1:50

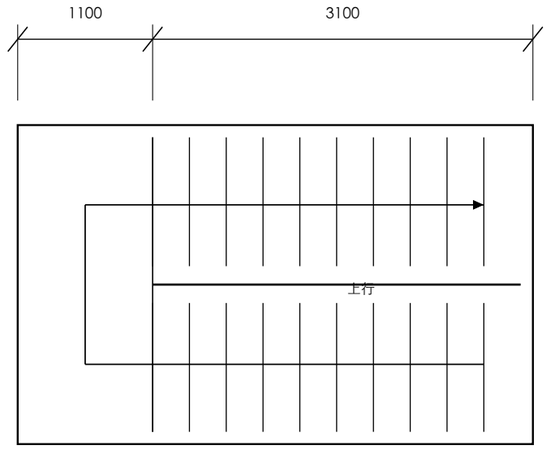


楼梯外包参考4200×2600

**01 首层至二层**

层高暂按3300。可试排20个踢面，每个165；踏面以290为初步布置目标。此为方案计算，不替代楼梯施工详图。

**02 二层至三层**

层高暂按3100，可试排20个踢面，每个155。楼梯仅服务至三层及前部露台，不表示已设计通往高屋面的楼梯。

**03 尺寸与净空复核**

图示楼梯净宽、平台、扶手、梁底及梯段净高须由设计单位结合结构、完成面及适用规范一并校核。

**04 不在本图指定**

未指定钢筋、板厚、混凝土等级、支座锚固或基础构造，施工人员不得自行从图中推定。

| | | | | |
|---|---|---|---|---|
| 编制阶段：建筑方案深化参考；结构、设备及场地条件尚未核定。<br>尺寸单位：平面与洞口为毫米，标高为米；不得量图替代标注尺寸。<br>本套未含结构及机电施工图；正式设计、审查与签审由具资质单位完成。 | 项目：祁东双户合院 | 图号：建方-07 | 图幅：A3 | 2026.10.26 |
| | 图名：长辈房、卫浴及楼梯布置 | 比例：1:40 / 1:50 | 版本：02 | 签审：待完成 |

# 祁东县双桥镇厚南村双户住宅

## 房间统计与主要门窗洞口建议

专业方案深化参考版

非施工图，不得据此放线、下料或施工

### 十四间卧室对应表

| 房间编号 | 楼层 | 数量 | 用途 |
|---|---|---|---|
| 甲1、乙1 | 一层 | 各1间 | 首层长辈房 |
| 甲2至甲5 | 二层 | 4间 | 甲户卧室 |
| 乙2至乙5 | 二层 | 4间 | 乙户卧室 |
| 甲6至甲8 | 三层 | 3间 | 甲户卧室 |
| 乙6 | 三层 | 1间 | 乙户卧室 |
| 合计 | 三层合计 | 14间 | 甲8间、乙6间 |

### 卫生与服务空间

首层：长辈浴室2间、客卫2间，共4处。

二层：每户3处，共6处；三层：每户2处，共4处。

合计14处卫浴，其中12处带淋浴、2处为客卫。

厨房2间，日常餐厅2间；另设可容纳20人的多功能团圆厅。

洗衣房共4间：每户一层约1000×2800，三层约1200×2600；洗衣房不计入卫浴数量。

### 主要平面尺寸与面积属性

后部总宽29600、前部开间总宽23000、总进深16700均为原始示意参考轴线值。

按概念包络估算，室内合计约766平方米；入户雨廊及前阳台约29平方米；露台约113平方米；新增雨棚约2.8平方米。

以上数据不是法定建筑面积、测绘成果或结算工程量，须在正式设计中另行计算。

### 主要门洞类型建议（尺寸：宽×高）

| 编号 | 位置 | 洞口建议 | 备注 |
|---|---|---|---|
| 门01 | 入户门 | 1800×2400 | 形式、门槛待定 |
| 门02 | 卧室及一般内门 | 1000×2100 | 按净宽目标深化 |
| 门03 | 长辈浴室 | 1000×2100 | 推拉意向，净宽复核 |
| 门04 | 楼梯侧卫浴 | 850×2100 | 与洁具通行复核 |
| 门05 | 厨房门 | 1000×2100 | 排烟、燃料待核 |
| 门06 | 团圆厅连接门 | 1400×2400 | 推拉意向 |
| 门07 | 露台门 | 1000×2400 | 门前截水另详 |
| 门08 | 上层后部卫浴 | 800×2100 | 内开，复核洁具避让 |

### 主要窗型建议（实际洞口须统一）

| 编号 | 位置 | 方案宽度 | 高度 / 窗台 |
|---|---|---|---|
| 窗01 | 后部卧室 | 约2400至2700 | 1500 / 900 |
| 窗02 | 首层前厅 | 约3000 | 1800 / 600 |
| 窗03 | 后部浴室 | 首层约1200；上层约800 | 600 / 高窗待定 |
| 窗04 | 厨房 | 约1850 | 1200 / 1200 |
| 窗05 | 二层前卧室 | 约2800 | 1500 / 900 |
| 窗06 | 二层家庭起居 | 约3400 | 1800 / 600 |

本表为方案类型对照，并非门窗生产表。数量、开启扇、纱窗、防护、防火、玻璃、型材、气密水密与节能性能均未定。洞口宽度含“约”的项目必须在正式图中标准化；本表不得用于订货或下料。

编制阶段：建筑方案深化参考；结构、设备及场地条件尚未核定。

尺寸单位：平面与洞口为毫米，标高为米；不得量图替代标注尺寸。

本套未含结构及机电施工图；正式设计、审查与签审由具资质单位完成。

| | | | |
|---|---|---|---|
| 项目：祁东双户合院 | 图号：建方-08 | 图幅：A3 | 2026.10.26 |
| 图名：房间统计与主要门窗洞口建议 | 比例：表格 | 版本：02 | 签审：待完成 |


# 祁东县双桥镇厚南村双户住宅

## 二十人聚餐布置与流线验证

专业方案深化参考版

非施工图，不得据此放线、下料或施工

### 甲户前部：两桌各十人，室内共同用餐

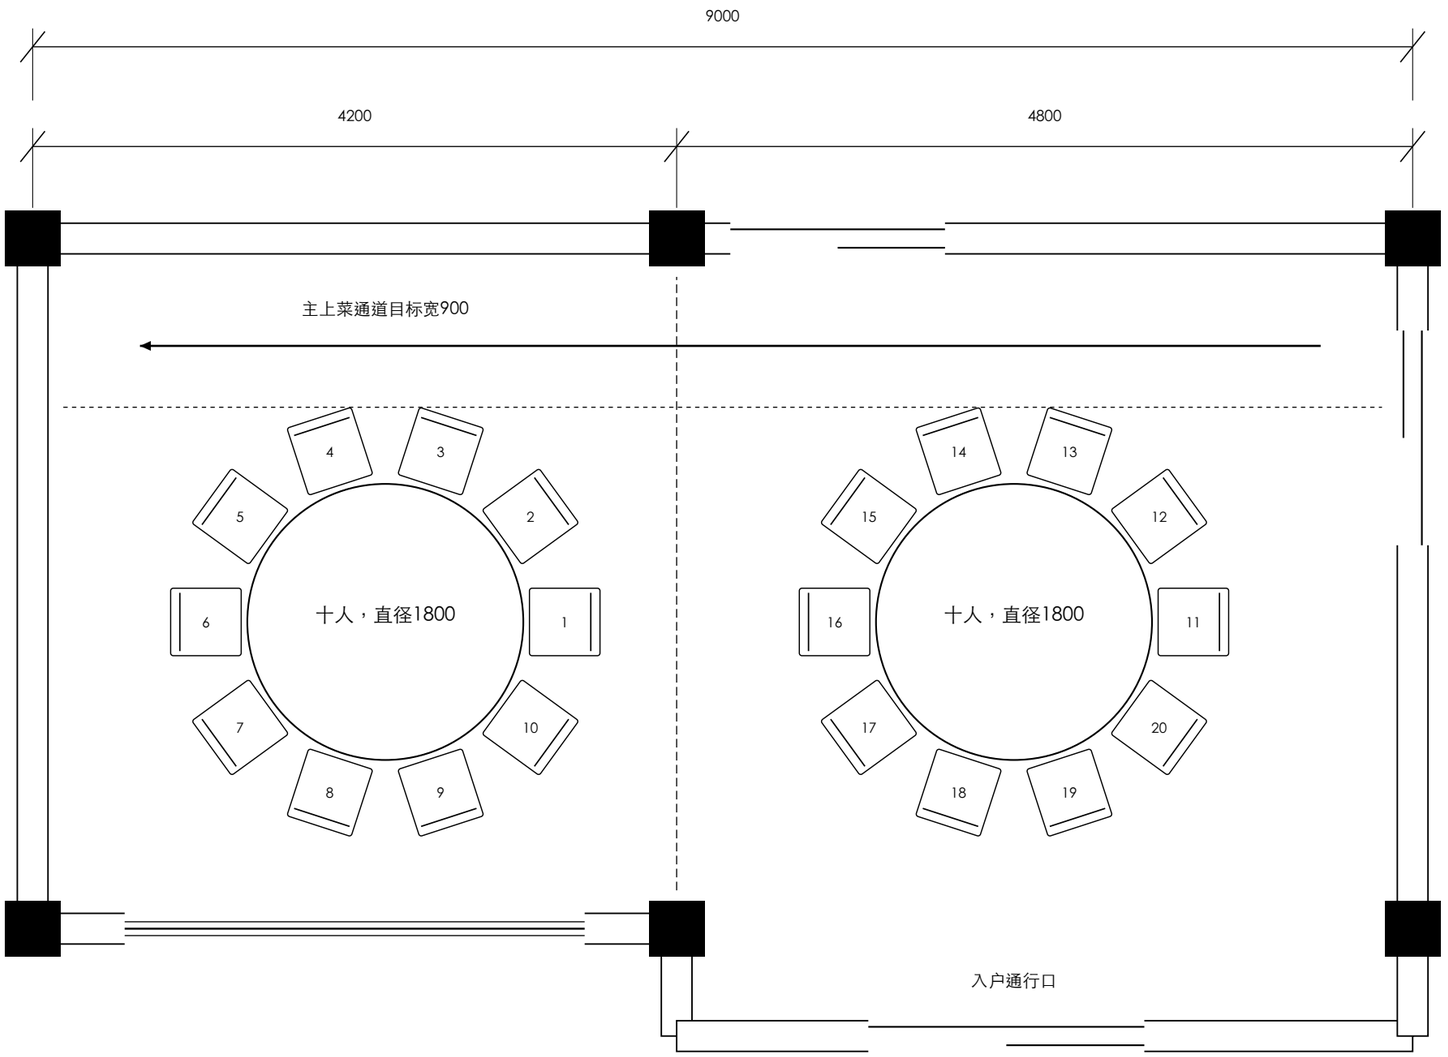


桌椅按紧凑型家庭聚餐布置。北侧作为主要服务路线，南侧仅为次要余量。

**01 二十个明确餐位**

图中20把椅子逐一编号。每张直径1800的餐桌按10人紧凑布置，不代表宽松宴会厅标准。

**02 活动家具**

甲户门厅预留约1000×2100收纳柜，桌椅须按实际尺寸核对。春节将轻型模块沙发移至乙户堂屋侧墙；须验证搬运门洞和临时位置。

**03 两厨协作**

乙厨经后部走廊和局部雨棚进入甲户，甲厨负责主要热菜。前厅后侧门为主要上菜口。

**04 结构协调**

虚线分隔拟打开，原有开间位置仍需合理梁柱传力。不得按本图擅自拆除或取消承重构件。

**05 定案验证**

使用实际桌椅完成二十人的实尺寸排布，核对老人坐席、椅后通行、转身、上菜及出入，再确定墙体开口与家具采购。

**06 室外空间定位**

天井保持露天，露台仅作天气适宜时的辅助活动，不计入春节所需室内餐位。

| | | | | |
|---|---|---|---|---|
| 编制阶段：建筑方案深化参考；结构、设备及场地条件尚未核定。<br>尺寸单位：平面与洞口为毫米，标高为米；不得量图替代标注尺寸。<br>本套未含结构及机电施工图；正式设计、审查与签审由具资质单位完成。 | 项目：祁东双户合院 | 图号：建方-09 | 图幅：A3 | 2026.10.26 |
| | 图名：二十人聚餐布置与流线验证 | 比例：1:40 | 版本：02 | 签审：待完成 |

# 祁东县双桥镇厚南村双户住宅

## 预算控制及施工图深化任务

专业方案深化参考版

非施工图，不得据此放线、下料或施工

### 二百万元总费用控制额度

| 分项 | 控制额度 / 元 |
| --- | --- |
| 主体、基础、楼板及楼梯 | 970000 |
| 门窗、外立面、保温及防水 | 240000 |
| 给排水、电气、热水及通风 | 200000 |
| 基础装修、两厨、十四卫浴及四洗衣间 | 270000 |
| 基本家具家电 | 60000 |
| 庭院、排水及外部接驳 | 50000 |
| 设计测绘及专业协调 | 40000 |
| 预备费 | 170000 |
| 合计 | 2000000 |

以上为待询价的费用上限分配，不是当地报价。保留十四卫浴及四洗衣间后，增加设备与基础装修额度；活动家具及庭院装饰从简，预备费约17万元。约766平方米体量下预算偏紧，须按地勘、工程量及本地报价闭合；不得以削弱结构、防水或排水换取预算。

### 本套可立即提供给专业团队的内容

家庭需求、房间数量、分户归属、功能分区、主要参考尺寸、春节二十人餐位与流线、露台与露天天井的空间关系、门窗类型意向及预算控制范围。

施工人员可据此讨论工序可行性和报价范围，不能据此直接施工或自行补定结构及设备参数。

### 转为可施工图纸必须完成的工作

**01 测绘与规划核定**

批准宅基地范围、基本农田界线、退界、道路关系、地形及邻房标高；确定总平面、绝对标高和建设许可条件。

**02 勘察与结构设计**

地勘、地基承载及基础形式；结构体系、抗震、梁柱墙板、楼梯、雨棚及围护连接。不得由施工队凭经验补齐。

**03 建筑施工图深化**

完成合规核查、墙体与门窗定位、楼梯及净高、构造材料、防水保温、露台围护、节点索引及详图；统一平立剖与各专业。

**04 给排水与热水**

给水来源及压力、同时用水、热水设备、污废水通气、化粪池或市政接驳、雨水计算与排放、检修空间。

**05 电气与通风**

负荷、回路、接地及保护、厨房燃料和排烟、卫浴排风、空调及冷凝水；设备不得随意占用安全通道。

**06 审查、签审与价格闭合**

由具相应资质单位出具完整成果，按属地要求办理审查及手续，形成可追责的签审图纸；按完整范围核对二百万元预算。

**图纸状态说明**

本套为专业方案深化参考，未盖设计单位出图章、注册人员签章或审图章。没有虚构设计单位、资质及责任人。其专业排版不改变当前方案深度。

编制阶段：建筑方案深化参考；结构、设备及场地条件尚未核定。

尺寸单位：平面与洞口为毫米，标高为米；不得量图替代标注尺寸。

本套未含结构及机电施工图；正式设计、审查与签审由具资质单位完成。

| | | | |
| --- | --- | --- | --- |
| 项目：祁东双户合院 | 图号：建方-10 | 图幅：A3 | 2026.10.26 |
| 图名：预算控制及施工图深化任务 | 比例：表格 | 版本：02 | 签审：待完成 |