两栋分开，中间采光，后部连厅

14间卧室 · 14处卫浴 · 2间厨房 · 2间日常餐厅 · 每户二层洗衣间 · 一层梯下储藏




两栋楼各向外移1米，单栋尺寸不变，总宽29.6米，上层恢复2米间距；一层保留2×5.6米后部连接厅，餐厅南侧仍开敞。南端5米花窗墙连接实体外墙，天井围合且露天。原柱位保留，柱身与墙同色；两端各新增南端转角柱，贯通首层至屋顶；取消二层露台8处多余柱段。勒脚连续包过窗下与柱脚，门口断开。

首层层高3.9米，二、三层各3.3米；室内外高差450毫米，前后入口均设三级150毫米台阶。二楼露台及三楼楼板取消范围按标记保留。

天井高窗固定配窄扇；厨房、餐厅及影音室6处北面大窗四折，卫浴上悬、楼梯固定窗保留。封面为网页同一三维网格的离线投影。

一层：走廊围护与天井入口

玄关、客厅、楼梯不设分隔门墙；卫浴、外墙、后门及院墙保留。

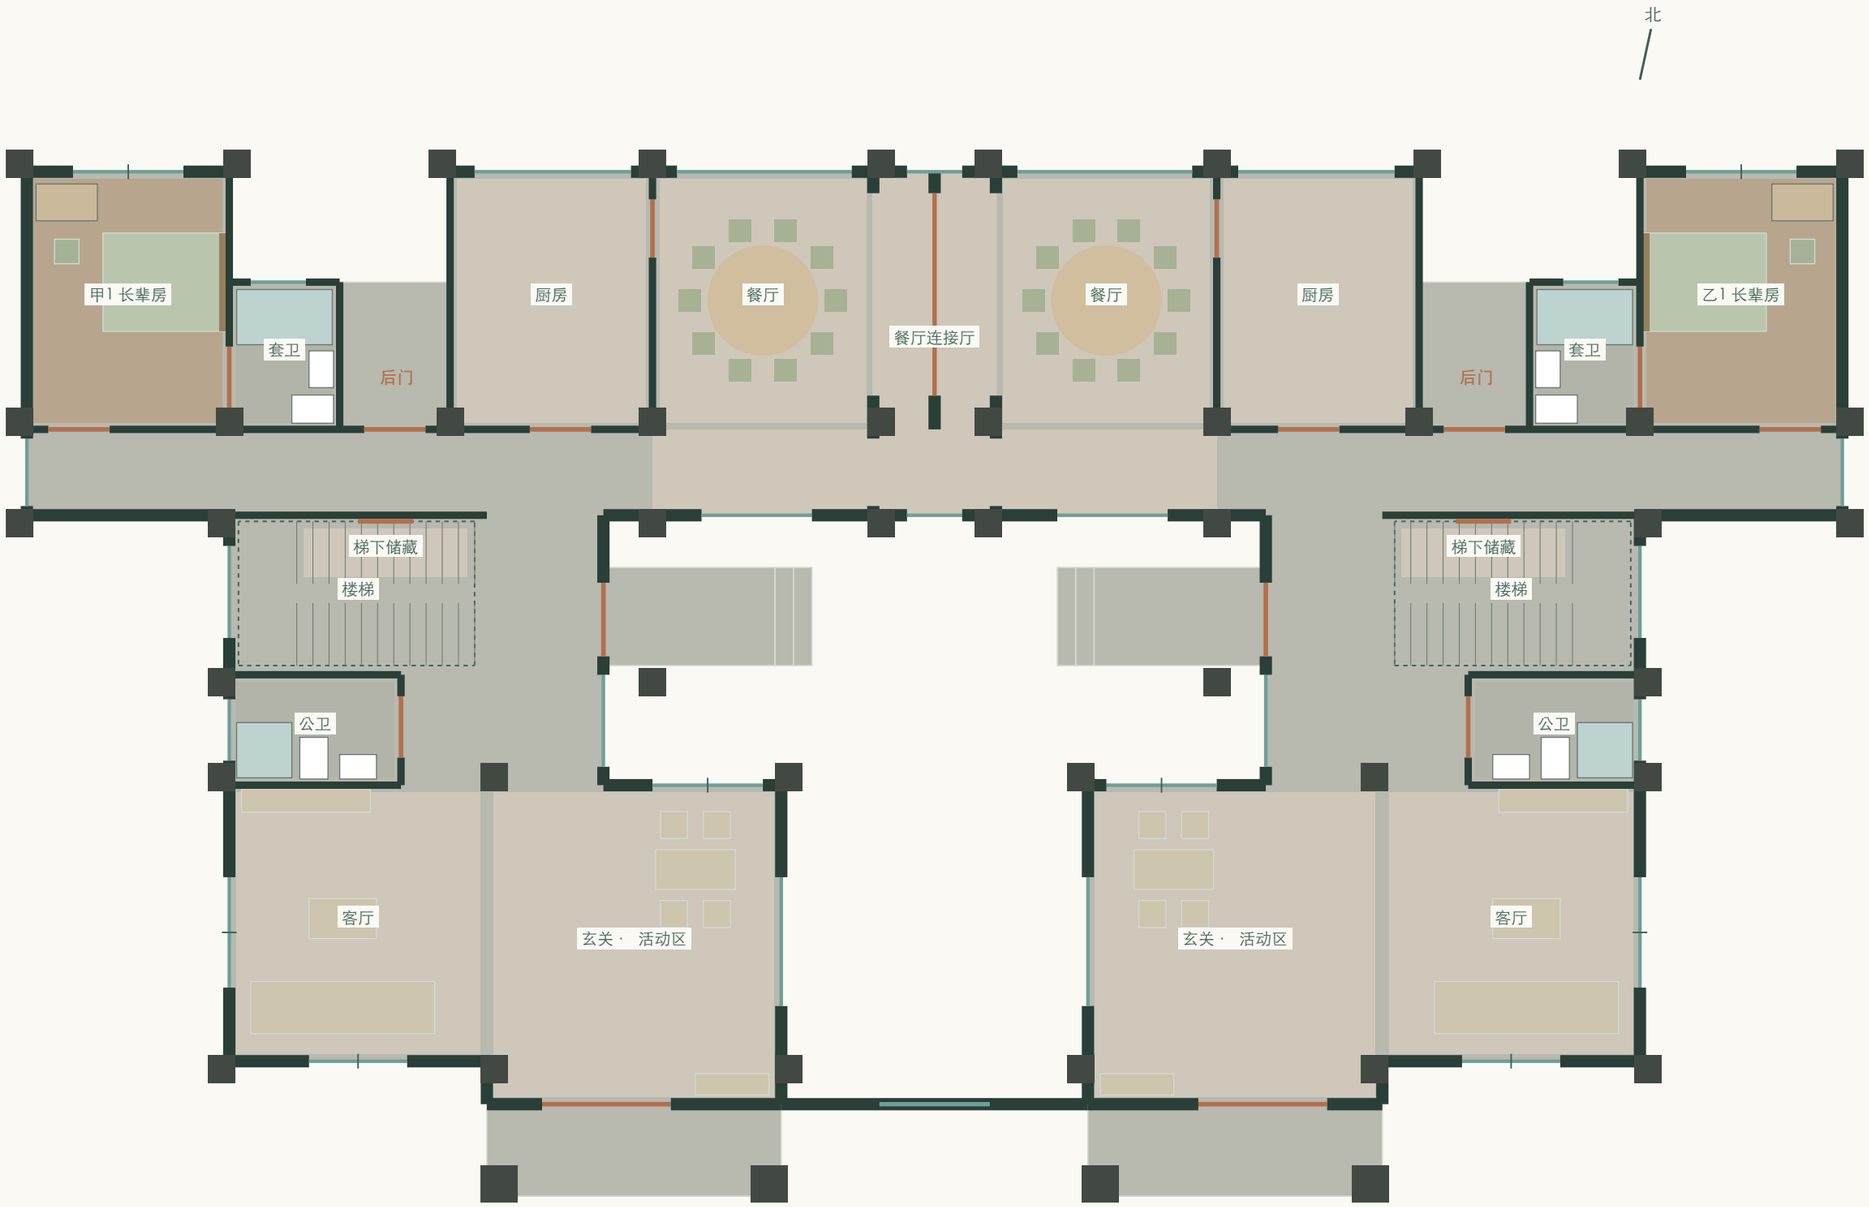

01

长辈房、厨房与四处卫浴保留，卧室不新增朝天井的洞口。

02

每户走廊设1.20米外开玻璃天井门；门外2.80米深平台，再接三级150毫米台阶。

03

天井侧窗同步大固定玻璃配窄扇；中央南向窗1.80×1.85米，窗台1米，大固定玻璃配0.45米窄开启扇。

04

两餐厅经后部连接厅连通，中央设3.30米活动隔断；春节打开可供两桌20人同餐。

05

两端侧墙各三柱，新增南端柱贯通；电视位于卫浴南侧实墙，沙发朝北，楼梯下改储藏，洗衣机移至二层。

墙线：深灰 窗：青绿

门：棕色 栏杆：蓝色

二层：有顶走廊围合，露台保持敞开

四处门位按黑色标记调整；转折通道延伸屋顶补齐，套卫保持独立。



01

8间卧室保留；甲5、乙5旧入口及短隔墙拆除，套卫门墙保留。

02

卫浴旁侧门1.00米进卧室，南端1.10米门进洗衣间，再由0.90米门通露台；北端原露台门墙取消。

03

侧走廊窗同步高窗与窄开启扇；中央南向六窗加高，大固定玻璃配0.45米开启扇。

04

转折通道由低坡内翼补顶，天井侧恢复墙，前露台保留矮基座金属栏杆。

05


前套卫、后排可切换卫浴及其双入口保留；露台不放室内电视。

墙线：深灰 窗：青绿

门：棕色 栏杆：蓝色

三层：恢复走廊外墙，以窗借光

取消楼板与低坡翼顶范围不变，不设通向屋面或空洞的门。

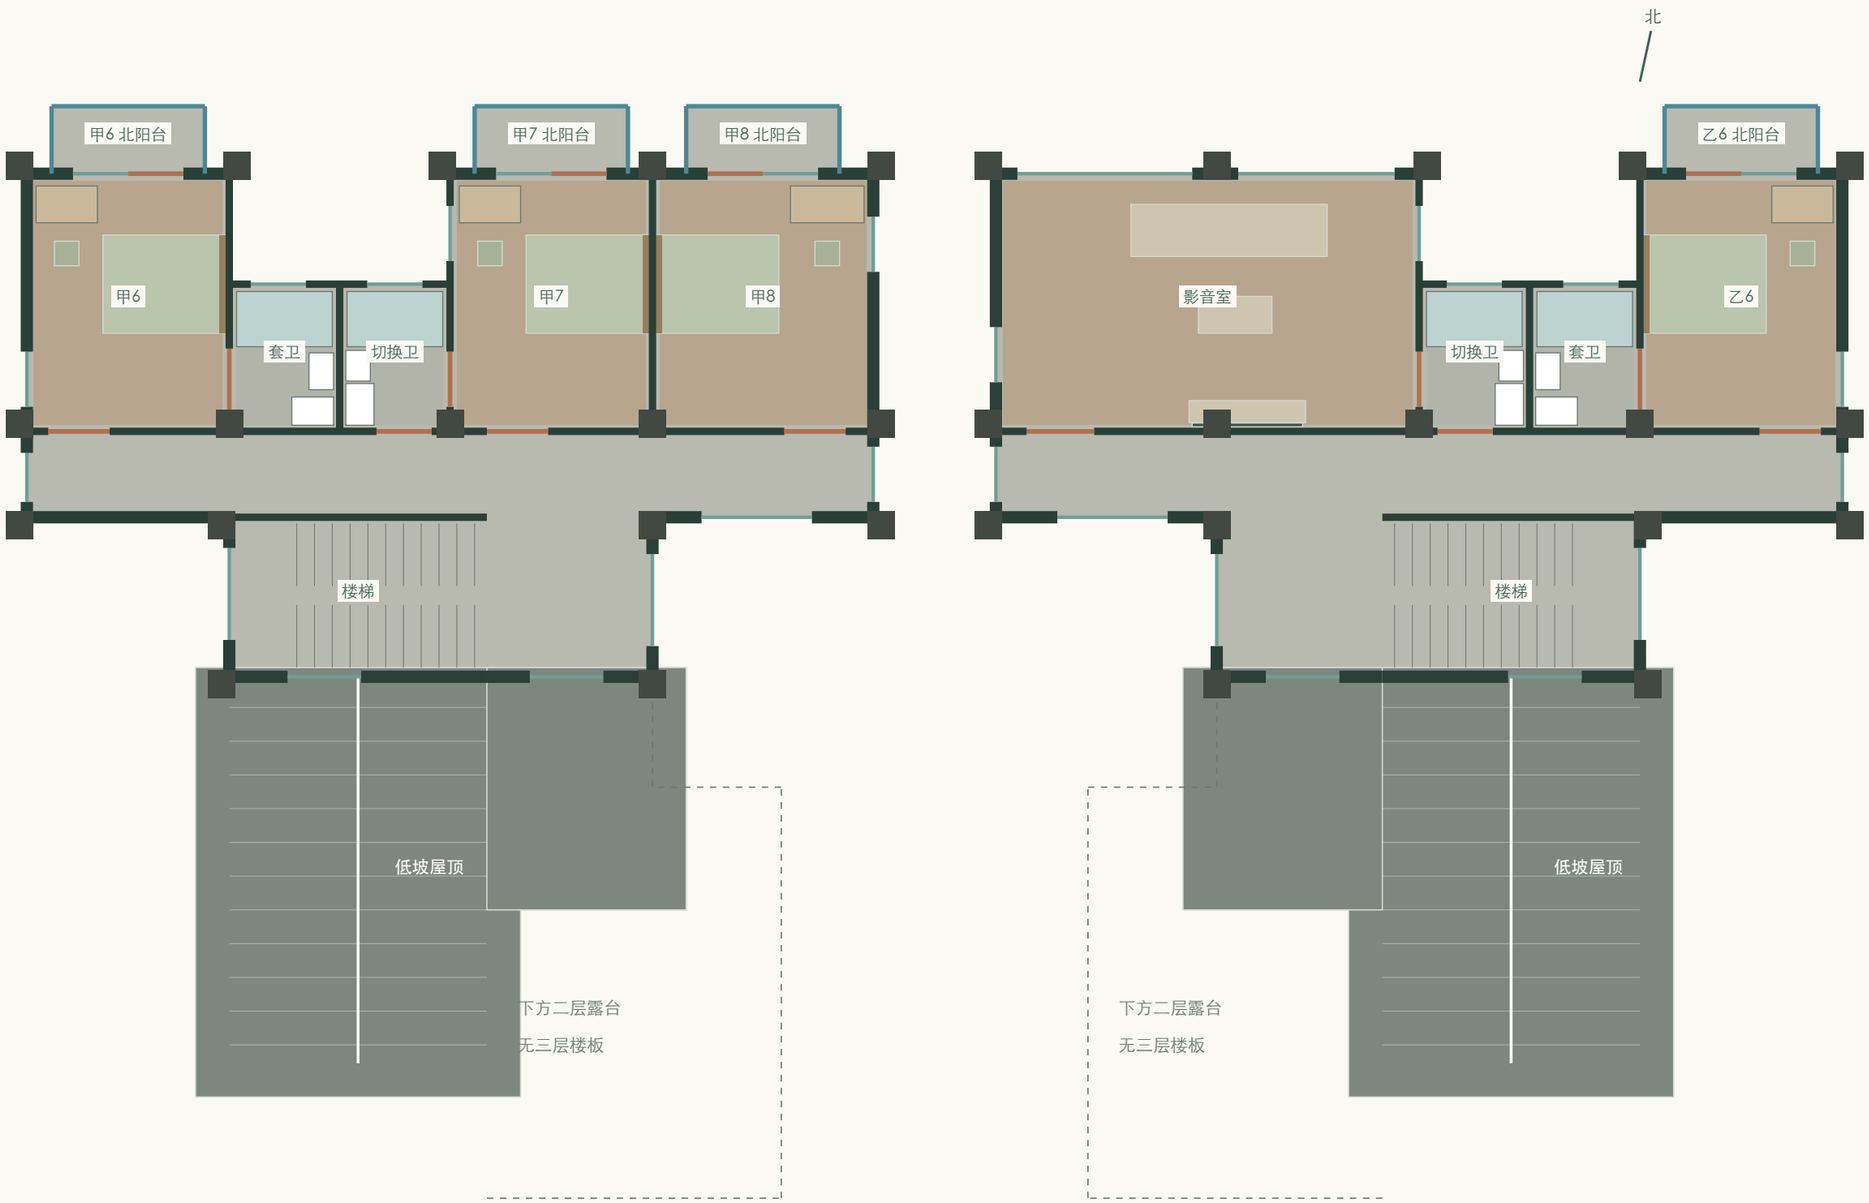

01

甲户3间卧室、乙户1间卧室及影音室保留。

02

侧走廊、后排走廊及南端墙恢复；原临空走廊栏杆取消。

03

侧窗保留，四扇小南窗统一1.20×1.50米；中央六窗仍1.80×1.85米，窗台1米，窗头2.85米。

04

侧窗上下对齐、窗框统一炭灰；中央窗主玻璃固定、窄扇外开，楼梯窗继续固定。

05

主坡顶与到达楼梯保留，洗衣机统一移至二层；二楼连续L形屋面左右8°、纵向南3°。

墙线：深灰 窗：青绿

门：棕色 栏杆：蓝色

天井六窗：主玻璃固定，窄扇通风


原洞宽1.80米，统一加高为1.85米；窗台1.00米、窗头2.85米，把手中心约1.50米。

关闭 / 约75%固定 + 25%开启



分格及开合意向，非门窗加工图

开启 / 仅45厘米窄扇向外开

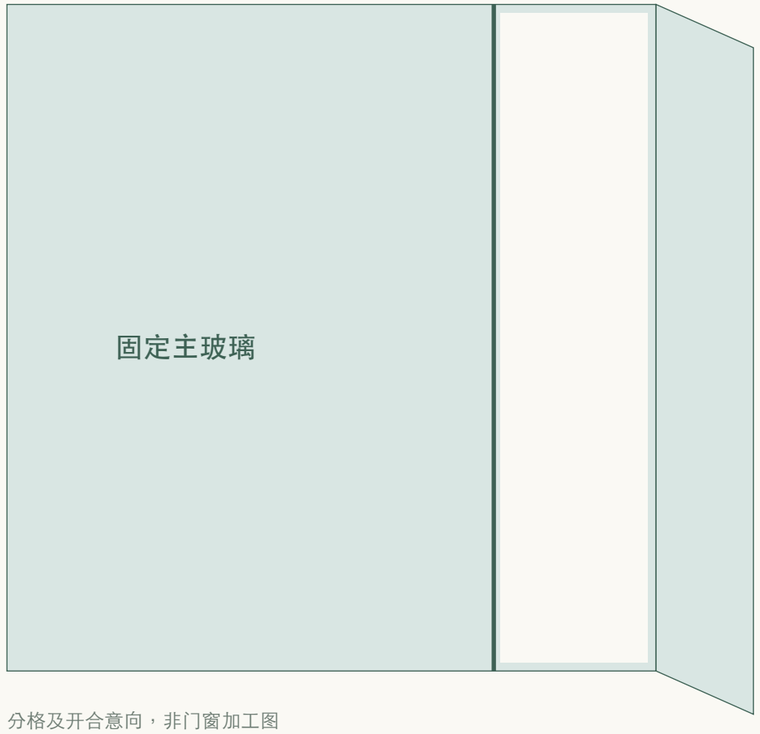

分格及开合意向，非门窗加工图

一至三层后排走廊朝南、朝天井的6扇窗采用同一比例；两户开启扇在外侧边缘镜像布置，形成安静、连续的竖向节奏。固定主玻璃保持不动，网页点击只开启窄扇。


8处天井侧窗和三楼2处走廊南窗也采用固定主玻璃 + 窄扇。其余12处宽窗双扇中分、6处大窗四扇折叠、18处窄窗单扇外开；14处卫浴及2处洗衣间为上悬窗。8处楼梯窗固定，另10处卧室北门保留固定侧窗。

窗头提高后，窗过梁及梁底净高需结构协调；玻璃、五金、纱窗、防雨、限位和实际通风面积须正式设计。不能以模型开度代替产品性能与全屋通风验算。

团圆宴：隔断打开，两桌20席


一层保留连接厅，餐厅合并轴线范围约9.2×4.2米，约38.6平方米。

平日：隔断关闭，各自用餐

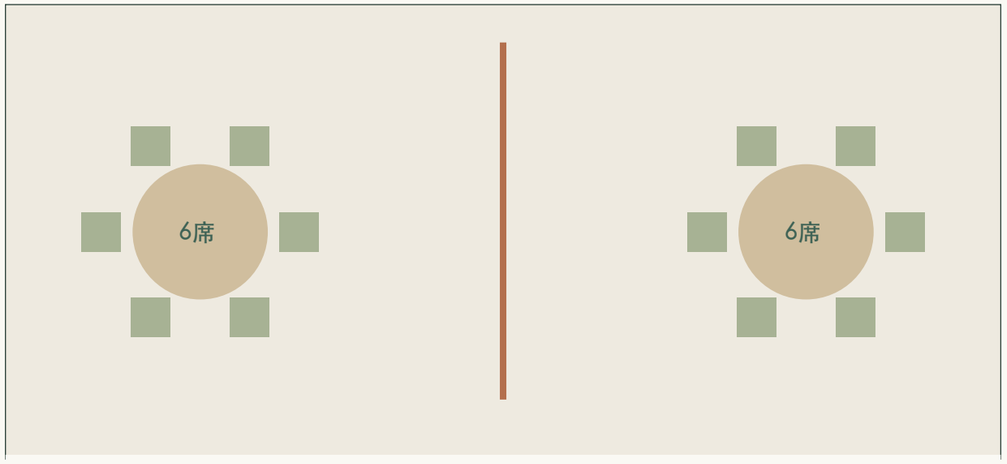

南侧开敞连接长走廊

春节：隔断打开，共20席

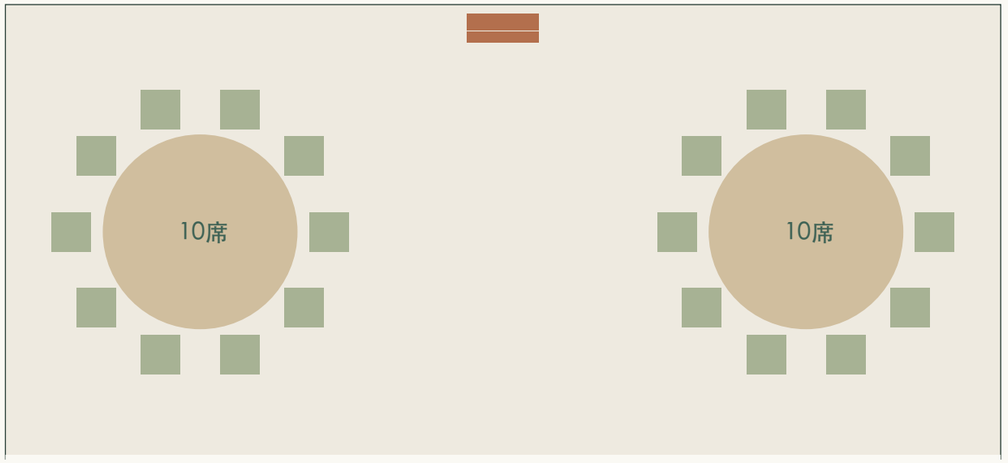

南侧开敞连接长走廊

桌椅为布置意向，保留通向厨房和公共走廊的入口；中间活动隔断不承重。实际家具尺寸与拉椅、端菜通道应现场放样确认。

两户一层楼梯下均封闭储藏，设独立贴墙推拉门；洗衣机移入二层露台入口双门洗衣间，走廊与露台各设一门。14处卫浴均保留淋浴区、坐便器及台盆，二、三层4间可切换卫浴仍采用双入口。

本轮恢复走廊围护及取消楼板均为尚未开工阶段的方案调整。连接厅与两栋的连接、露台边梁、栏杆锚固与坡顶荷载须由当地设计人员统一设计，不能据模型直接施工。

预算与落实：先核结构，再按同一清单报价

总预算约200万元，涵盖建筑、内装、机电与院落；本轮不承诺当地成交价。

几何范围已经明确

单栋13.8米开间与室内房间尺寸不变，两户恢复旧版2米间距，总宽29.6米；一层保留连接厅，三层前部露台楼板仍取消。

材料保持克制

暖白耐候墙面、烟陶红低坡屋顶、暖灰薄基座与哑光暖灰铜细竖杆；减少石材、装饰线脚和复杂定制。中央6窗为固定主玻璃配窄扇，其余窗保留；前部小屋顶左右分坡、纵向向南降低。

结构需重新组织

没有既定结构图。两栋各自柱位保留；连接厅及两侧节点、基础、抗震与沉降策略须正式计算。

防水与雨天使用

有顶走廊恢复带窗围护，二层前段和露台仍露天；天井门外平台、台阶、露台、檐沟及二层洗衣间分别协调防水、排水与检修。露台栏杆须完成支承与锚固设计。

拿去报价的内容

先核现场边界、朝向、高程和审批条件，再形成结构、门窗表、栏杆、屋顶及防水节点和工程量；按同口径向当地单位询价。

烟陶红 · 推荐

暖石板灰

深炭灰

灰橄榄

砂岩褐

地面选材：温暖、耐用、便于维护

四组瓷质砖控制材料种类；室内外采用协调色调，按不同湿水环境选择具体表面。



客厅 / 餐厅 / 玄关 / 厨房

暖米灰细石纹瓷质砖 / 800×800毫米

暖米灰、细石纹、细腻哑光。客餐厅尽量连续铺贴，厨房选厂商明确适用的易清洁表面。



卧室 / 影音室

浅橡木色木纹瓷质砖 / 200×1200毫米

低饱和浅橡木色，顺直或不超过三分之一错缝；不做人字拼，避免偏橙、强木结。



天井 / 露台 / 开敞走廊

暖浅灰室外石纹瓷质砖 / 600×600毫米

暖浅灰、细防滑石纹；按室外湿区适用性选样，兼顾泥水清洁与排水。楼梯从同色系列裁制踏步。



卫浴 / 淋浴区

暖灰卫浴防滑瓷质砖 / 300×300毫米

暖灰细防滑砖，配近色灰缝；适用于赤脚湿区，便于围绕地漏找坡。

砖缝采用近色灰，宽度按具体砖厂说明和实际尺寸偏差确定，拒绝零缝铺贴。先做样板，比较湿水、茶渍或油污清洁后的实际表现。木纹是瓷砖的视觉效果，仍保留硬质脚感。

控制费用：主砖集中采购同批次与同色号；卧室才使用木纹，避免拼花和超大板；报价包括找平、防水、粘结、勾缝、收边、运输、损耗与人工，不只比单片砖价。

材料性能与维护参考： 瓷质砖与低吸水性 室外瓷砖与易清洁表面 湿区适用分类 留缝与铺贴说明

门色：入口有重点，室内轻而安静

两户采用同一套色彩；门框与门扇尽量协调，五金统一哑黑。以下为色彩意向，须现场饰面样板确认。




入户门

烟熏胡桃色




卧室及普通室内门

浅灰橡木色

 

卫浴门

暖灰米色

 

北侧后门

深暖灰



天井 / 露台门框

炭灰细框

入户门用压低橙黄的中深烟熏胡桃色，作为外观的温暖重点；室内门用更轻的浅灰橡木色，衔接卧室地面。卫浴用暖灰米色，后门用深暖灰，玻璃门框与窗框统一炭灰。


外部门按户外耐候饰面选样，室内、卫浴按各自环境选门体；色彩相近不表示门体材料必须相同。板材、包边、锁具、耐湿、开启与必要的消防要求须按最终产品和正式设计核对。

色彩比手机或打印图更可靠的判断方式，是把门样、地砖、墙面、栏杆及屋顶色板放在现场同一光线下比较。

大窗四折：平日采光，需要时折叠打开

厨房、餐厅与影音室共6处北向大窗；洞口宽度、窗台及窗头保留。

关闭 / 四扇分格

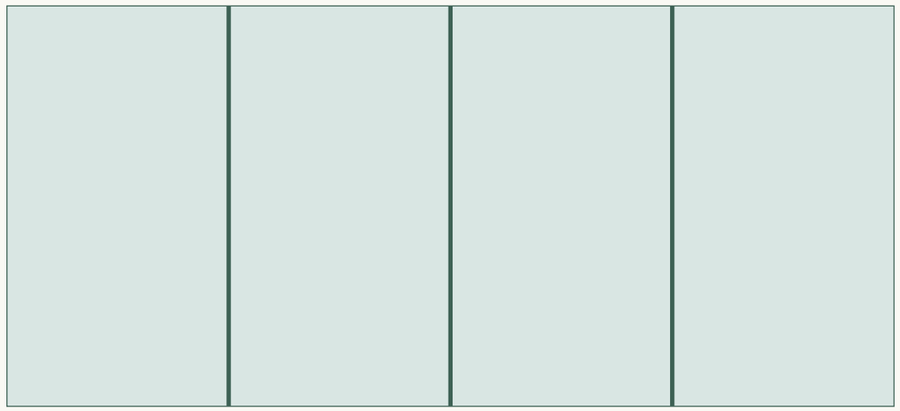

示意 / 正立面

打开 / 左右各两扇向外折叠



示意 / 平面折叠，不按比例

每侧两扇组成折叠对，模型展示向外折约85°，中间不留固定玻璃。点击大窗可打开，再点关闭。厨房与餐厅每户各1处；乙户三层影音室2处，共6处。

安装前核对玻璃重量、折叠五金、轨道与清洁维护方式；开启时的室外窗扇空间、纱窗、排水与气密水密性能按实际产品深化。普通窗不改成折叠窗，控制定制范围。

北侧：只给卧室小阳台

二层6处，三层4处，共10处；影音室保持原窗。




每处约2.50×1.10米，新增阳台投影共约27.5平方米。原北窗保留900毫米固定侧窗，另900毫米玻璃门向房内开启，门位避开书桌，床位不变。

栏杆统一哑光暖灰铜与暖灰薄基座。模型仅表达空间及外观；阳台悬挑、边梁、锚固、防水、排水、门槛及总造价须正式核定，未据此完成承载或合规验算。

二层洗衣、一层梯下储藏


两户镜像设置；走廊—洗衣间—露台双门连通，梯下单扇推拉门。

二层洗衣间 / 1:30

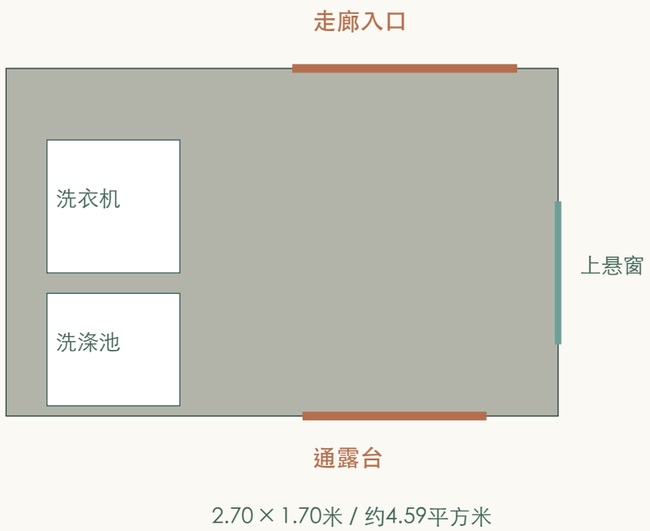

2.70 × 1.70米 / 约4.59平方米

一层梯下储藏 / 1:40

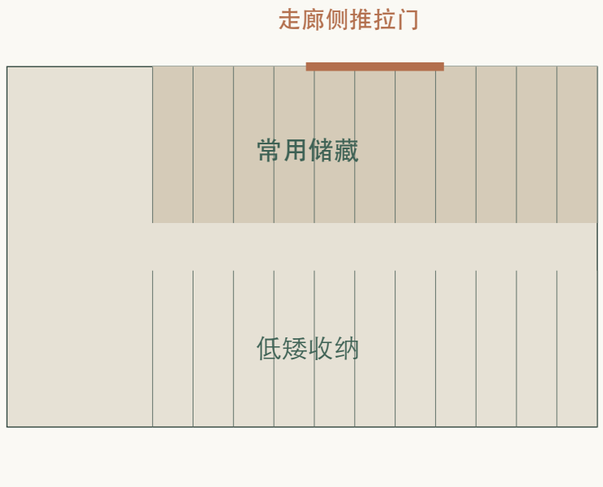

轮廓为楼梯投影，不能全计为可站立面积。

顶面随梯板收口，门参考宽0.90米、高2.05米。

洗衣间：占用每户二层露台北侧一角；现有走廊门保留，新增南侧露台门。洗衣机与洗涤池靠同侧布置，门扇避开设备；东侧上悬窗通风，地面暖灰湿区砖。轻质墙、屋面、设备荷载、防水和排水须联合设计。

梯下储藏：一层两户均封闭，低矮处放收纳箱，高净空区由公共走廊进入。单扇贴墙推拉门减少对通道及柜内空间的占用；通风、防潮、照明和成品净空另行深化。

北侧卧室新增10处小阳台，统一尺寸与轻质栏杆；新增工程纳入原200万元总预算复核，结构及造价以正式设计和当地报价为准。