
专业协调01：分栋连厅与一层平面

两户各向外移1.00米；单栋不缩放。上层相对墙轴线x=13.80及15.80米，恢复2米间距。

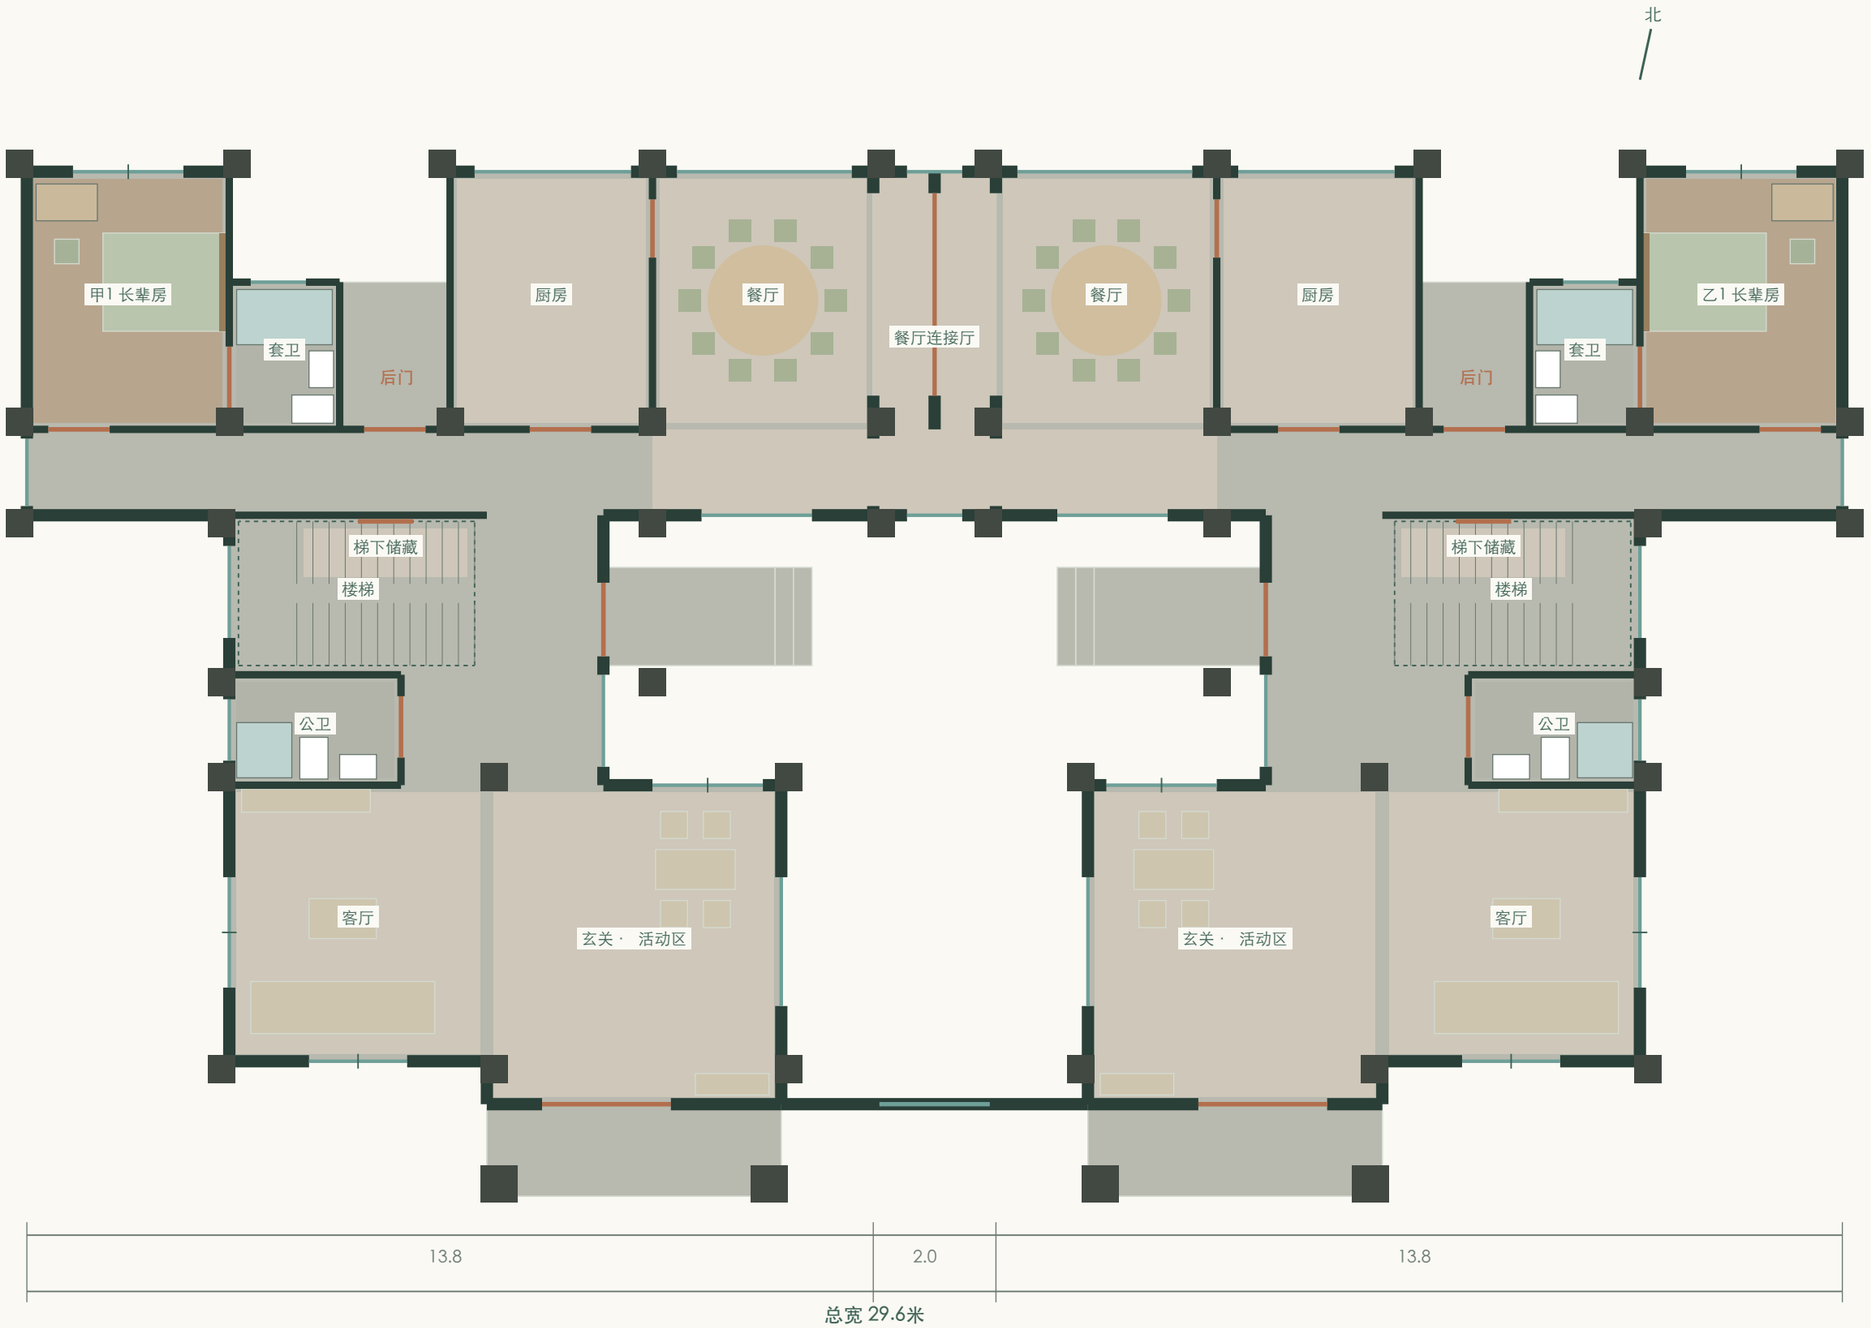

几何变更

层高3.90/3.30/3.30米；室外−0.45米，三级150毫米台阶。

总宽29.60米，单栋开间13.80米，中间2.00米。

一层保留2.00×5.60米连接厅及20席餐厅；二、三层中间不设楼板，相对端墙各补走廊高窗及错位房间侧窗。屋檐内侧外挑600毫米，中央余约800毫米开缝。

餐厅隔断参考洞长3.30米，梁柱与门头承载另定。

一层三角标记新增2处1.00米门洞；X侧门改窗；北侧通道北墙按标记取消，设后门及三级台阶。


天井门洞1.20米，门外平台2.80×1.60米，门扇全开后模型余深超过1.50米；实际净尺寸按门窗深化复核。非施工图，未定配筋与基础。

专业协调02：二、三层临空边缘与屋面

蓝线为保留的露台栏杆；深灰为恢复的走廊墙，青绿为新窗；室内楼板范围保留，北侧增卧室小阳台；内侧主屋顶补600毫米挑檐。



二层：有顶走廊加墙，转折通道补顶，前露台敞开

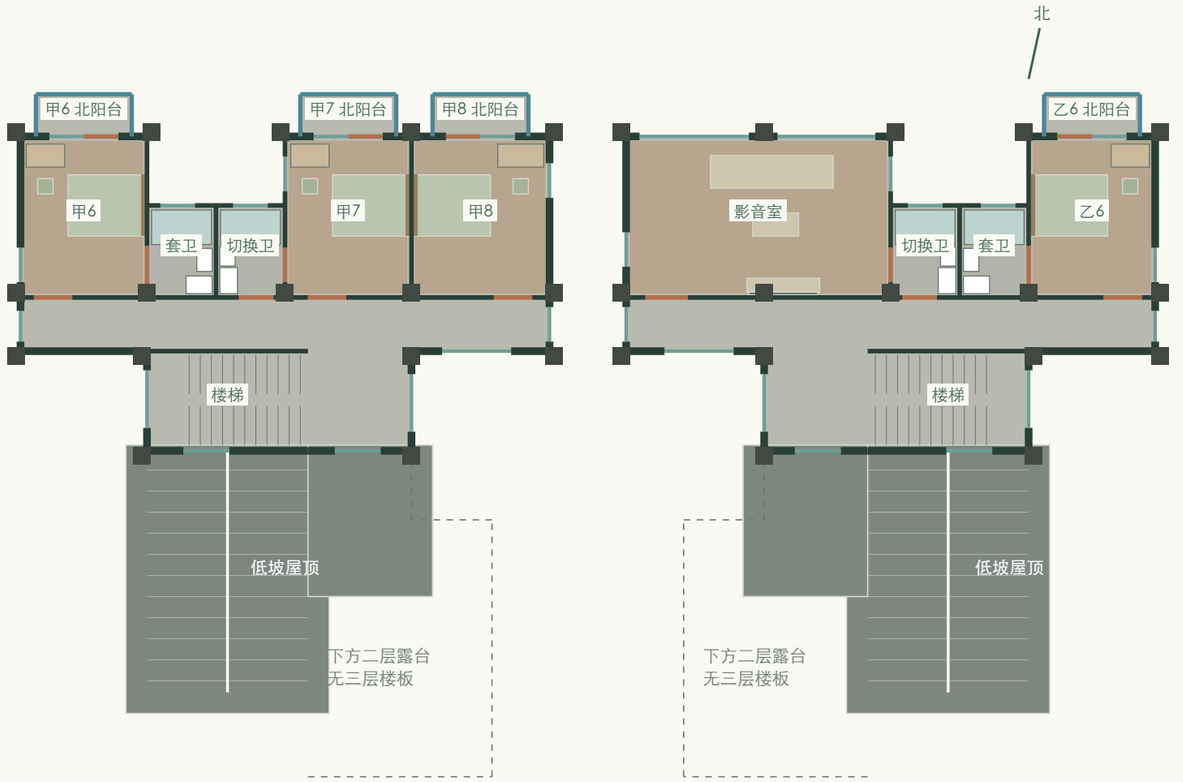

三层：走廊墙与窗恢复，低坡翼顶延伸，前露台保持露天

前部露台原8段栏杆保留，北侧卧室阳台各三面围护：0.35米暖灰轻质基座，上部哑光暖灰铜细竖杆与扶手，高度暂按1.20米建模；应复核实际完成面高度、竖杆间距、扶手、基座与边梁锚固。

后排主屋顶前坡约18°，楼梯并入连续坡面，二层卧室上方小顶左右约8°分坡，屋脊及侧檐向南约3°降低；三层前部原露台楼板全部取消，不将坡屋面作为可走露台。

相对内墙新增4扇走廊高窗及4扇错位房间侧窗，连接厅前后补2窗。上层2米为墙轴线几何间距；实际净距、采光通风、防火及维护条件须正式核定。

专业协调03：门窗统计与结构待办

仅完成方案几何筛查。未确定结构体系、地勘、构件截面及配筋，不能放行施工。

本轮门窗与功能核对

卧室 / 卫浴	14间 / 14处（42件洁具）
厨房 / 日常餐厅	2间 / 2间，合厅20席
洗衣 / 储藏	每户二层露台入口洗衣间；一层梯下封闭储藏
竖向标高	层高3.90/3.30/3.30米；室外−0.45米，三级150毫米台阶
窗总数	92处：12双扇、6四折、22固定配窄扇、18单扇、16上悬、18固定（含8楼梯窗及10侧窗）
门总数	59处：53处平开、6处贴墙推拉（4卫浴、2储藏）
中间新窗	4扇走廊高窗、4扇错位侧窗、2扇连接厅窗
几何筛查	按平移后的原柱状符号复核，无洞口投影重叠；41处近柱提示

正式结构设计应落实

1. 原图保留柱位随两栋向外复位；二层露台8处多余柱段仍取消。两栋各自柱网及连接厅节点、基础与沉降策略须正式设计，不能将模型视为已定柱网。
2. 恢复围护的新增恒荷载、窗过梁、墙梁柱连接和下部支承；一层墙线与上层不重合，不能直接认定传力可行。
3. 餐厅3.30米开口上方的上部荷载传递；活动隔断本身不承重。
4. 主坡顶、低坡顶、檩条、屋架、檐沟及抗风连接。
5. 双扇外开窗的尺寸、五金、限位、玻璃和纱窗，以及室外通行净空。
6. 地基基础、重力、抗侧与抗震计算及签审图。

坐标表按分栋复位后的实际坐标输出：两户恢复原坐标，单栋尺度不变；中间墙轴线x=13.80和15.80米。门窗高度、洞口、栏杆与坡度均为方案意向；门窗表不能用于直接加工或施工。

下载逐洞口坐标及开启意向表（CSV）

专业协调04：地面材料与采购接口

色彩和规格为选材方向；具体产品须核实用途、吸水率、湿面适用与耐污维护资料。



客厅 / 餐厅 / 玄关 / 厨房

800×800毫米 / 暖米灰细石纹瓷质砖

暖米灰、细石纹、细腻哑光。客餐厅尽量连续铺贴，厨房选厂商明确适用的易清洁表面。



卧室 / 影音室

200×1200毫米 / 浅橡木色木纹瓷质砖

低饱和浅橡木色，顺直或不超过三分之一错缝；不做人字拼，避免偏橙、强木结。



天井 / 露台 / 开敞走廊

600×600毫米 / 暖浅灰室外石纹瓷质砖

暖浅灰、细防滑石纹；按室外湿区适用性选样，兼顾泥水清洁与排水。楼梯从同色系列裁制踏步。



卫浴 / 淋浴区

300×300毫米 / 暖灰卫浴防滑瓷质砖

暖灰细防滑砖，配近色灰缝；适用于赤脚湿区，便于围绕地漏找坡。

长条木纹砖错缝和砖缝按厂家及实物平整度确定；本图不承诺任一厂家产品已通过项目选材。开敞走廊与天井采用室外湿区适用面，淋浴区另核赤脚湿态性能。不能把单一摩擦系数或哑光外观当作所有场地的安全证明。

地坪完成面、地漏与找坡、防水、接缝及门槛一并协调；普通同色勾缝须耐污且适应使用环境，室外不得把所有缝刚性填死。瓷质砖日常用适配的中性清洁剂与清水维护；按厂家方法清除残留并避免长期积油、皂膜或泥水。

参考：TCNA湿区用途分类、Marazzi室外瓷砖与安装维护说明；均不替代中国项目正式设计及实际产品报告。

专业协调05：门饰面颜色表

位置与洞口详见门窗协调CSV；以下颜色用于协调，不作涂层、门芯或防火等级承诺。



入户门 / 2处

烟熏胡桃色 / #806A55



卧室及普通室内门 / 19处

浅灰橡木色 / #B2A087



卫浴门 / 18处

暖灰米色 / #B9B6AA



北侧后门 / 4处

深暖灰 / #666C63



天井 / 露台门框 / 16处

炭灰细框 / #414944

入户和后门按户外使用环境核对耐候、防腐与五金；卫浴按耐湿、清洁和门锁条件核对。门体材料、面层与安全性能分别确认，不能以效果图木色认定门芯或结构。

同一颜色在木纹膜、烤漆、金属和玻璃框上会产生不同光泽和观感，应以同一现场光线下的实样批准。

专业协调06：天井侧恢复墙与门窗布置

原有16处新增窗保留；玄关内部两门取消，二层门位保持；原门窗保留范围、二楼新门位、中央六窗及小屋顶见本轮说明；均为方案意向。

每户新增窗：宽 × 高 / 窗台高（米）

一层玄关北窗	1.80 × 1.45 / 1.00
一层侧走廊	1.50 × 1.85 / 1.00
一层中央南向窗	1.80 × 1.85 / 1.00
二层侧走廊	1.50 × 1.85 / 1.00
二层中央南向窗	1.80 × 1.85 / 1.00
三层侧走廊	1.50 × 1.85 / 1.00
三层中央南向窗	1.80 × 1.85 / 1.00
三层南端	1.20 × 1.50 / 1.35

每行甲、乙户各1处。中央6窗及8处天井侧窗窗头2.85米，固定主玻璃配窄开启扇；三楼小南窗的窄扇宽0.30米，其他天井窗0.45米。把手中心约1.50米。新洞口未与原柱状符号投影相交；该筛查不等于结构承载或抗震验算。

空间与实施核对

一层：玄关通楼梯门与内部隔墙取消，外侧北窗保留，避开转角窗开启范围，窗下不增柜体以保留活动桌拉椅空间。天井门洞1.20米，门外平台2.80×1.60米，后接三级150毫米高差；模型中门扇完全外开后仍有超过1.50米余深。两侧台阶之间约留2.00米通行。

二层：北端y=8.50米原露台门墙取消；卫浴旁x=7.50米设1.00米卧室侧门，南端y=6.70米设1.10米露台门。甲5、乙5旧入口及短隔墙拆除，卫浴门墙保留。转折通道已补低坡内翼屋顶，天井侧为墙，前露台仍用栏杆。

三层：有顶走廊南墙改窗，不设通向取消楼板处的门。

围护暂按200毫米外观建模，宜优先比选轻质墙；新增墙体荷载、边梁、连接、过梁与基础须结构设计确认。窗下及洞边实体段不能据本图认作已设计的构造柱。

统一炭灰窗框；外侧窗台排水、上口滴水、安全玻璃、限位、纱窗和实际净空须门窗深化。原低窗防护及全屋采光通风仍须整体核查，本页不作全屋合规结论。

协调依据：GB 55038-2025 第4.2.1条（公共走廊及开启窗）、第4.1.16条（临空外窗防护）、第4.2.7条（出入口与平台）。适用范围及项目落实由当地正式设计核定。

查看主管部门发布的规范摘录

专业协调07：复坡小屋顶与中央六窗

屋顶坡度及门窗尺寸仅为方案几何，未确定结构截面、玻璃及五金。



小屋顶：每片以局部x=5.40米起脊，左右各8°分坡；沿y方向另设约3°南向坡。前、后檐形成山墙轮廓，左右侧檐沟向南端汇水。后缘最高约1.03米，低于新南窗窗台1.35米；柱顶按同一坡面下延40毫米，避免穿出屋面。

低坡内翼：小屋顶右坡与内翼合成同坡面连续L形屋面，覆盖两户转折通道与新增洗衣间；不增加三层楼板，前露台及中央天井仍露天。取消内部檐沟与重叠补片，外围檐沟、泛水和滴水须深化。

中央六窗：原1.80米洞宽不动，窗台1.00米、窗头2.85米；主玻璃固定，0.45米侧扇外平开。不能把模型分格视为玻璃厚度或五金承载已定。

侧檐沟、落水、泛水、双锁边金属板与实际复坡排水路径须联合深化；型材、屋架、抗风与梁柱荷载须正式验算。各家屋面系统对坡度及密封有专门要求，按最终产品选型。

屋面构造参考：RHEINZINK Standing Seam Technology（非项目选材或中国标准替代）

专业协调08：四折大窗与本轮空间核对

平面模型协调，非五金加工图或结构计算。

四折窗清单 / 原洞口不变

甲户 / 1层 / 厨房	2.55 × 1.60米；窗台0.85米
甲户 / 1层 / 餐厅	2.85 × 1.60米；窗台0.85米
乙户 / 1层 / 厨房	2.55 × 1.60米；窗台0.85米
乙户 / 1层 / 餐厅	2.85 × 1.60米；窗台0.85米
乙户 / 3层 / 影音室	2.55 × 1.60米；窗台0.85米
乙户 / 3层 / 影音室	2.85 × 1.60米；窗台0.85米

四折窗在模型全开状态下，中间视线未被玻璃阻挡；左右堆叠仍占用端部空间，不能按整个洞口面积作为实际通风或消防有效开口。门窗表与本页须随选定厂家复核，不作直接订货依据。

本轮分栋与屋面协调

一层：玄关、客厅和楼梯之间的分隔门墙取消；公卫围墙、外墙及原柱保留，两端各补南端柱并贯通至屋顶。上部荷载不能依赖已删除的隔墙，须复核梁柱承载和传力。电视位于公卫南侧实墙，沙发朝北，通向楼梯的家具通道已核对。

二层：相邻双坡小顶向内侧延伸，转折通道有顶；边梁、轻屋面与泛水需正式设计。模型对二层房间和通道的980个采样点作竖向屋面射线检查，前露台保持露天。

侧窗：8处朝天井的侧窗改固定主玻璃配0.45米窄扇；甲7侧窗改为0.90×1.60米，与甲3一致。

折叠窗：四扇2＋2外折，端部窗扇约0.64至0.71米宽；重量、五金、轨道、耐候、限位、纱窗及洞边支承由产品及正式设计确定。模型动作不代替加工或结构性能核验。

专业协调09：三楼南窗、连续屋面与补柱

本页为方案位置与几何核对，新增柱及连接需正式结构设计。

四扇南向小窗 / 同一立面语言

每扇外框约1.20×1.50米；窗台1.35米、窗头2.85米，与中央高窗对齐。主玻璃约0.90米，窄分格约0.30米，两户镜像布置。

两扇楼梯窗保持固定，两块玻璃均不动且不设把手。两扇走廊窗仅窄扇向外开启；新窗不作为上人屋面出入口。

连续屋面后缘最高约1.03米，新窗下方留约0.32米模型间隙；实际窗台、泛水、完成面及安装公差须复核。

连续L形屋面 / 外围排水

主翼右坡与通道内翼共面，沿接边高度及法向一致。屋面没有原补片之间的坡度折线或内檐沟；锁边纹理连续，统一薄檐。

左右坡约8°，纵向向南约3°；排水沿L形外围组织。前露台和中央天井保持露天。屋面接墙泛水、檐沟容量、防结露、保温及抗风仍须正式设计。

两端侧墙每层各三柱。新柱位于南端转角，与原前排柱线对齐；新增柱参考原柱状符号外形，非已设计的截面或配筋。

柱位及上下衔接

原图128处柱段记录保留，取消的8处二层柱段及6处已无楼板的矮柱段不显示；新增两端南柱每户每层1段，共6段。模型共显示120段柱，新增柱脚落至室外铺地下50毫米；72处上层柱段逐一核对与下层衔接，顶层接主屋顶下皮。

新增柱不意味着基础和荷载路径已完成设计。结构人员应统一核定柱网、地基基础、梁柱连接、抗震与沉降策略，并把新增柱计入门窗洞口协调。

专业协调10：v4挑檐与餐厅界面

主檐600毫米，低檐550毫米；默认烟陶红；内侧600毫米挑檐分开收边，顶部约800毫米开缝。

主屋面外露边挑出约600毫米；二楼L形低屋面外露边挑出约550毫米。扩大外露檐口，保持原坡面和屋脊高度，采用约60毫米视觉薄檐、深阴影线及外围排水；接上层墙处采用泛水，不将屋面穿入室内。

v4恢复上层2米间距，一层保留2×5.6米连接厅。两户餐厅南侧3.60米轴线范围内的墙和门取消，连通长走廊；西、东端柱及连接厅中部活动隔断保留。地面连续铺暖米灰室内砖；厨房界面、外侧玻璃围护保留。


挑檐悬挑、檩条、抗风连接、檐沟容量、滴水及屋面层厚度须联合设计。模型中的檐口和柱位只用于方案协调。餐厅墙移除时，上部荷载应由正式设计的梁柱体系承担，不能将移墙后的模型当作承载已获确认。

中间4扇走廊窗0.90×1.85米，固定主玻璃配300毫米外开窄扇；4扇房间侧窗0.90×1.60米，沿用旧版错位及半透玻璃，整扇外开。连接厅前后各补1窗。南端墙长5.00米、高2.20米，保留1.80米装饰花窗。屋檐落地黑色管线从外观模型移除，实际排水系统仍须正式设计。

二层洗衣、一层梯下储藏


两户镜像设置；走廊—洗衣间—露台双门连通，梯下单扇推拉门。

二层洗衣间 / 1:30

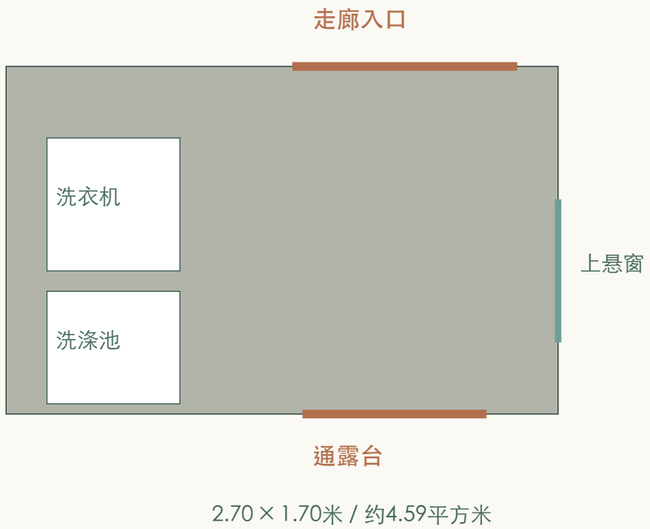

2.70 × 1.70米 / 约4.59平方米

一层梯下储藏 / 1:40

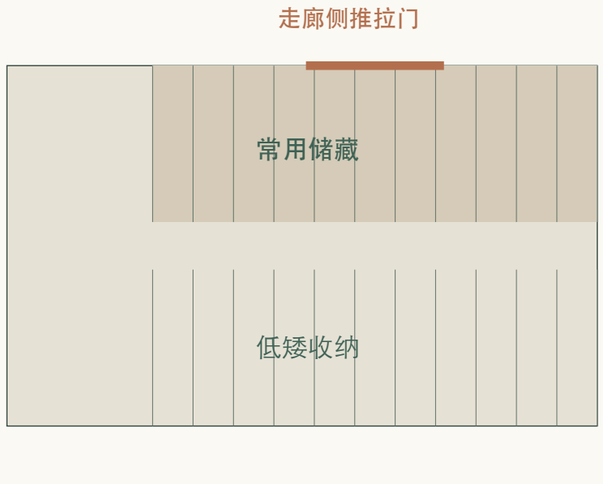

轮廓为楼梯投影，不能全计为可站立面积。

顶面随梯板收口，门参考宽0.90米、高2.05米。

洗衣间：占用每户二层露台北侧一角；现有走廊门保留，新增南侧露台门。洗衣机与洗涤池靠同侧布置，门扇避开设备；东侧上悬窗通风，地面暖灰湿区砖。轻质墙、屋面、设备荷载、防水和排水须联合设计。

梯下储藏：一层两户均封闭，低矮处放收纳箱，高净空区由公共走廊进入。单扇贴墙推拉门减少对通道及柜内空间的占用；通风、防潮、照明和成品净空另行深化。

北侧卧室新增10处小阳台，统一尺寸与轻质栏杆；新增工程纳入原200万元总预算复核，结构及造价以正式设计和当地报价为准。

北侧：只给卧室小阳台

二层6处，三层4处，共10处；影音室保持原窗。



每处约2.50×1.10米，新增阳台投影共约27.5平方米。原北窗保留900毫米固定侧窗，另900毫米玻璃门向房内开启，门位避开书桌，床位不变。

栏杆统一哑光暖灰铜与暖灰薄基座。模型仅表达空间及外观；阳台悬挑、边梁、锚固、防水、排水、门槛及总造价须正式核定，未据此完成承载或合规验算。