
双户合院· 家人沟通版

祁东双户合院概念方案 | 保留十四间卧室，照顾长辈，容纳二十人团圆饭

平日各自安居，春节共享团圆。

两户围绕露天天井独立生活。首层可转换团圆厅承担共同聚餐；卧室、日常厨房和独立楼梯满足全年的生活需要。

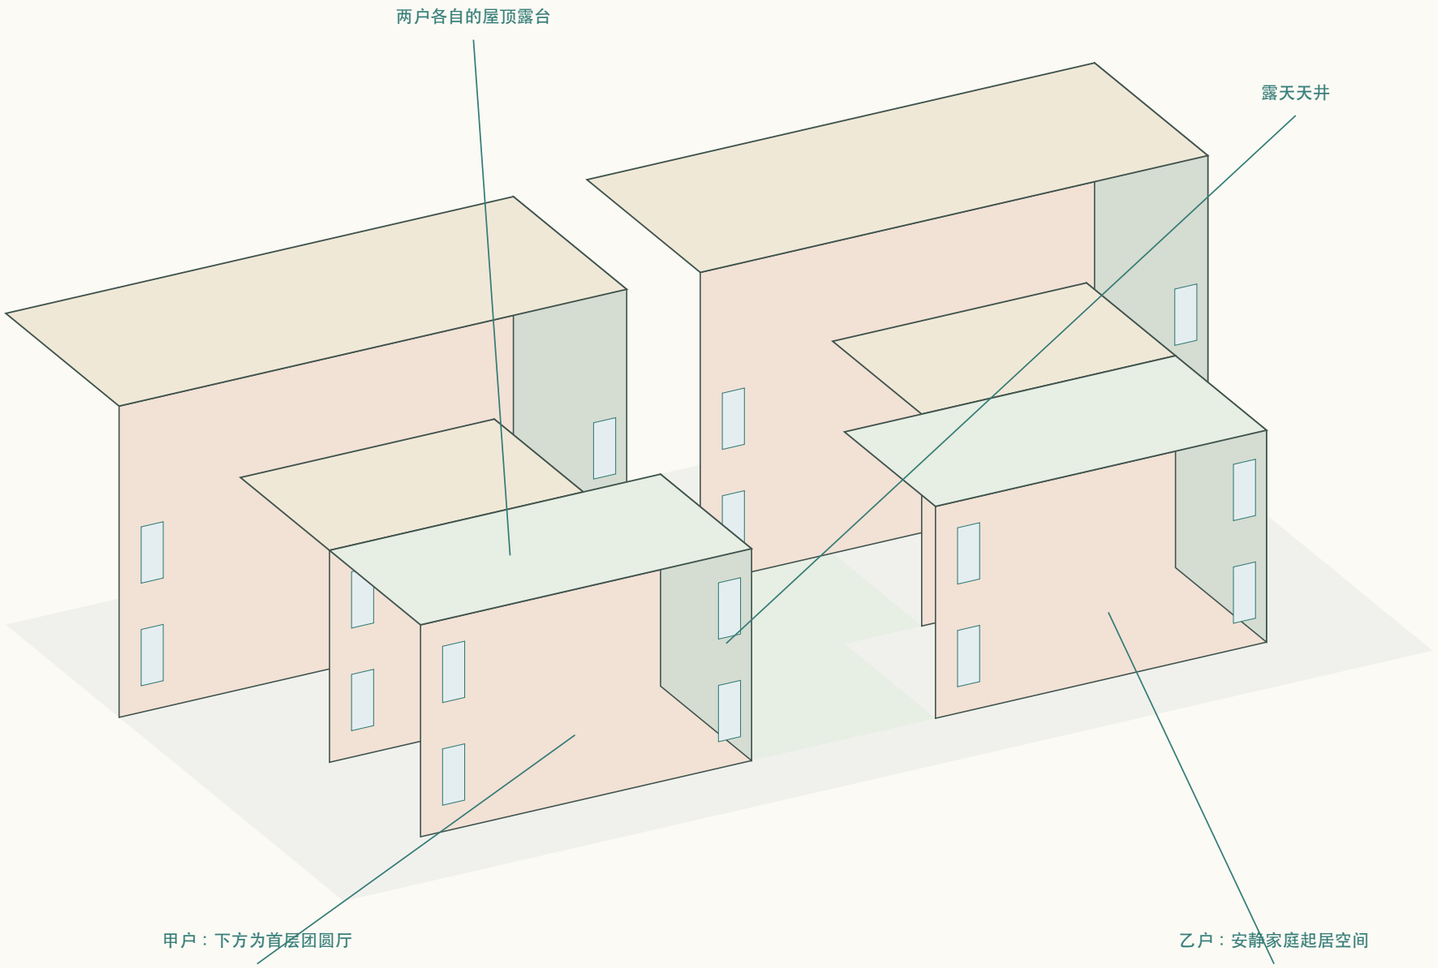

14

保留卧室总数

2

首层长辈房，两户各一间

20

室内共同用餐人数

200

万元人民币，总预算上限

固定要求

甲户8间卧室，乙户6间卧室。

每户首层保留长辈房，厨房和楼梯独立。

中央天井保持露天。

露台用于晾晒及适宜天气下的休闲。

图册导读

图01 一层平面 / 图02 二层平面 / 图03 三层及屋顶露台

图04 二十人团圆饭 / 图05 长辈生活与日常转换 / 图06 立面、剖面与防雨策略

一层平面

一层平面 | 两户独立生活 + 首层长辈房 + 可转换团圆厅



1 两户首层均设长辈房

甲1、乙1保留在首层，分别配置加大的独立浴室。日常就餐与卫浴均在同层，不依赖楼梯。

2 室内二十人团圆厅

甲户前部客厅与堂屋整合为可转换的家庭空间。保留主要开间的结构协调位置，宽敞连通口须由结构设计人员深化。

3 两套独立日常厨房

后部餐厅服务平日用餐。春节可由甲户承担主要热菜烹饪，乙户协助备菜、清洗及收餐。

4 连接两厨的避雨流线

在后部两条走廊之间建议设置跨度约2米的轻型雨棚，仅连接首层。约2.8平方米的新增遮盖须核对规划许可。

5 安排实际储物位置

设置洗衣柜、厨房食品储藏柜及聚餐桌椅收纳柜。后部通风采光凹口保持露天。

尺寸为开间或轴线参考值，并非实测净尺寸。墙体及天井边界按原方案包络作概念调整。

*北向依据原一层图指北针估读，须以实测核定。

二层平面

二层平面 | 保留两户各四间卧室 + 独立家庭起居



1 二层保留八间卧室

甲2至甲5、乙2至乙5，保持原方案每户四间卧室的数量。

2 卫浴数量不减少

本层每户后部两间共用卫浴，另有楼梯侧一间，共六间。两间后部卫浴各约1.8×2.8米，由走廊进入。

3 保留分户安静起居

前部家庭起居室用于分户休息、阅读和学习，不作为新增卧室计算。

4 服务区集中布置

新增卫浴利用原后部服务区，不占卧室；上下层给排水集中深化。洗衣房设在一层和三层。

5 两户保持独立交通

两户使用各自的楼梯，二层不增设跨越天井的连桥。

尺寸为开间或轴线参考值，并非实测净尺寸。墙体及天井边界按原方案包络作概念调整。

*北向依据原一层图指北针估读，须以实测核定。

三层及屋顶露台

三层平面 | 左三间 / 右一间卧室 + 露台，天井保持露天



1 保留原三层卧室数量

甲6至甲8共三间，乙6一间；三层合计四间，与原始图纸一致。

2 共用卫浴与洗衣房

每户保留两间共用卫浴，均由后走廊进入；门厅外墙侧设独立洗衣房，靠近露台晾晒。

3 影音室作为辅助活动室

乙户保留影音及多用途活动室；首层仍设置看电视的位置，长辈不必上三层参加主要团聚活动。

4 前部低层屋顶设置露台

两户各有露台，可晾晒、休闲。春节冬季团圆饭所需餐位全部安排在室内，不依赖露台。

5 先解决排水与防水

深化时须落实门前截水、主排水、应急溢流及安全围护。图示排水方向仅为意向，须另行设计。


尺寸为开间或轴线参考值，并非实测净尺寸。墙体及天井边界按原方案包络作概念调整。

*北向依据原一层图指北针估读，须以实测核定。

春节：二十人室内共同用餐

春节使用验证 | 两桌各十人，室内共同用餐；天井与露台不计入必需餐位


甲户前厅：紧凑型家庭团圆饭布置

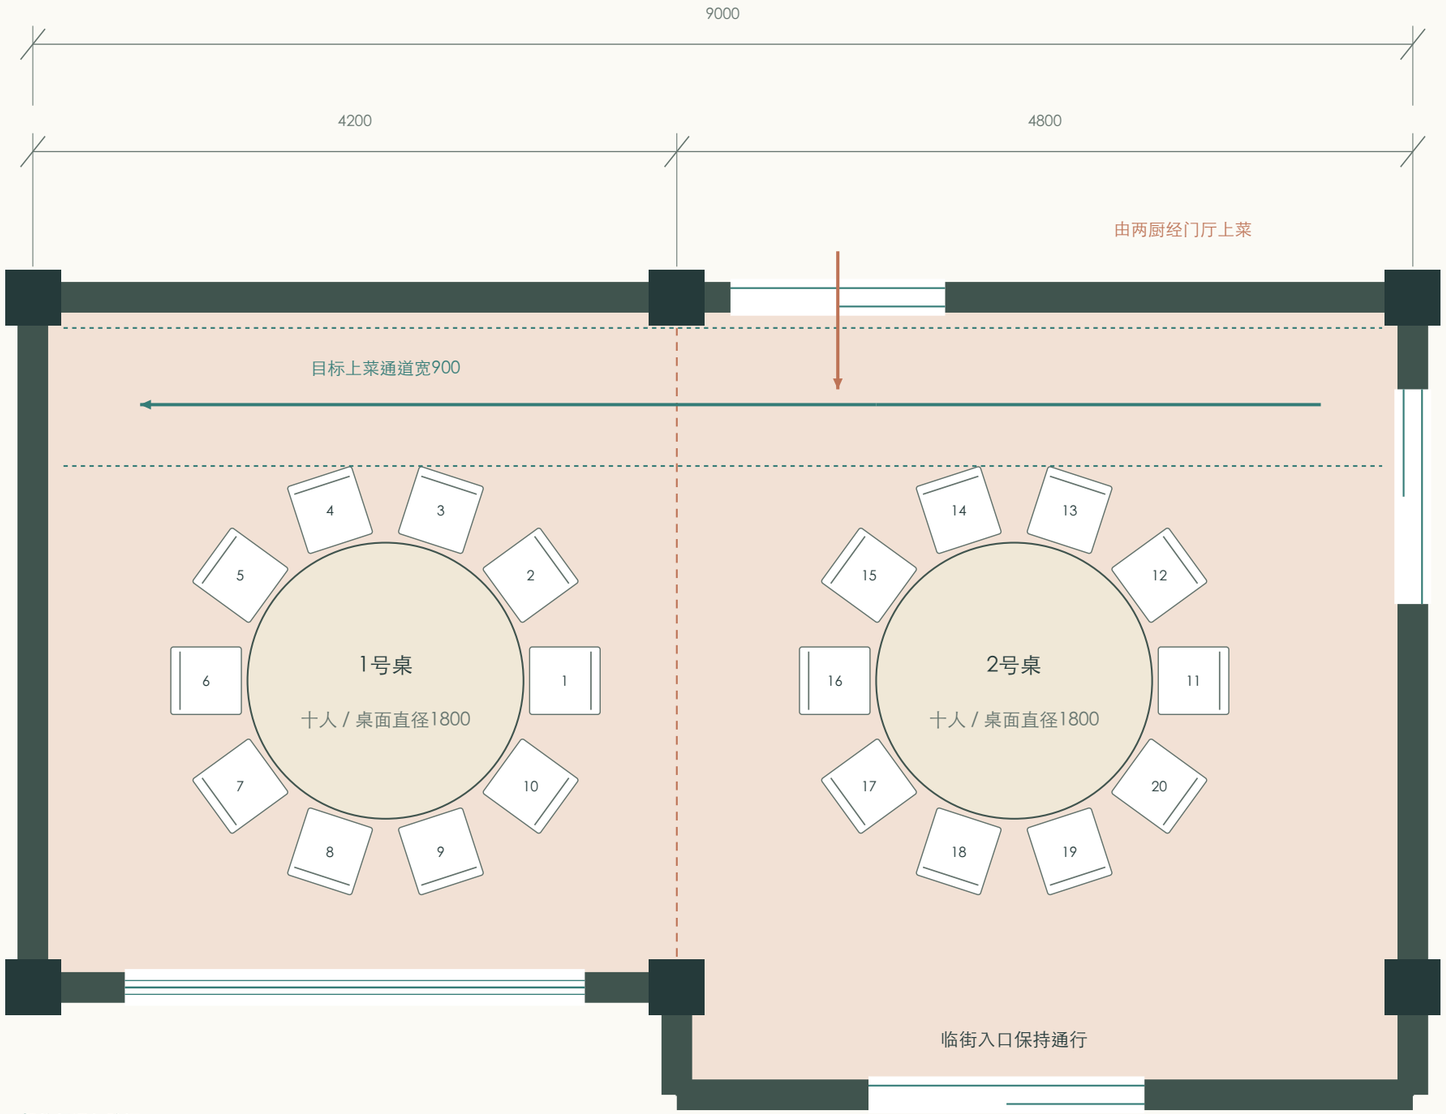

餐位与通行验证

图中明确绘制并编号20把椅子，配置两张直径1800毫米的餐桌。每桌连同就座空间的直径约2800毫米；北侧主上菜通道在结构协调位置处以900毫米为目标。南侧为次要余量。

备餐及上菜流线

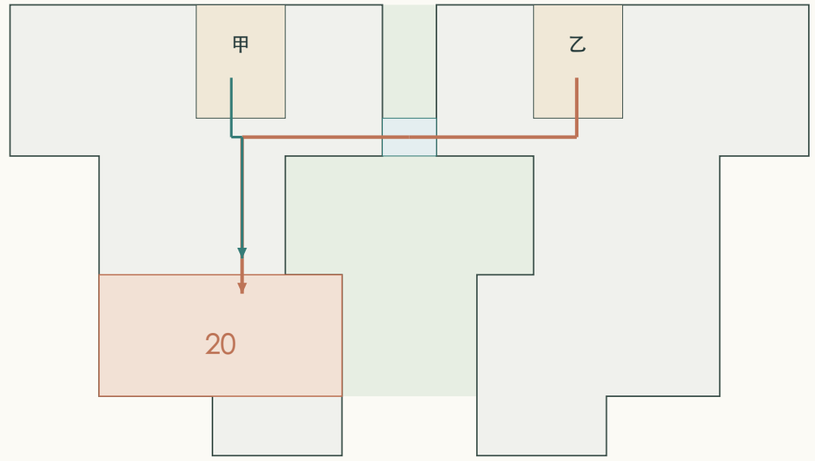

1. **一厨主烹饪，一厨协助**

   甲户承担主要热菜，乙户按需要协助备菜与清洗。生食处理与待上桌熟菜应分开组织。

2. **后部设置局部避雨连接**

   轻型雨棚遮盖后部走廊之间约2米的跨越段，使人和菜品在雨天无需横穿露天天井。

3. **桌椅与临时家具安排**

   甲户门厅预留约1000×2100的收纳柜，须按实际桌椅核对。春节时将甲户轻型模块沙发临时移至乙户堂屋侧墙，腾出餐桌位置。


4. **保留主要结构协调位置**

   虚线位置改为宽敞连通口。保留必要的柱、梁与传力路径，须完成结构设计后再确定开口构造。

首层长辈生活与日常转换

长辈生活与日常转换 | 首层卧室、同层浴室、安静休息与节日活动并存

甲1 / 乙1：预留护理侧，缩短夜间如厕路线

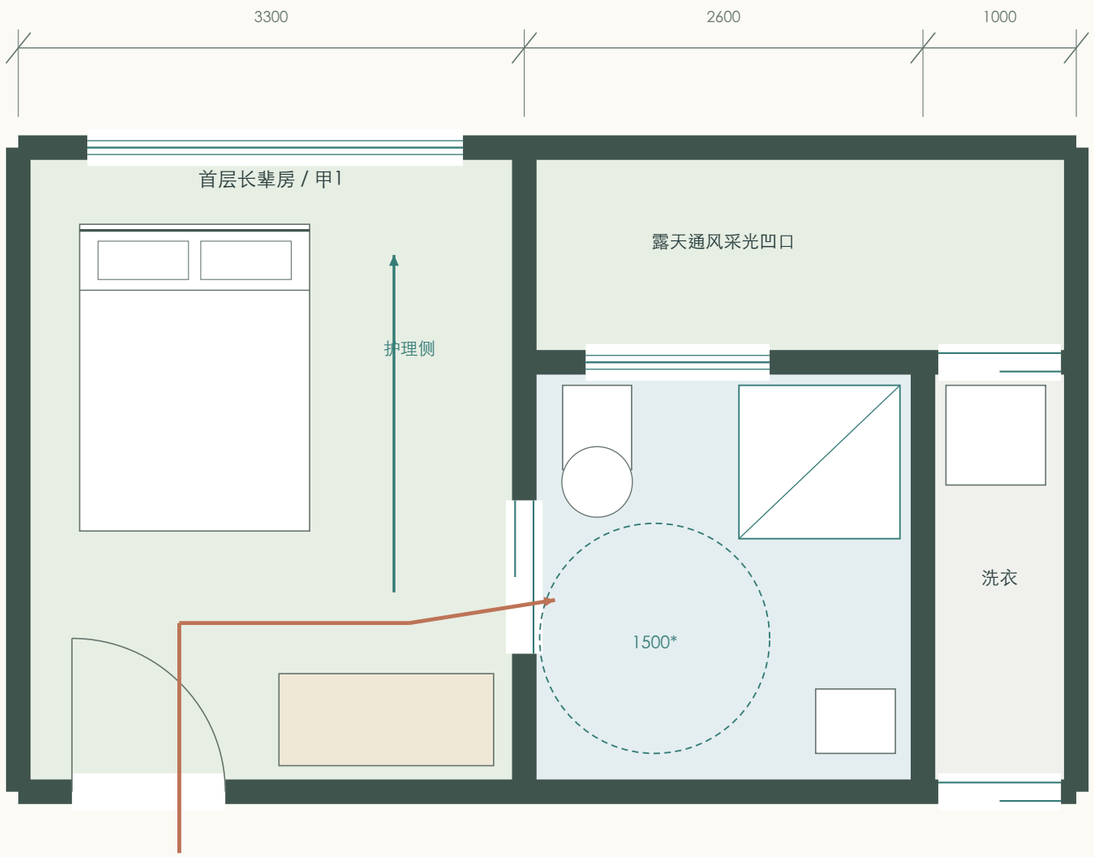

*虚线圆直径1500毫米为布置目标，须结合完成面与实际洁具复核。

浴室入口尽量平顺，采用防滑地面，预留扶手基层，开关易触及，并设置夜间照明。床侧预留一侧较宽的护理通道；尚未完成正式无障碍合规核验。

1. **首层就是一层，长辈不爬楼**
   甲1与乙1均在入户层。日常用餐、如厕、淋浴和主要家庭活动均可在同层完成。
2. **长辈休息与热闹活动分开**
   长辈房位于后部，与前厅活动分开。重视门窗隔声、保温与独立温控，并结合邻房遮挡核实实际日照采光。
3. **饭后甲户：十人看春晚聊天**
   折叠餐桌收起后，两张三人沙发配四把活动椅，形成十人的春晚与聊天区。
4. **饭后乙户：分成两组活动**
   外侧客厅安排四人棋牌，堂屋安排六人茶叙，合计提供另一组十人的活动位置。
5. **平日保持便捷好用**
   日常在后部餐厅用餐。布草、洗衣、食品和聚餐桌椅均有指定位置，避免长期堆放在交通通道中。

饭后活动人数验证


甲户看春晚聊天10人 + 乙户棋牌4人 + 乙户茶叙6人 = 20人

采用活动家具，兼顾不同年龄家人的团聚与安静休息。

简洁体量，遮雨入户

建筑体量与剖面意向 | 前部两层 + 后部三层，露天天井与分户露台

南向入户立面：概念比例与材料意向

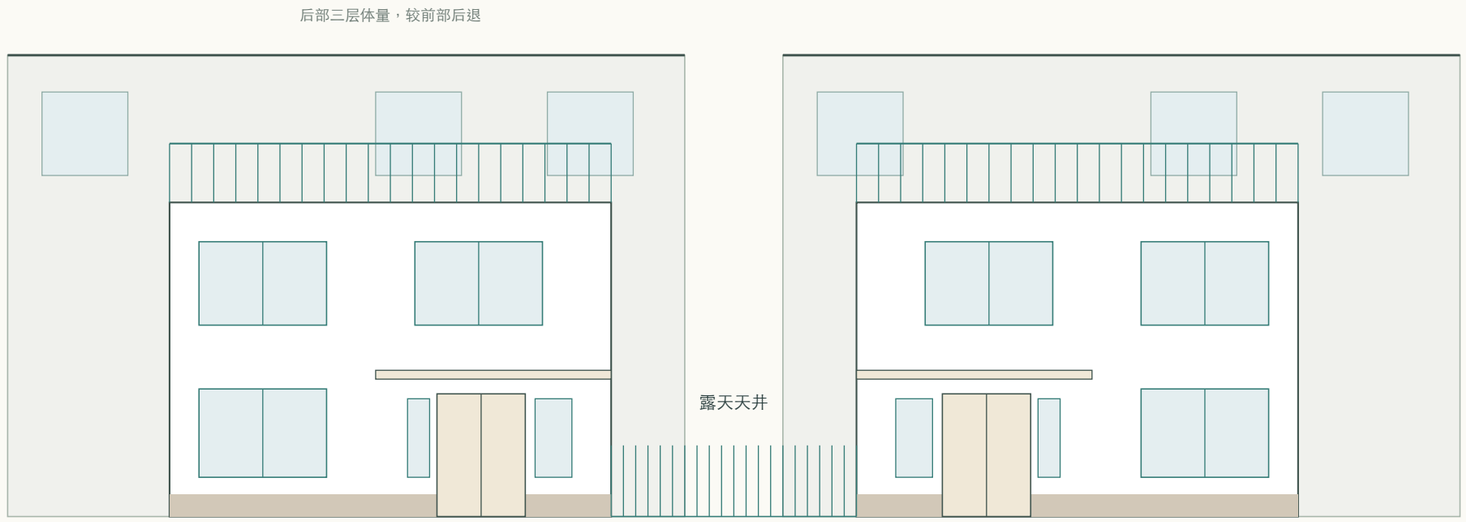

暖白色墙面

简洁抹灰墙面，选用当地易维护的耐久涂层。

耐久墙脚与入户区域

易溅水位置采用适量石材或瓷砖防护。


减少门窗规格种类

统一可开启窗型，控制种类与维护成本。

露台首先是一套屋面系统

落实保温、防水、排水与安全围护。

天井剖面示意：露天空间与分户露台

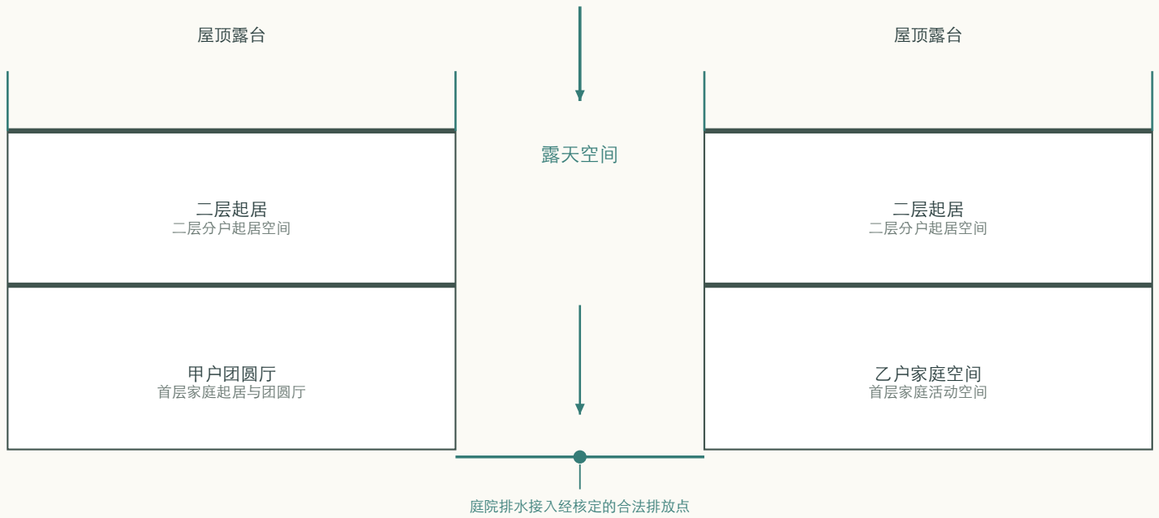

1. **中央天井保持露天**

   不封闭天井顶部，上层不设连桥。后部小雨棚仅遮盖首层跨越段，中央天井仍保持露天。

2. **统一深化所有防雨节点**

   统筹露台找坡、雨水口、溢流、门前截水、泛水、防水上翻及屋面保温，避免各工种各做一段。

3. **层高与标高仅为方案建议**

   方案层高暂按首层3.3米、二层3.1米、三层3.0米。露台围护示意高1.2米，须按适用规范进一步核定。

4. **根据实测标高安排平顺入户**

   结合地形实测确定室内地坪、庭院排水坡向及平顺入户路径，避免先砌台阶后补坡道。

家庭需求与房间统计

设计说明 | 固定条件、房间数量与使用场景

保留原图十四间卧室及两户独立生活格局，两户首层各有一间长辈房。甲户前部家庭空间承担二十人室内共同用餐；中央天井保持露天。

楼层	甲户 / 左侧	乙户 / 右侧	合计
一层	甲1: 1	乙1: 1	2
二层	甲2-甲5: 4	乙2-乙5: 4	8
三层	甲6-甲8: 3	乙6: 1	4
保留卧室合计	8	6	14

本次方案的主要调整

可以转换用途的团圆厅

甲户前部客厅与堂屋连通，主要开间的结构位置作为深化协调依据。两张直径1800毫米的折叠桌提供二十个紧凑型家庭餐位；实际家具与通道须进行实尺寸复核。

十四处卫浴完整保留

一层四处、二层六处、三层四处，共十四处，其中十二处带淋浴、两处为客卫。长辈浴室保留较大尺度；上层后部每户设两间约1.8×2.8米共用卫浴，均从走廊进入。

每户两间独立洗衣房

一层后部设约1.0×2.8米洗衣间，三层门厅外墙侧设约1.2×2.6米洗衣间，三层可就近到露台晾晒。洗衣机、盆、门扇与净通道须按实际设备复核。

沿用原方案两户卧室分配

原图为左侧八间、右侧六间卧室。本方案保留这一分配，不另行调整两户的卧室数量与归属。

春节团聚的完整使用过程

到家：入户避雨，鞋衣有处放，客人可使用首层客卫。

备餐：两厨协作，菜品经后部走廊和局部雨棚转运。

聚餐：甲户室内二十人共同用餐，不依赖露天天气。

饭后：甲户春晚聊天十人，乙户棋牌四人、茶叙六人。

夜间：卧室与布草收纳独立于前部热闹活动区。

待确认：过夜人数、烹饪燃料、长辈行动能力，以及两户共同待客的具体安排。

总预算控制在二百万元

预算控制 | 两户合计，包含室内、设备与庭院；以下为控制额度，非当地报价

二百万元按两户全部费用合计控制，包含室内、设备和庭院。下表是用于询价的分项控制额度，并不证明可按这些价格建成。目前尚无经核实的祁东本地施工报价及地勘资料。

费用项目	控制金额 / 元	占比
主体、基础、楼板与楼梯	970,000	48.5%
门窗、外立面、保温与防水	240,000	12.0%
给排水、电气、热水及通风	200,000	10.0%
基础装修、两厨、十四卫浴及四洗衣间	270,000	13.5%
基本活动家具及家电	60,000	3.0%
庭院、外部接驳及排水	50,000	2.5%
设计、测绘及专业协调	40,000	2.0%
预备费	170,000	8.5%
预算总上限	2,000,000	100.0%

为什么必须按实际工程量询价

按本次几何示意估算：各层室内面积合计约766平方米，另有入户雨廊及前阳台约29平方米、露台约113平方米，以及建议新增的局部雨棚约2.8平方米。数据按示意轴线包络计算，室内面积已扣除后部露天凹口，并非法定建筑面积。

在这一体量下，二百万元全包预算偏紧。地基、挡土、外部接驳、较大结构开口与装修标准均会明显影响造价。保留十四间卧室，基础装修应简洁实用。

控制费用时应优先保障

屋面和露台防水、保温门窗、排水与污水处理、长辈浴室、厨房排烟、电气及结构设计。

装饰吊顶、大面积石材、复杂定制柜和露台家具可先简化。团圆厅大开口与局部雨棚应单列报价，不能藏在笼统的每平方米单价中。

接受施工报价前应完成

由当地造价或施工人员按工程量列出分项报价，注明包含范围、排除项及税费；确认拆旧、地基处理、挡土及外部接驳费用。开工前按完整范围核对二百万元总上限。

设计依据与专业深化交接

设计依据与深化任务 | 供家人讨论及当地建筑师、结构与设备设计人员深化

图示尺寸与结构符号的含义

依据原图后部宽29600毫米、前部开间宽23000毫米、总进深16700毫米作为参考。新方案调整分隔并规整天井局部边界；示意主墙厚200毫米、隔墙厚120毫米。实际厚度须深化核定。方形符号仅为主要开间结构协调位置，不代表已核定的柱或柱尺寸。

已确认的家庭要求

地点为湖南祁东；两户独立生活，有年长家人；首层必须设置长辈房；春节约二十人共同用餐；天井保持露天；设置屋顶露台；卧室总数与原分配保持不变；室内、设备和庭院等所有费用合计二百万元。

尚缺少的技术资料

尚缺实测地形、彩色权属界线、批准用地及退界、邻房高度、场地标高、地质条件、结构体系、基础设计、常住及过夜人数、烹饪燃料与设备清单。该方案不构成规划许可、结构安全或规范合规的证明。

建筑与工程专业需要落实

先核定合法建设范围与实测标高，再深化团圆厅开口及结构传力。复核楼梯踏步和净高，协调防水、露台围护、门槛、排水能力、污水或化粪池、厨房排烟及热水需求。团圆厅定案前应使用实际桌椅完成二十人实尺寸布置。

本套图纸已核对的内容

卧室按甲1至甲8、乙1至乙6标识，并在各层图中对应；团圆饭详图明确编号二十把椅子。主要平面为矢量图，以A3原尺寸打印时比例1:100；团圆饭及长辈房详图比例1:40。体量、剖面及使用流线为解释性方案示意。

业主提供的原始参考图纸

原始一层平面图（序号4）	首层功能及尺寸参考
原始二层平面图（序号5）	二层功能及尺寸参考
原始三层平面图（序号6）	三层功能及尺寸参考
原始场地图（序号7）	界线以颜色区分，当前文件显示为黑色

官方技术与管理参考资料

《湖南省农村住房建设管理办法》

《湖南省好房子建设技术导则（2026版）》

本项目具体适用的现行规范及审批要求，须由当地设计与主管部门核定。