两栋分开，中间采光，后部连厅

14间卧室 · 14处卫浴 · 2间厨房 · 2间日常餐厅 · 21张床 · 每户二层洗衣间 · 甲户农具间、两户储藏间




两栋楼各向外移1米，单栋尺寸不变，总宽29.6米，上层恢复2米间距；一层保留2×5.6米后部连接厅，餐厅南侧仍开敞。南端5米花窗墙连接实体外墙，天井围合且露天。原柱位保留，柱身与墙同色；两端各新增南端转角柱，贯通首层至屋顶；取消二层露台8处多余柱段。勒脚连续包过窗下与柱脚，门口断开。

首层层高3.9米，二、三层各3.3米；室内外高差450毫米，主要入口设三级150毫米台阶，农具间另设推车缓坡。二楼露台及三楼楼板取消范围按标记保留。

天井高窗固定配窄扇；厨房、餐厅4处北窗四折，影音室2处北窗中间固定、双侧窄扇外开，卫浴上悬、楼梯固定窗保留。封面为网页同一三维网格的离线投影。

一层：走廊围护与天井入口

玄关、客厅、楼梯不设分隔门墙；卫浴、外墙、后门及院墙保留。

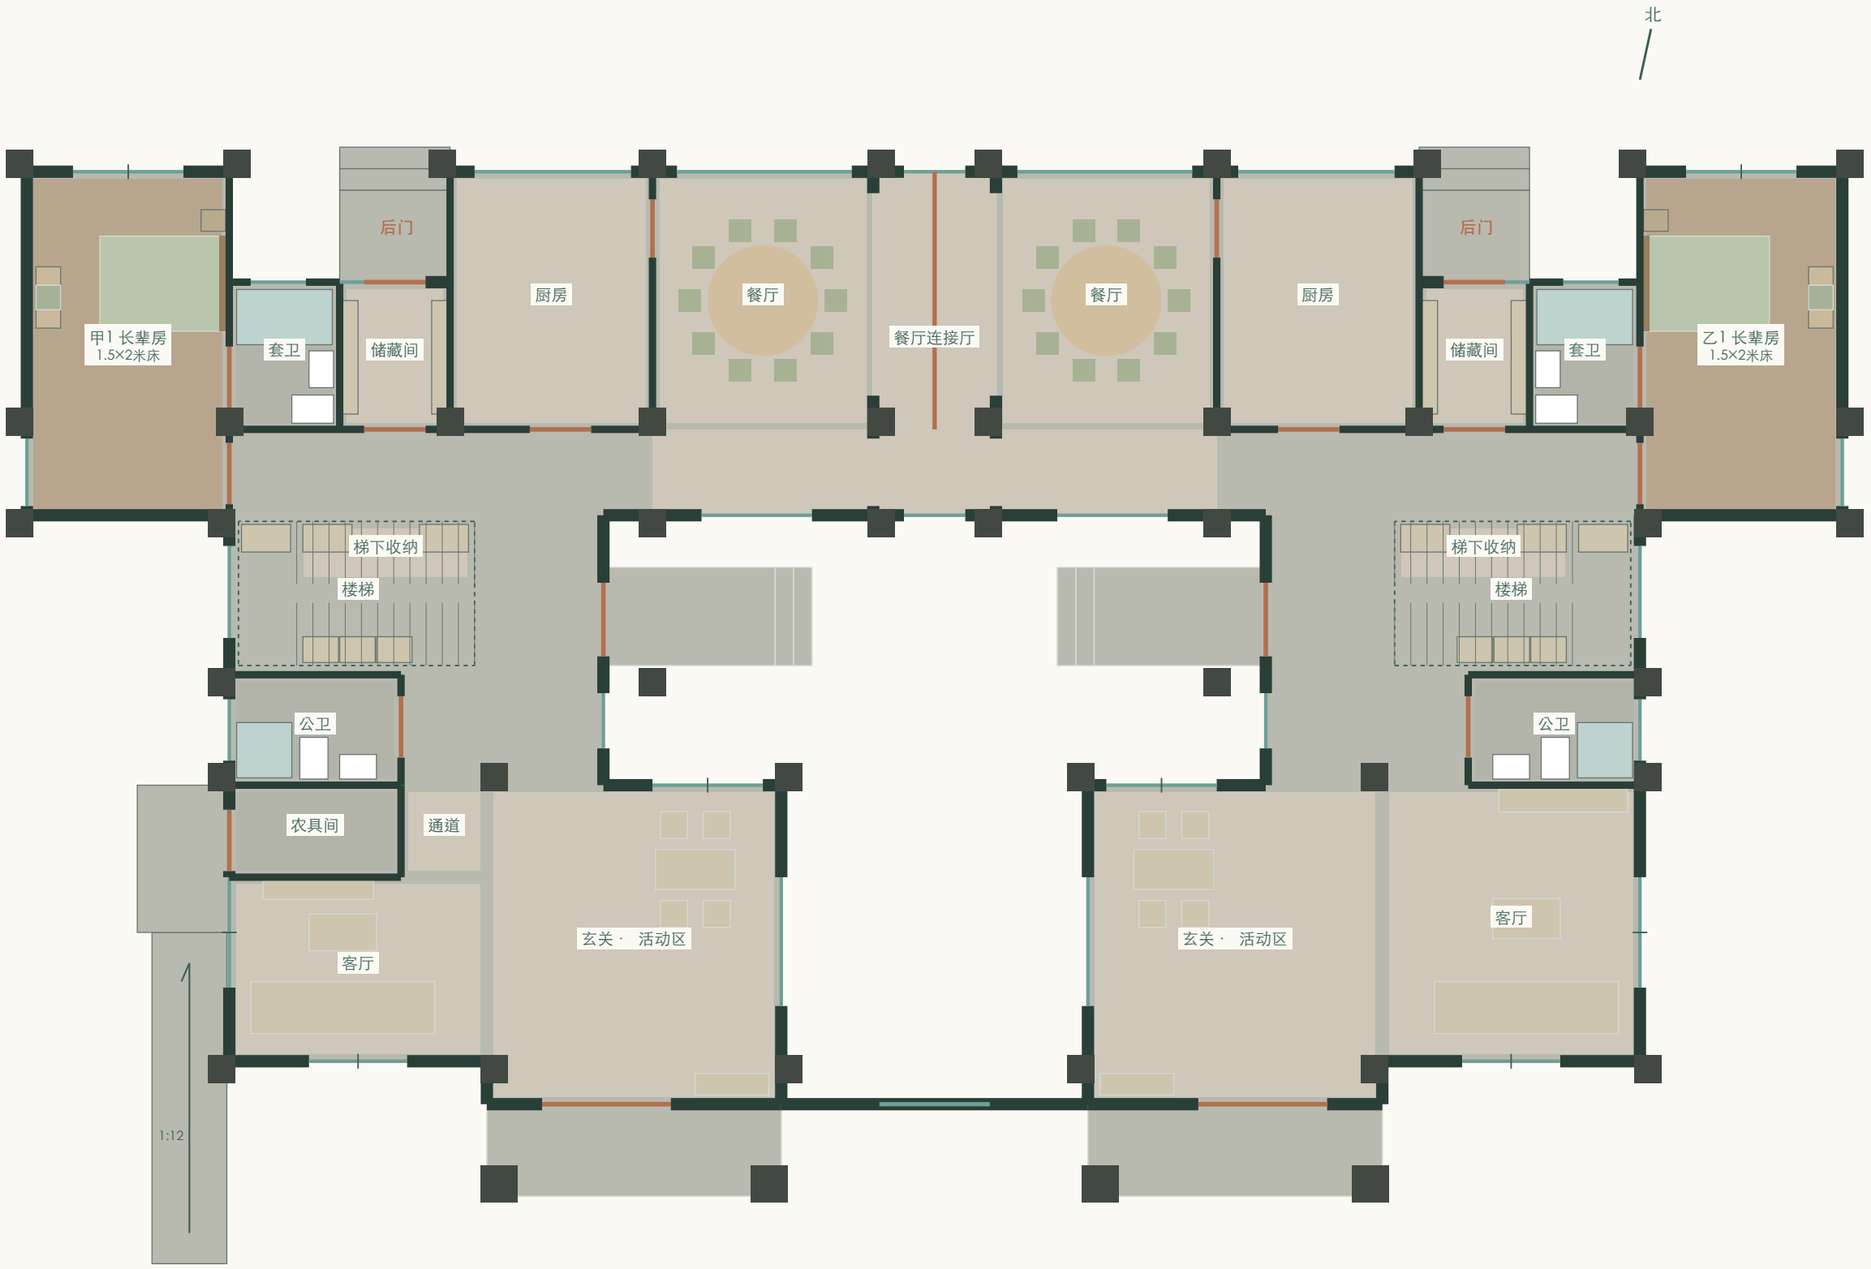

01

长辈房、厨房与四处卫浴保留，卧室不新增朝天井的洞口。

02

每户走廊设1.20米外开玻璃天井门；门外2.80米深平台，再接三级150毫米台阶。

03

天井门旁两侧窗改0.90×1.35米固定玻璃，窗台1.10米、窗头2.45米，与门头齐平；中央南窗沿用原分格。

04

两餐厅经后部连接厅连通，中央4.20米活动屏风可整块移走；取消隔断线上的短墙与横挡墙，地面同标高连铺，春节两桌20人同餐。

05

两端侧墙各三柱，新增南端柱贯通；甲户后角设4.2平方米农具间，乙户恢复完整客厅；两户均保留厨房旁储藏间。

墙线：深灰 窗：青绿

门：棕色 栏杆：蓝色

二层：有顶走廊围合，露台保持敞开

四处门位按黑色标记调整；转折通道延伸屋顶补齐，套卫保持独立。



01

8间卧室保留；甲5、乙5旧入口及短隔墙拆除，套卫门墙保留。

02

卫浴旁侧门1.00米进卧室，南端1.10米门进洗衣间，再由0.90米门通露台；北端原露台门墙取消。

03

侧走廊窗同步高窗与窄开启扇；中央南向六窗加高，大固定玻璃配0.45米开启扇。

04

转折通道由低坡内翼补顶，天井侧恢复墙，前露台保留矮基座金属栏杆。

05


前套卫、后排可切换卫浴及其双入口保留；露台不放室内电视。

墙线：深灰 窗：青绿

门：棕色 栏杆：蓝色

三层：恢复走廊外墙，以窗借光

取消楼板与低坡翼顶范围不变，不设通向屋面或空洞的门。

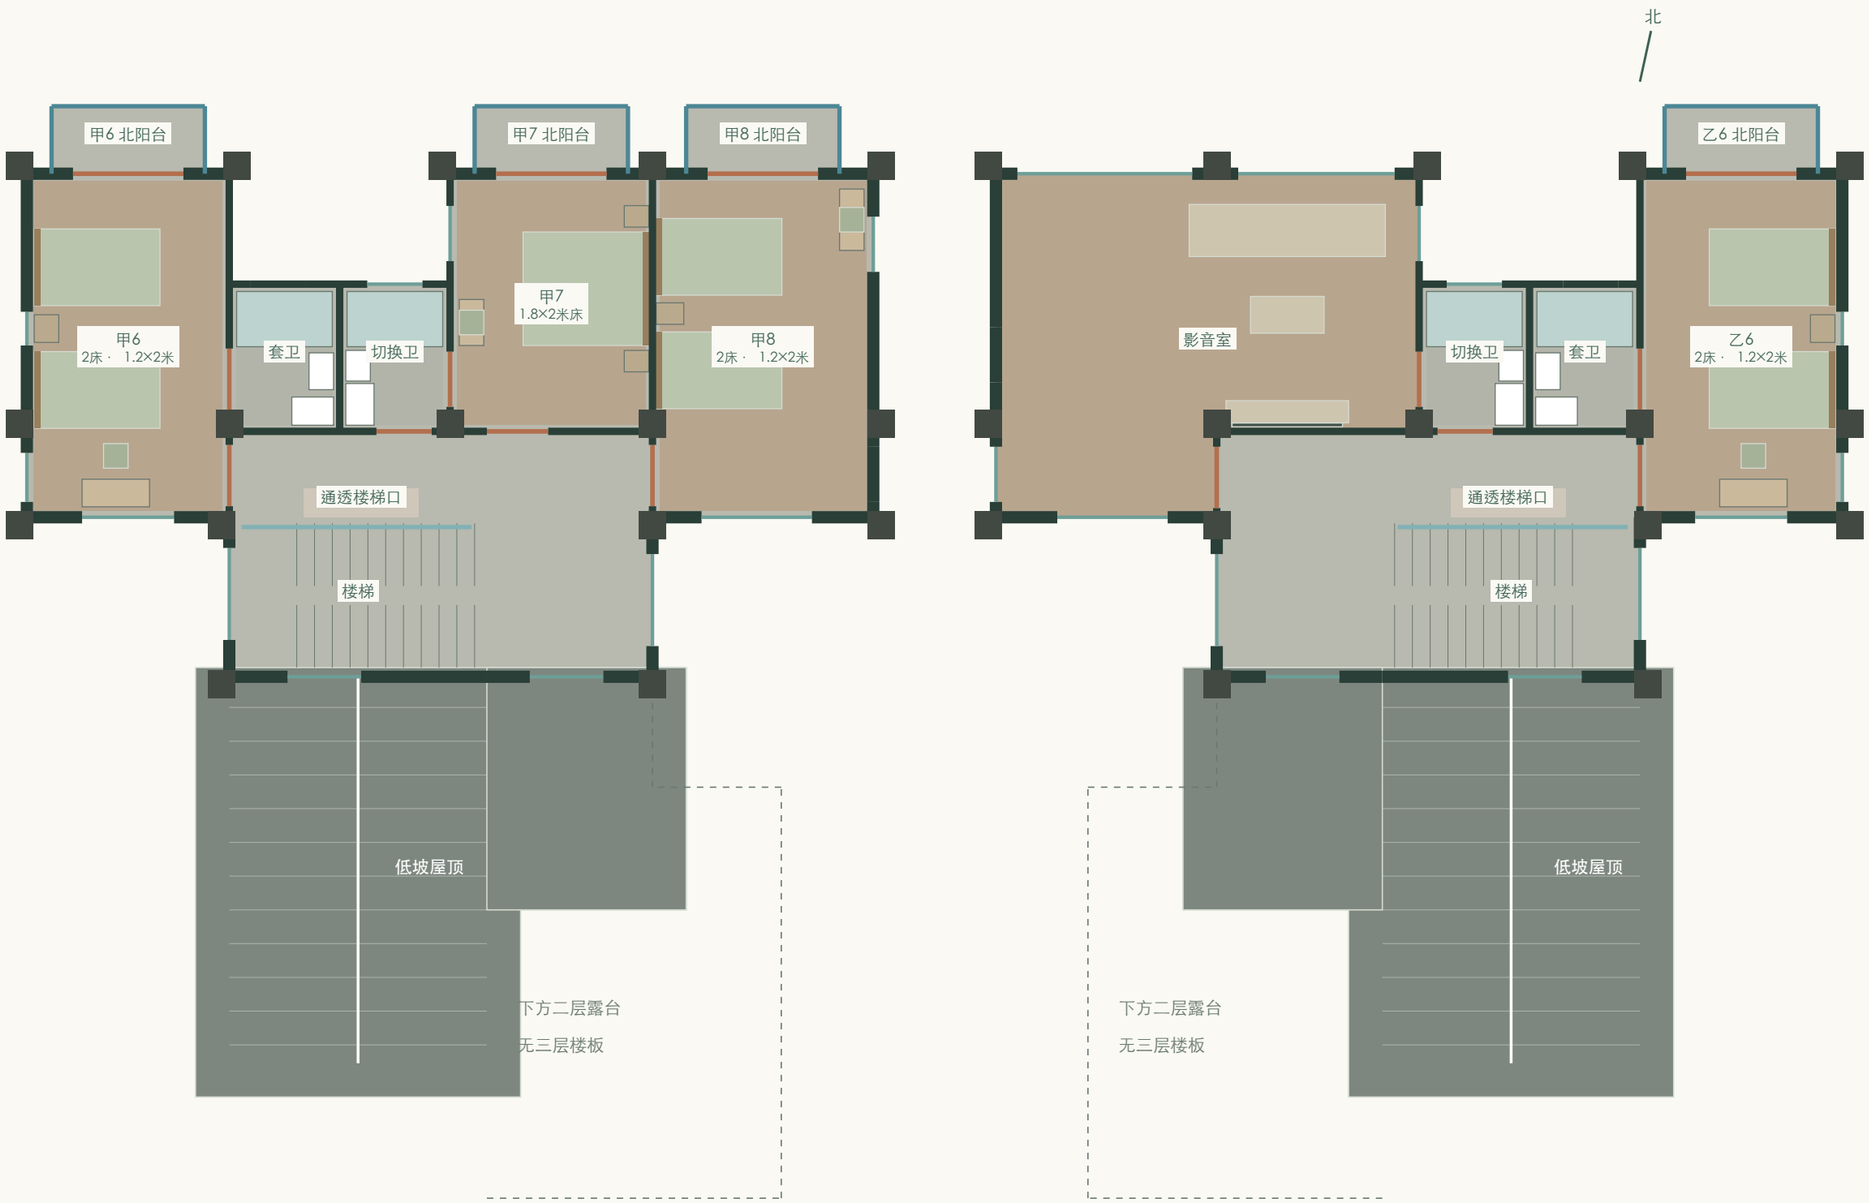

01

甲户3间卧室、乙户1间卧室及影音室保留。

02

侧走廊及后排外墙保留；楼梯与走廊间实墙改玻璃栏杆。

03

侧窗保留，四扇小南窗统一1.20×1.50米；后排南向高窗仍1.80×1.85米，窗台1米，窗头2.85米。

04

侧窗上下对齐、窗框统一炭灰；中央窗主玻璃固定、窄扇外开，楼梯窗继续固定。

05

主顶与楼梯保留；楼梯北侧实墙改1.20米高玻璃栏杆，东侧上楼出口敞开。

墙线：深灰 窗：青绿

门：棕色 栏杆：蓝色

天井走廊窗：主玻璃固定，窄扇通风


原洞宽1.80米，统一加高为1.85米；窗台1.00米、窗头2.85米，把手中心约1.50米。

关闭 / 约75%固定 + 25%开启



分格及开合意向，非门窗加工图

开启 / 仅45厘米窄扇向外开

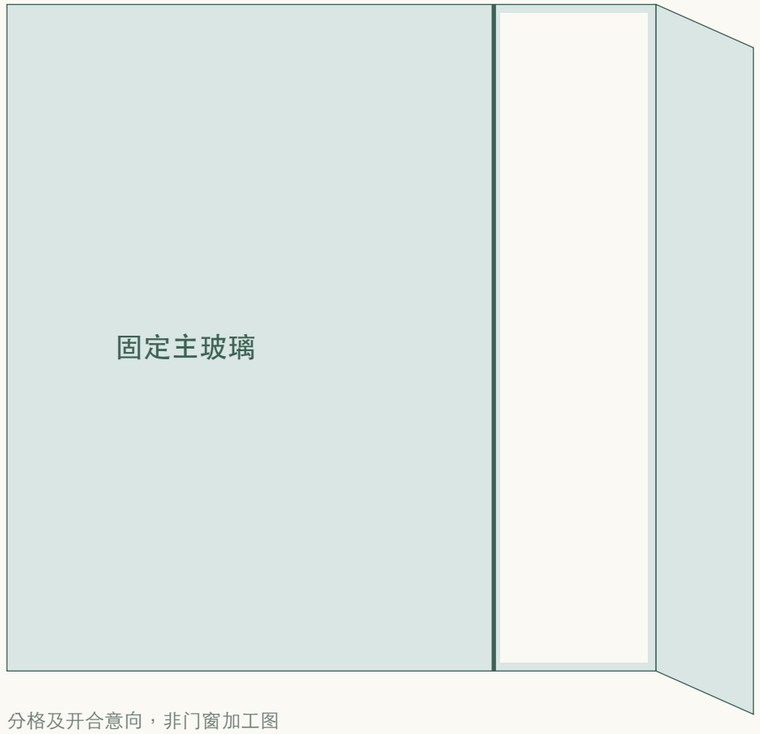

分格及开合意向，非门窗加工图

一至三层后排朝南、朝天井的6扇窗采用同一比例；两户开启扇在外侧边缘镜像布置，形成安静、连续的竖向节奏。固定主玻璃保持不动，网页点击只开启窄扇。


8处天井侧窗和三楼2处走廊南窗也采用固定主玻璃 + 窄扇。其余12处宽窗双扇中分、4处大窗四扇折叠，影音室2扇北窗中间固定、两侧窄扇外开、18处窄窗单扇外开；14处卫浴及2处洗衣间为上悬窗。8处楼梯窗固定；10组卧室北侧门窗改为通高双片玻璃推拉。

窗头提高后，窗过梁及梁底净高需结构协调；玻璃、五金、纱窗、防雨、限位和实际通风面积须正式设计。不能以模型开度代替产品性能与全屋通风验算。

团圆宴：隔断打开，两桌20席


一层保留连接厅，餐厅合并轴线范围约9.2×4.2米，约38.6平方米。

平日：隔断关闭，各自用餐

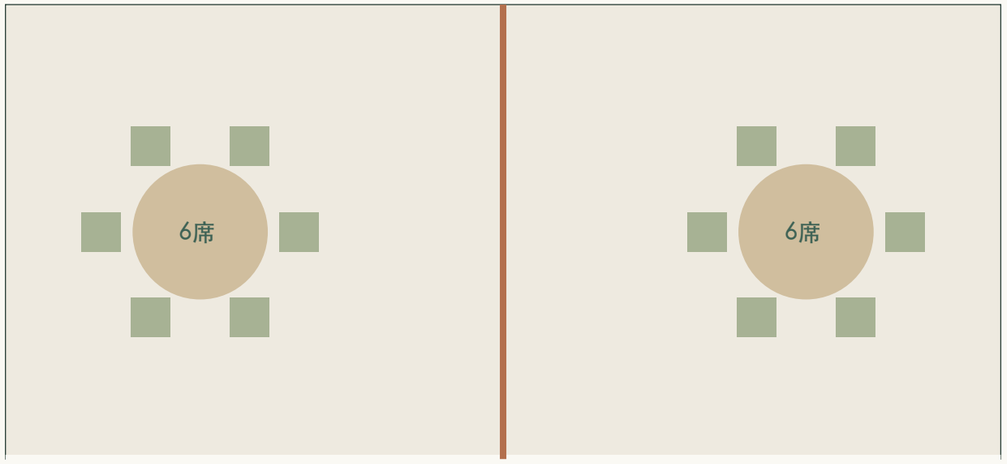

南侧开敞连接长走廊

春节：隔断打开，共20席

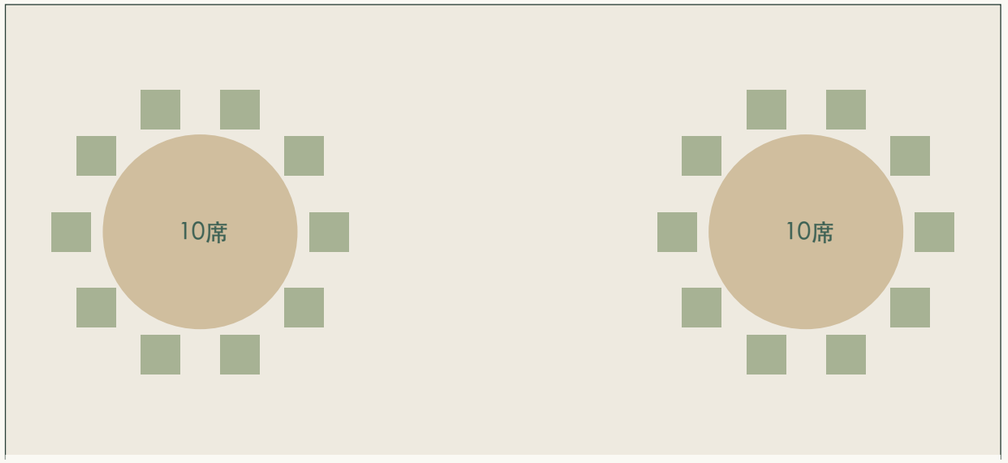

南侧开敞连接长走廊

桌椅为布置意向，保留通向厨房和公共走廊的入口；中间活动隔断不承重。实际家具尺寸与拉椅、端菜通道应现场放样确认。

两户一层梯下均改半开放收纳，甲户另设农具间，两户均保留独立储藏间；洗衣机移入二层露台入口双门洗衣间，走廊与露台各设一门。14处卫浴均保留淋浴区、坐便器及台盆，二、三层4间可切换卫浴仍采用双入口。

本轮恢复走廊围护及取消楼板均为尚未开工阶段的方案调整。连接厅与两栋的连接、露台边梁、栏杆锚固与坡顶荷载须由当地设计人员统一设计，不能据模型直接施工。

预算与落实：先核结构，再按同一清单报价

总预算约200万元，涵盖建筑、内装、机电与院落；本轮不承诺当地成交价。

几何范围已经明确

单栋13.8米开间与室内房间尺寸不变，两户恢复旧版2米间距，总宽29.6米；一层保留连接厅，三层前部露台楼板仍取消。

材料保持克制

暖白耐候墙面、烟陶红低坡屋顶、暖灰薄基座与哑光暖灰铜细竖杆；减少石材、装饰线脚和复杂定制。后排南向高窗为固定主玻璃配窄扇，其余窗保留；前部小屋顶左右分坡、纵向向南降低。

结构需重新组织

没有既定结构图。两栋各自柱位保留；连接厅及两侧节点、基础、抗震与沉降策略须正式计算。

防水与雨天使用

有顶走廊恢复带窗围护，二层前段和露台仍露天；天井门外平台、台阶、露台、檐沟及二层洗衣间分别协调防水、排水与检修。露台栏杆须完成支承与锚固设计。

拿去报价的内容

先核现场边界、朝向、高程和审批条件，再形成结构、门窗表、栏杆、屋顶及防水节点和工程量；按同口径向当地单位询价。

烟陶红 · 推荐

暖石板灰

深炭灰

灰橄榄

砂岩褐

地面选材：温暖、耐用、便于维护

四组瓷质砖控制材料种类；室内外采用协调色调，按不同湿水环境选择具体表面。



客厅 / 餐厅 / 玄关 / 厨房

暖米灰细石纹瓷质砖 / 800×800毫米

暖米灰、细石纹、细腻哑光。客餐厅尽量连续铺贴，厨房选厂商明确适用的易清洁表面。



卧室 / 影音室

浅橡木色木纹瓷质砖 / 200×1200毫米

低饱和浅橡木色，顺直或不超过三分之一错缝；不做人字拼，避免偏橙、强木结。



天井 / 露台 / 开敞走廊

暖浅灰室外石纹瓷质砖 / 600×600毫米

暖浅灰、细防滑石纹；按室外湿区适用性选样，兼顾泥水清洁与排水。楼梯从同色系列裁制踏步。



卫浴 / 淋浴区

暖灰卫浴防滑瓷质砖 / 300×300毫米

暖灰细防滑砖，配近色灰缝；适用于赤脚湿区，便于围绕地漏找坡。

砖缝采用近色灰，宽度按具体砖厂说明和实际尺寸偏差确定，拒绝零缝铺贴。先做样板，比较湿水、茶渍或油污清洁后的实际表现。木纹是瓷砖的视觉效果，仍保留硬质脚感。

控制费用：主砖集中采购同批次与同色号；卧室才使用木纹，避免拼花和超大板；报价包括找平、防水、粘结、勾缝、收边、运输、损耗与人工，不只比单片砖价。

材料性能与维护参考： 瓷质砖与低吸水性 室外瓷砖与易清洁表面 湿区适用分类 留缝与铺贴说明

门色：入口有重点，室内轻而安静

两户采用同一套色彩；门框与门扇尽量协调，五金统一哑黑。以下为色彩意向，须现场饰面样板确认。




入户门

烟熏胡桃色




卧室及普通室内门

浅灰橡木色

 

卫浴门

暖灰米色

 

北侧后门

深暖灰



天井 / 露台门框

炭灰细框

入户门用压低橙黄的中深烟熏胡桃色，作为外观的温暖重点；室内门用更轻的浅灰橡木色，衔接卧室地面。卫浴用暖灰米色，后门用深暖灰，玻璃门框与窗框统一炭灰。


外部门按户外耐候饰面选样，室内、卫浴按各自环境选门体；色彩相近不表示门体材料必须相同。板材、包边、锁具、耐湿、开启与必要的消防要求须按最终产品和正式设计核对。

色彩比手机或打印图更可靠的判断方式，是把门样、地砖、墙面、栏杆及屋顶色板放在现场同一光线下比较。

大窗四折：平日采光，需要时折叠打开

厨房、餐厅共4处北向大窗；影音室北窗改为中间固定、双侧窄扇外开。

关闭 / 四扇分格

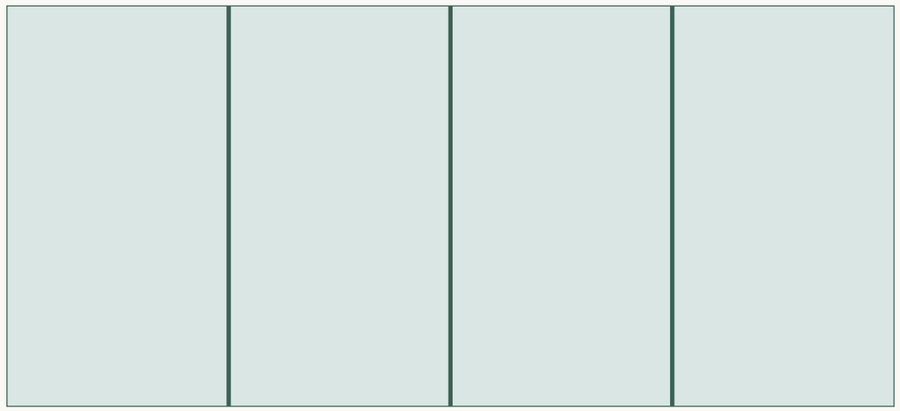

示意 / 正立面

打开 / 左右各两扇向外折叠



示意 / 平面折叠，不按比例

每侧两扇组成折叠对，模型展示向外折约85°，中间不留固定玻璃。点击大窗可打开，再点关闭。厨房与餐厅每户各1处，共4处；影音室北侧两大窗改用固定主玻璃配双侧开启窄扇，详见本册末页。

安装前核对玻璃重量、折叠五金、轨道与清洁维护方式；开启时的室外窗扇空间、纱窗、排水与气密水密性能按实际产品深化。普通窗不改成折叠窗，控制定制范围。

北侧：只给卧室小阳台

二层6处，三层4处，共10处；影音室不加阳台，北窗采用双侧开启扇。




每处约2.50×1.10米，新增阳台投影共约27.5平方米。原1.80米洞口统一为2.45米高的双片玻璃推拉门。靠书桌侧固定，另一片平移收拢，模型通行口约0.82米；原洞宽不变；床与书桌按最新床型表调整。

栏杆统一哑光暖灰铜与暖灰薄基座。模型仅表达空间及外观；阳台悬挑、边梁、锚固、防水、排水、门槛及总造价须正式核定，未据此完成承载或合规验算。


二层洗衣、一层梯下半开放收纳

两户镜像设置；洗衣间双门连通，梯下为敞开入口、低柜、搁架与格栅。

二层洗衣间 / 1:30

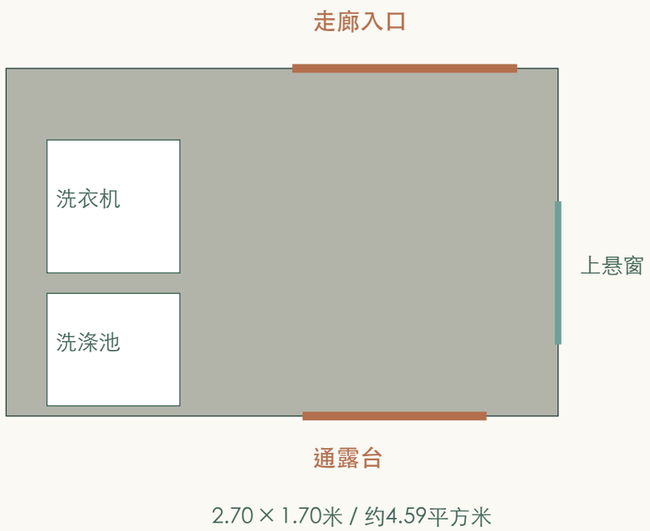

一层梯下半开放收纳 / 1:40

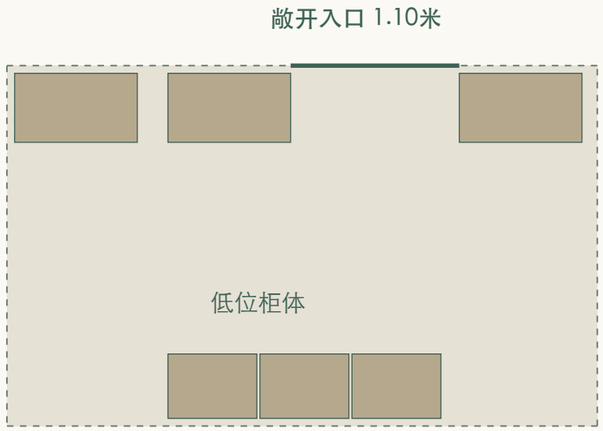

虚线为楼梯投影，入口不设门。

两侧低柜配开放搁架与疏朗木格栅。

洗衣间：每户二层露台北侧约4.59平方米，走廊与露台各一门；设备、门扇和侧窗保留。轻质围护、设备荷载、防水与排水须联合设计。


梯下收纳：取消门与整面封墙，北侧原楼梯隔墙同步取消，中央1.10米入口敞开。低处阶梯式带门柜，高处开放搁架，两侧浅灰橡木格栅轻遮挡；低矮处只放物品，不作站立通道。

农具入甲户专用房间，季节用品入各户储藏间；梯下以鞋、雨具、常用杂物为主。通风、防潮、照明及实际梯板下净高须深化。


卧室北侧门窗：整幅玻璃，同高细框

10组统一为1.80×2.45米通高推拉门；靠书桌侧固定，开启侧向其收拢。

闭合 / 两片完整玻璃

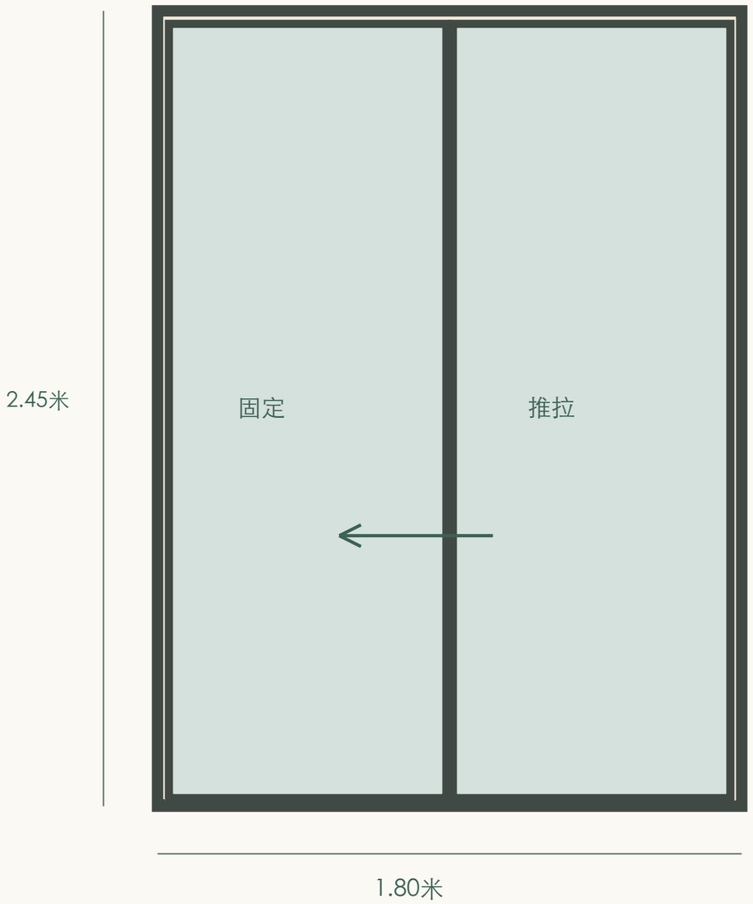

开启后 / 约0.82米通行口

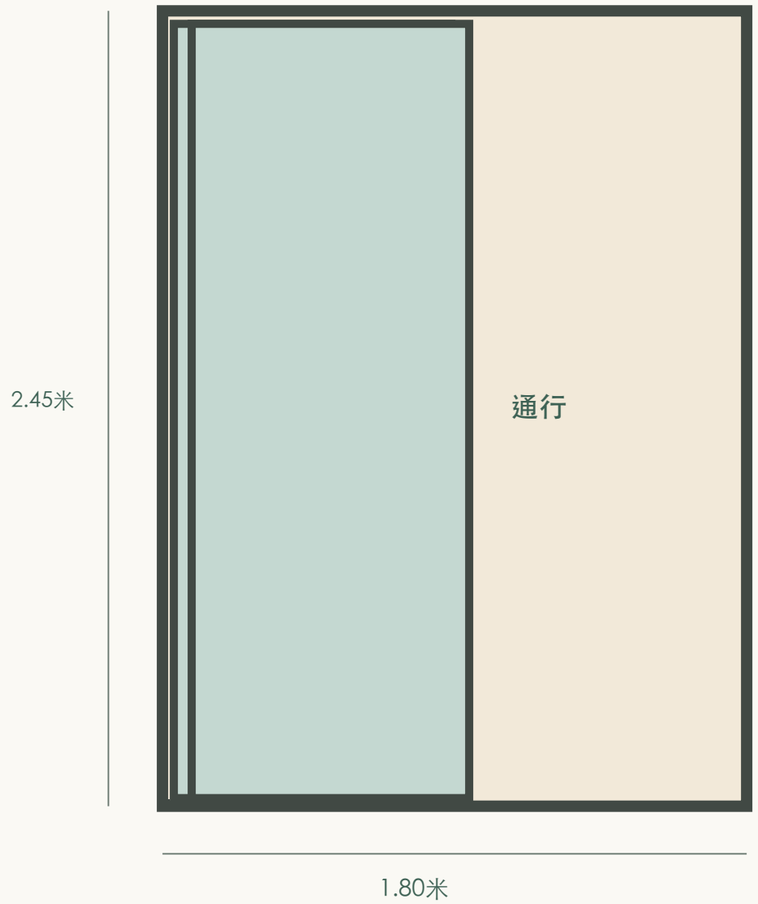

设计：整组同高、统一外框，仅留一道中央接缝，玻璃一直延伸至低轨。每间房按书桌位置镜像设置固定侧，推拉不占用室内及1.10米深阳台的门扇回转空间。

模型意向：外框约35毫米、扇框约25毫米、闭合中缝约70毫米，低轨约20毫米，模型通行口约820毫米；均不是成品加工或验收尺寸。

采用配套外门系统，实际净开口、安全玻璃、密封、五金、纱门、轨道清洁、门外截水与阳台找坡由门窗深化及施工图共同落实。原洞口位置及宽度保留，不据此认定结构验算已完成。

一层：农具、干储分开，生活动线保持敞开

甲户设农具间约4.20平方米；两户各设储藏间约4.32平方米，乙户恢复原客厅。房屋轮廓不变。

甲户农具间 2.80 × 1.50米




室外直接进出 · 1.00米门洞

只取甲户客厅后部外侧角落，甲户电视移到新增隔墙前；乙户该处恢复客厅，取消农具外门、平台与缓坡。农具从甲户侧院进出。

门外平台1.50×2.40米。推车缓坡净宽1.10米、长5.40米，跨越450毫米高差。

坡度1:12，侧缘设低挡边；场地、排水、防滑及成品净空待深化。

每户储藏间 1.80 × 2.40米

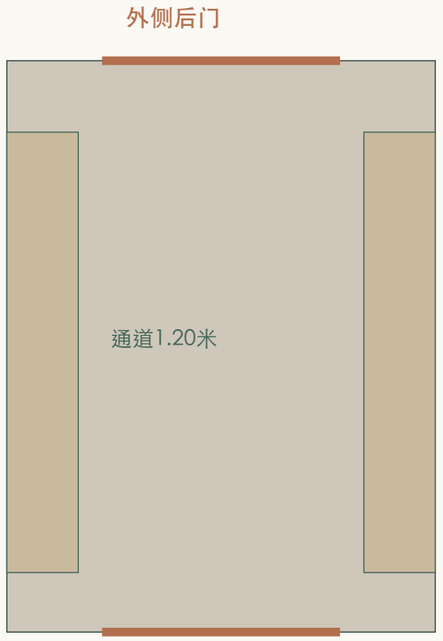

由室内进入

利用厨房旁原空置服务区，保留室内入口，北端新增外后门和高位通风窗；两侧约300毫米深搁架，中间1.20米模型通道。外门后为1.50米深平台与三级150毫米台阶。


宜存干货、折叠椅、节庆用品和清洁物料。农药、燃油等不与食品混放；喷雾器清洗、晾干后入农具间。

面积为轴线范围估算；净尺寸以正式设计为准。卧室14间、卫浴14处、厨房2间、日常餐厅2间及合厅20席保留。

季节与时间：拖动看光影

右侧两条连续滑杆；连接厅改整片固定景窗，三楼梯洞边改玻璃栏杆。

右侧控制 / 北京时间

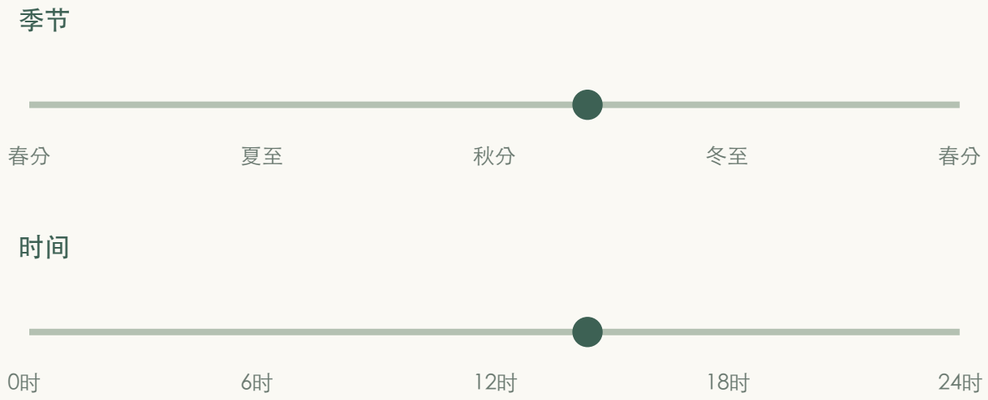


拖动季节，连续查看全年太阳位置；拖动时间，观察早晚方向、日照色温、阴影长度及夜间亮度变化。分享链接会保留所选季节与时间。

坐标：北纬26.745458°，东经112.056528°；北京时间UTC+8。沿用建筑南偏东约12.31°朝向，阳光按真北计算。

模型展示晴天太阳位置与几何遮挡；缺少实测山体、邻房和天气资料。剖切、隐藏屋顶或降低墙体时，界面标为“剖切光影示意”，不能据此判断实际室内采光。

太阳位置方法：NOAA通用方程


连接厅固定景窗

 

1.00 × 2.40米

连接厅前、后各一片固定玻璃，窗台0.55米、窗头2.95米；细框、无把手，不能点击开启。

三楼楼梯玻璃栏杆

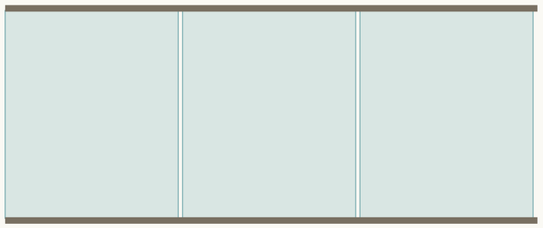


模型高度1.20米

三楼取消楼梯北侧整面隔墙；透明栏杆沿梯洞边设置，旁侧上楼出口保持敞开。走廊外墙、原柱和楼梯固定窗保留。

固定玻璃及栏杆的安全玻璃、构造、承载与锚固须正式设计。日照功能是方案展示工具，不是报审或规范日照分析。

三楼影音室：向天井侧南扩为L形

原约28.98平方米，增加约5.04平方米至34.02平方米；沿前排两柱围合，右侧公共走廊保留。

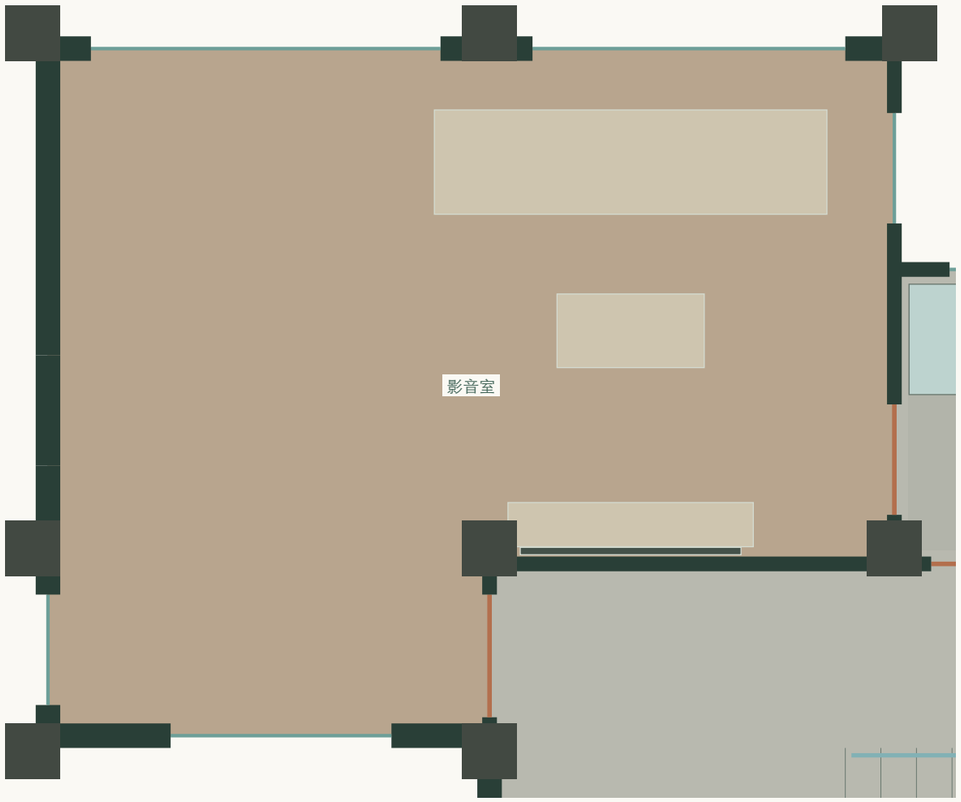

三层乙户局部 / 1:50（A3原尺寸打印）

墙、门、窗与家具一起调整

1. 拆旧南墙靠天井约3.60米的一段及原门；两柱之间形成新的南向围护，转角侧墙闭合，影音室保持独立。

2. 南窗恢复原1.80×1.85米分格，窗台1.00米、窗头2.85米；固定主玻璃配0.45米外开窄扇。其余5扇后排南向高窗沿用原分格。

3. 新入口位于转角侧墙，门洞1.00米，向影音室内开，避开楼梯到达及公共卫浴通道。

4. 电视贴右侧保留实墙，沙发与电视对正；原北向四折大窗、可切换卫浴及其双入口保留。

5. 不增楼板，不改屋顶或柱位；扩入部分由原楼板与主屋面覆盖。拆墙性质、梁下净高及新增围护荷载须正式核定。

地面连续采用浅橡木色木纹瓷质砖；转角扩出的区域可作自由活动空间。图示为同一模型平面，未据此完成结构承载或隔声设计。

14间卧室：七间双床，其余按房型配床

床垫长统一2.00米；七间双床房共14张1.20米床，全屋共21张床。门洞、卫浴及阳台保留。

房间	床垫规格（宽×长）	床头抽屉柜 / 宽×深	书桌（长×深）
甲1 / 1层	1张1.50×2.00米	1只 / 0.40×0.35米	1.00×0.40米
乙1 / 1层	1张1.50×2.00米	1只 / 0.40×0.35米	1.00×0.40米
甲2 / 2层	2张1.20×2.00米	1只 / 0.40×0.45米	1.10×0.45米
甲3 / 2层	1张1.80×2.00米	2只 / 0.40×0.35米	0.75×0.40米
甲4 / 2层	2张1.20×2.00米	1只 / 0.45×0.35米	1.00×0.40米
甲5 / 2层	1张2.00×2.00米	2只 / 0.45×0.35米	1.20×0.60米
乙2 / 2层	2张1.20×2.00米	1只 / 0.40×0.45米	1.10×0.45米
乙3 / 2层	1张1.80×2.00米	2只 / 0.40×0.35米	0.75×0.40米
乙4 / 2层	2张1.20×2.00米	1只 / 0.45×0.35米	1.00×0.40米
乙5 / 2层	1张2.00×2.00米	2只 / 0.45×0.35米	1.20×0.60米
甲6 / 3层	2张1.20×2.00米	1只 / 0.40×0.45米	1.10×0.45米
甲7 / 3层	1张1.80×2.00米	2只 / 0.40×0.35米	0.75×0.40米
甲8 / 3层	2张1.20×2.00米	1只 / 0.45×0.35米	1.00×0.40米
乙6 / 3层	2张1.20×2.00米	1只 / 0.40×0.45米	1.10×0.45米


1.20米为常见成品床垫宽度，不是必须统一采用的法定标准。薄床架外包长约2.05米、宽比床垫多约50毫米，采购时须按实际床架复核。

甲3、乙3、甲7各用一张1.80×2.00米床；甲2、乙2、甲4、乙4、甲6、甲8、乙6各用两张1.20×2.00米床，并列布置。每间卧室标签显示床垫尺寸。床头均有完整实墙，床头柜各两只抽屉；双床房共用柜，书桌及北阳台路线保留。成品家具与完成面净距须现场复核。


成品规格示例：IKEA中国120×200厘米床垫（非产品指定）

灯光：以灯带、局部灯具与低位光组织空间


卧室、客厅和影音室不用中央大吸顶灯；暖灰铜灯体、浅米灯罩，窄灯槽与常规型材控制施工复杂度。

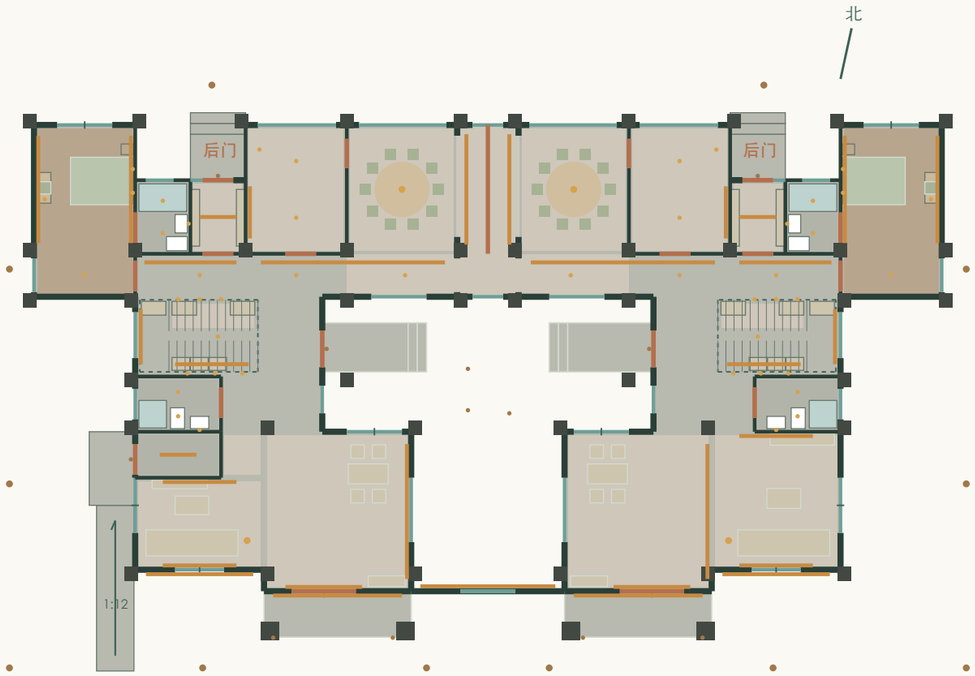

一层：客餐厅、厨房、庭院与入户路径

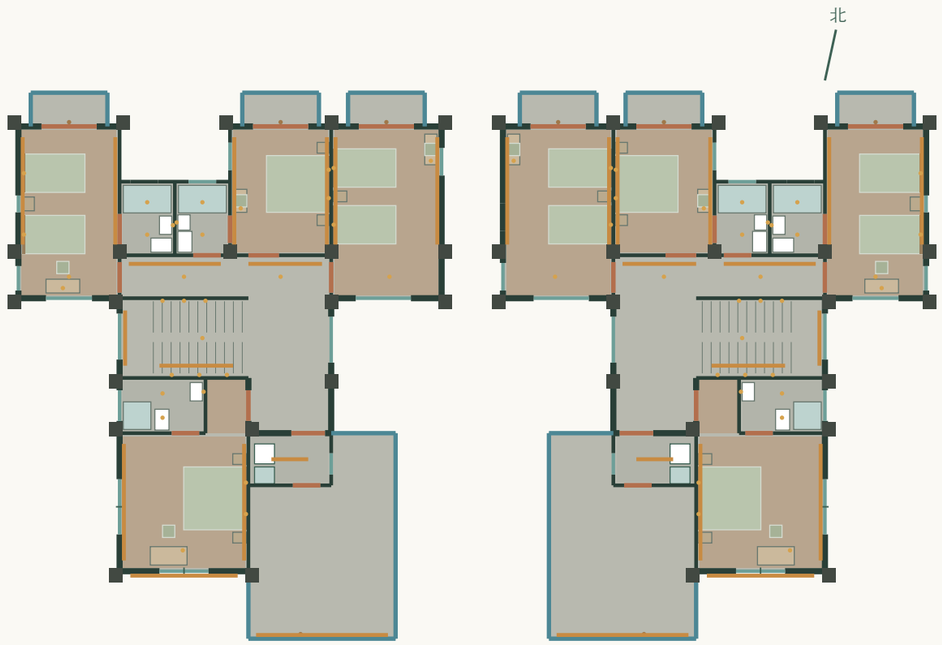

二层：卧室、阅读、洗衣与阳台

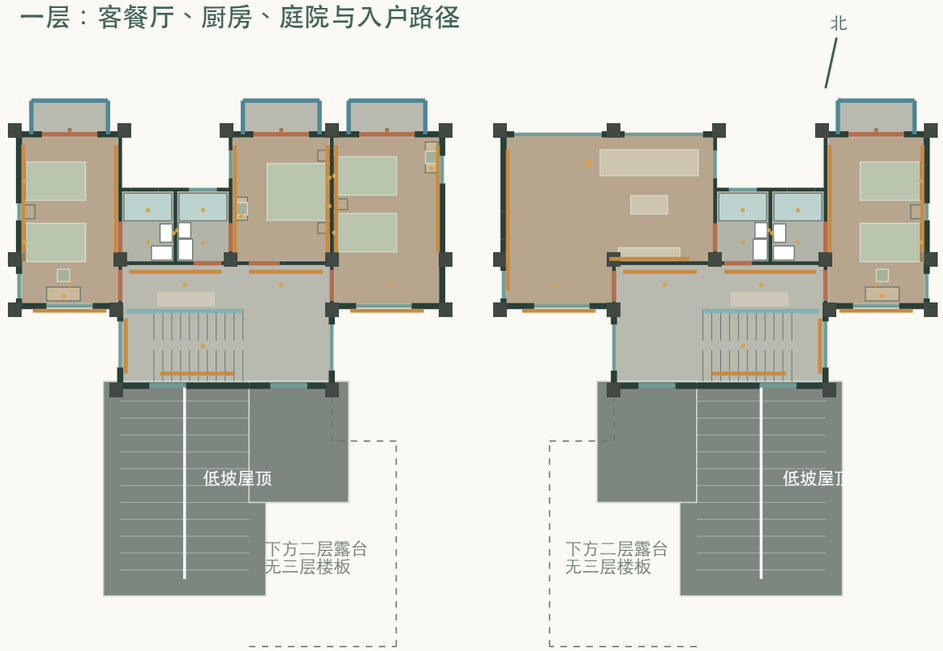

三层：卧室与影音室分层照明

用光与操作

金色线：隐藏灯带与工作灯；圆点：局部灯具及低位导光。图示按同一模型位置输出，非照明施工图。

卧室、客厅、影音室及室外建议2700K暖光；书桌、厨房和洗手台建议3000K工作光。床头阅读灯、台灯及3只落地灯独立使用，实际分路调光。

走廊连续线光与楼梯平台、踏步灯采用3000K；入户、露台、12只路径灯、3只树灯及花窗墙分层补光。室外选防眩、耐候产品，排水、线管与供电保护由正式设计落实。

右侧“夜景”切换至20点，也可滑动时间；灯具在傍晚渐亮，白天熄灭。夜景由Cycles计算遮挡与反射，网页固定烘焙；隔断移开工况，无照度、眩光或电气验算。

下载中文概念灯位表（坐标与色温）

9间侧卧室：沿柱线改门，纳入走廊尽端

二层平面作为示例；一层2间、二层4间、三层3间。建筑外轮廓、原柱和外窗保留。

二层：绿色区域纳入卧室，橙色为新侧门



绿色区域每间进深1.40米，来自原有顶走廊尽端；不新增建筑外轮廓。

公共通道仍连接楼梯、卫浴与其余卧室。原14间卧室、14处卫浴及21张床保留；移墙后的传力、隔墙锚固及门框与柱边关系由正式设计复核。

轴线面积对照（平方米）

卧室	原面积	调整后	增加
甲1（一层）	13.9	18.5	+4.6
乙1（一层）	13.9	18.5	+4.6
甲2（二层）	13.9	18.5	+4.6
甲4（二层）	15.1	20.2	+5.0
乙2（二层）	13.9	18.5	+4.6
乙4（二层）	15.1	20.2	+5.0
甲6（三层）	13.9	18.5	+4.6
甲8（三层）	15.1	20.2	+5.0
乙6（三层）	13.9	18.5	+4.6

新侧门洞口暂按1.00×2.35米；南侧铰接，向卧室内开，门口地面平接。门框安装后的实际净宽、柱边收口及五金须正式深化。

床、书桌、床头实墙、卫浴及北阳台入口保留。卧室地面连续铺木纹瓷砖，走廊灯带在新墙处截断并重新分区。

南北向墙线（模型坐标）

甲1／2／6：x=3.30米；乙1／2／6：x=26.30米。


甲4／8：x=10.20米；乙4：x=19.40米。

各新门y=11.28～12.28米；隔墙暂按120毫米。

四间双床房与错位采光窗

甲2、乙2、甲6、乙6调整；21张床、14间卧室与14处卫浴。影音室仅改北侧两扇大窗。

侧卧室南窗：1.50×1.85米

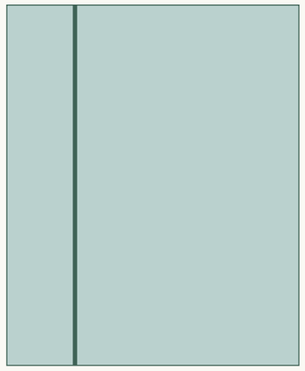

350毫米窄扇向外开启

窗台1.00米、窗头2.85米，与中间景窗齐平。两侧墙垛各约0.90米。主体玻璃固定，窄扇独立外开。

四间各两张1.20×2.00米床；甲户床头向西、乙户床头向东，均靠外侧实墙。

侧窗缩为0.55×1.60米并置于两床之间，共用床头柜；南窗下设1.10×0.45米书桌。床脚侧约1米通道，北阳台前约0.8米模型间距，成品与完成面须复核。

中间相对窗：甲北、乙南，共4扇




二、三层各按同样错位布置：甲栋保留北侧，乙栋保留南侧，其余4扇封实。

留下4扇统一900×1600毫米磨砂单扇外开窗，窗台850毫米、窗头2450毫米。

影音室北窗：中间固定、两侧开启



2.85×1.60米

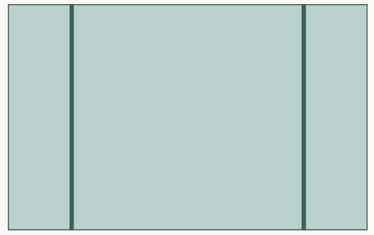

2.55×1.60米

原北窗洞口宽高保留，左右开启扇各0.45米，中间大块玻璃固定；两侧窄扇分别向外平开。南侧1.80米窗保持现有分格。

对应套卫封窗与排风

四间双床房各自对应的套卫封闭原小窗，公共及可切换卫浴窗保留。

预留独立机械排风至屋面，避免直接向对窗凹槽排气；风量、管径、止回、防水和检修由机电深化。

原柱及建筑外轮廓未改；新增窗洞的过梁、玻璃与五金需正式设计。